
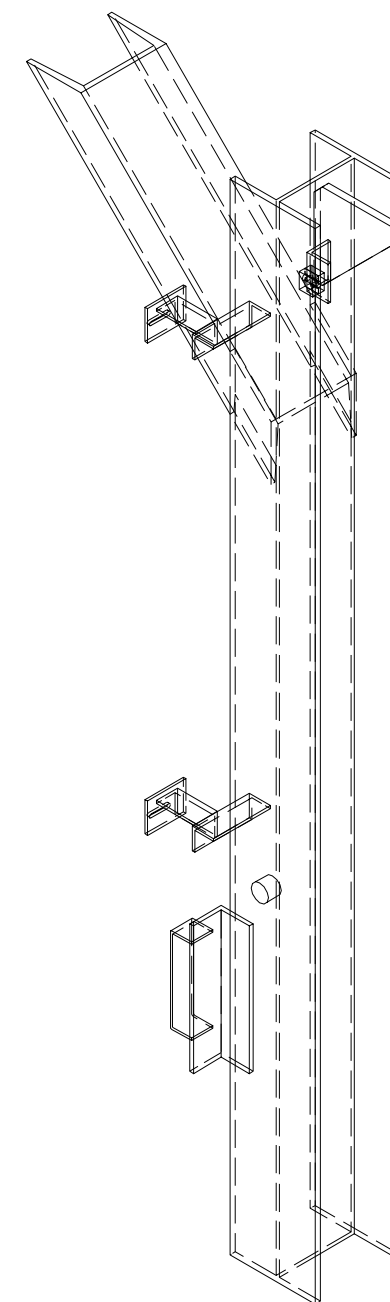
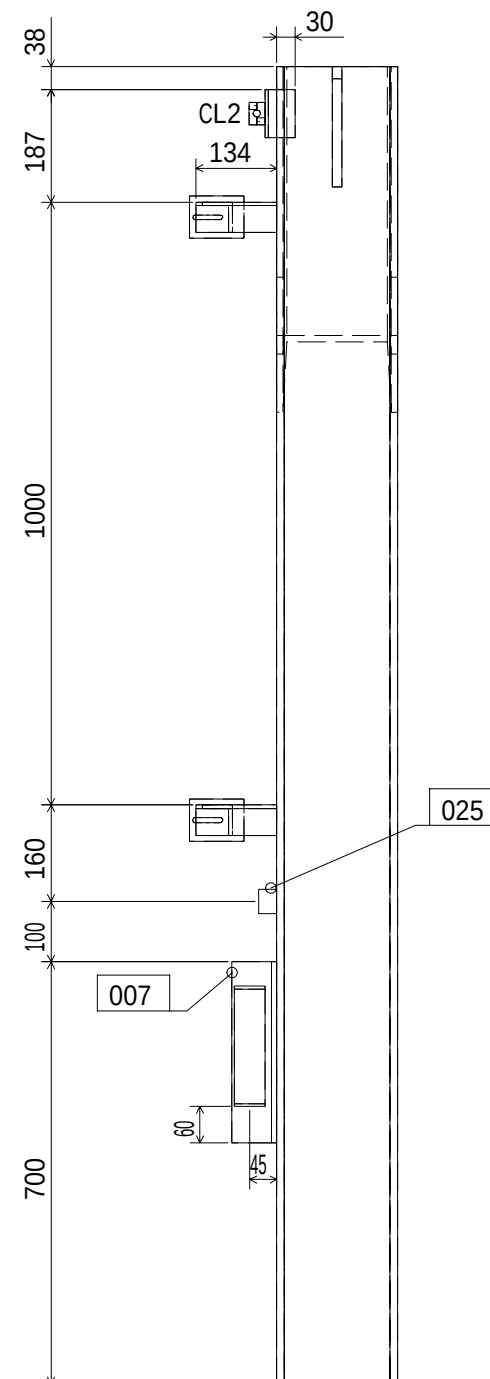
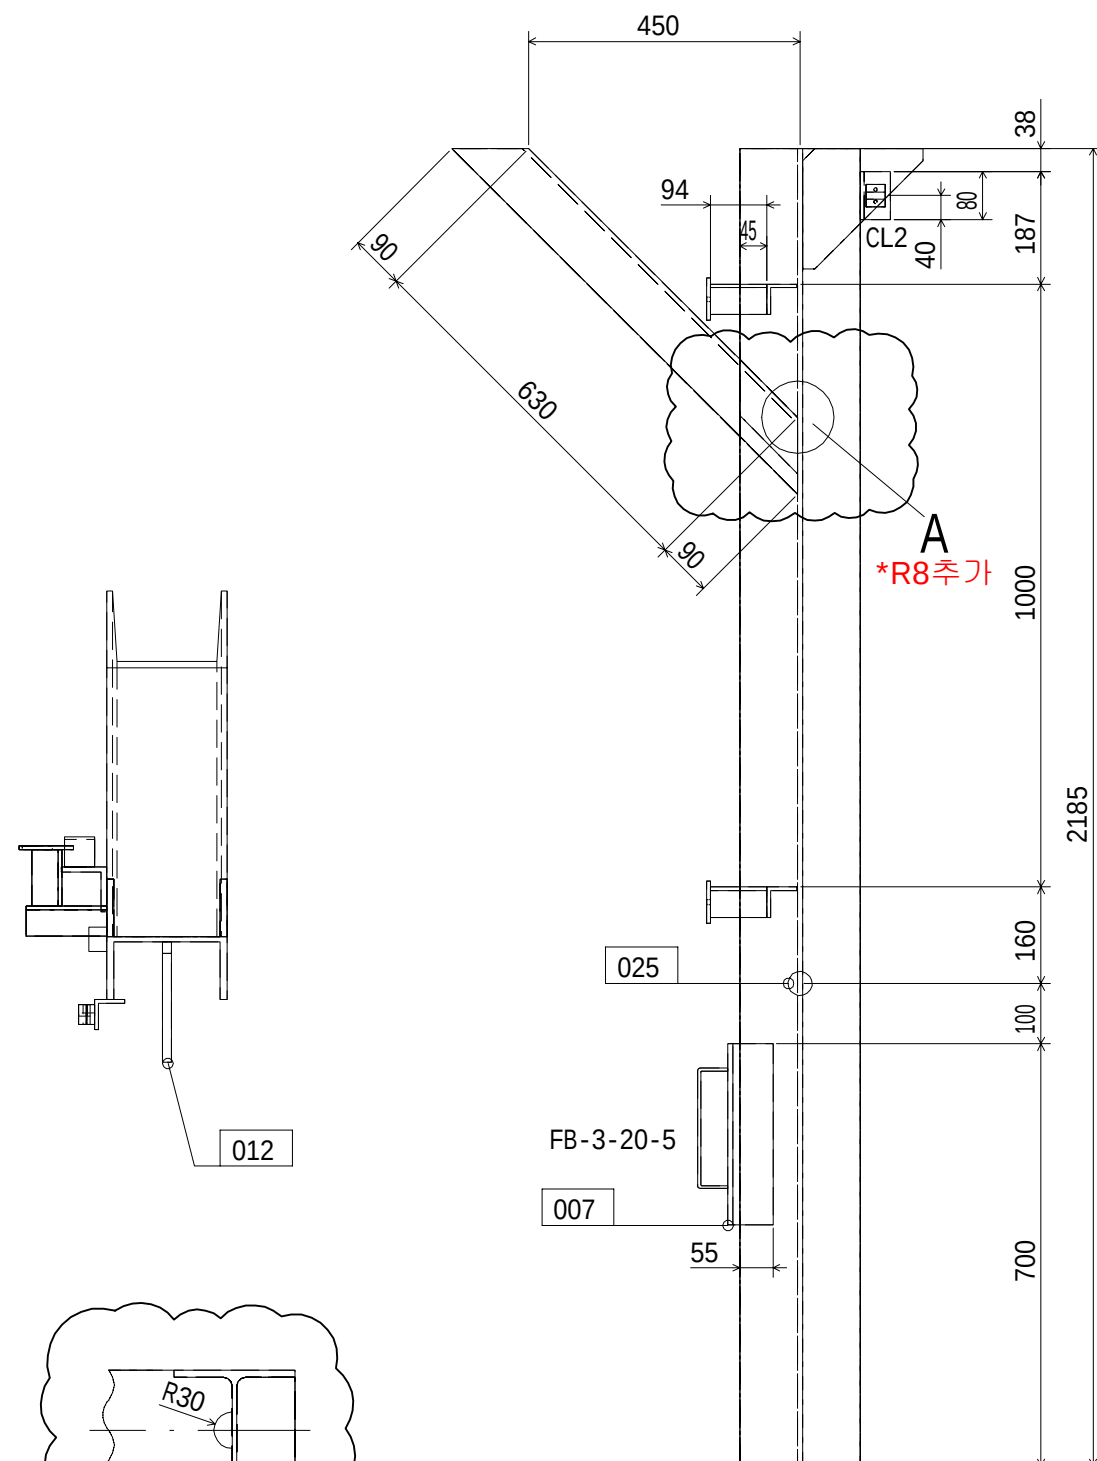


PIL-10

R8. 물빠짐홀 추가

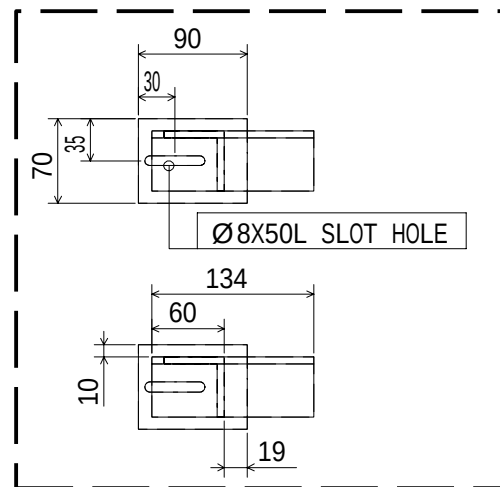

ALL NON MARKED SLOT HOLE Ø8X20L
ALL NON MARKED H-BEAMS H200x200
ALL NON MARKED U-BEAMS CH100x50
ALL NON MARKED L-BEAMS L50x50
ALL NON MARKED STIFFENER FOR H200x200

001
006
008
009

DETAIL : A

R8.260209추가

APPROVED 김 감 진	PROJECT NO. D2585 3LP165		
CHECKED 김 영 광	NAME OF DRAWING		
DRAWN 강 지 해	STEEL STRUCTURE SUPPORTS & PILARS		
TEL. NO. +82-51-260-5640			
DRAWING NO. SB-	CLASS DNV	SCALE .	☐
SUNBO UNITECH CO., LTD.			