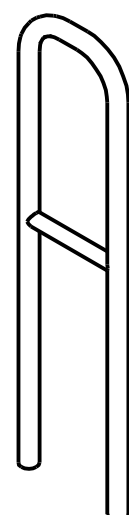
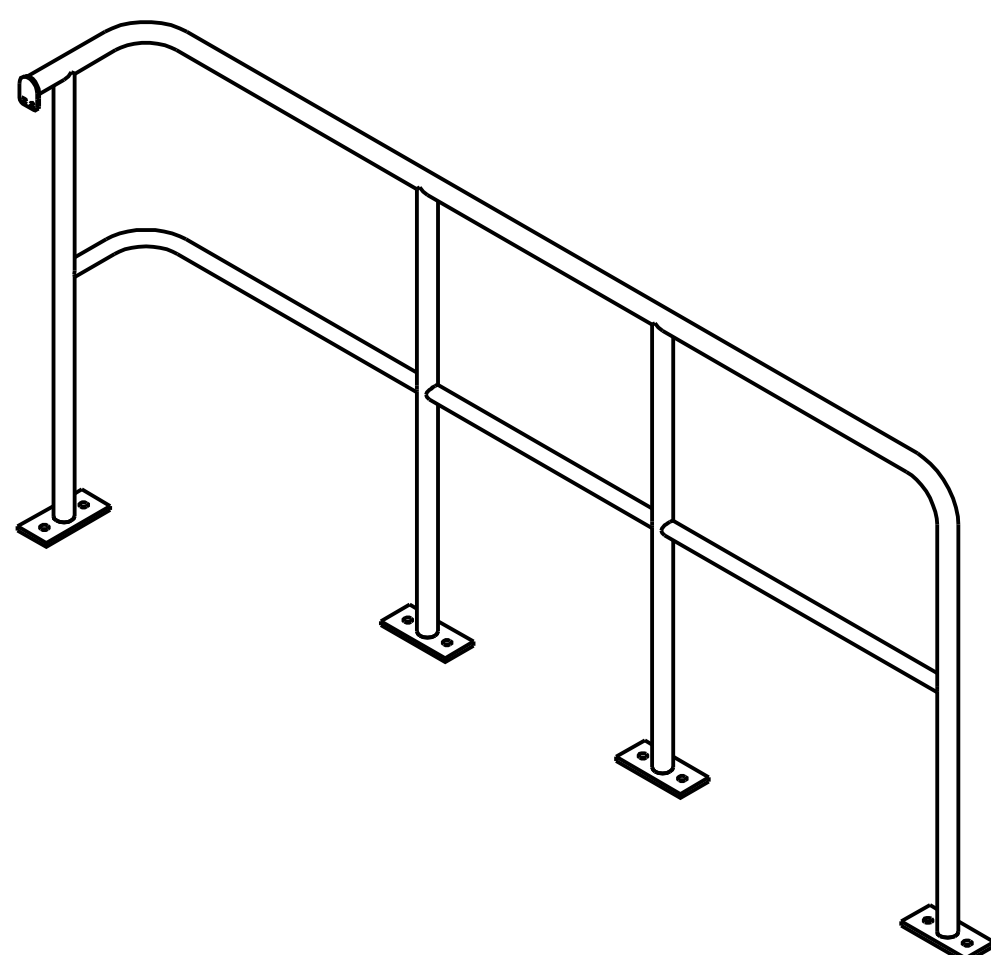
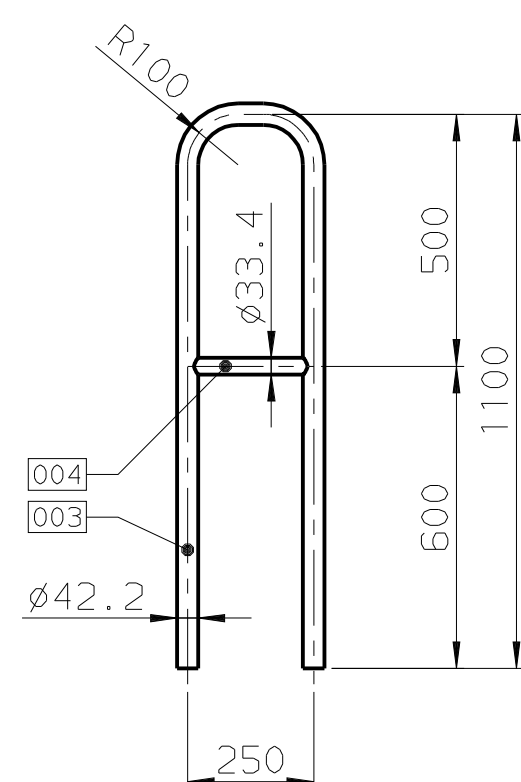
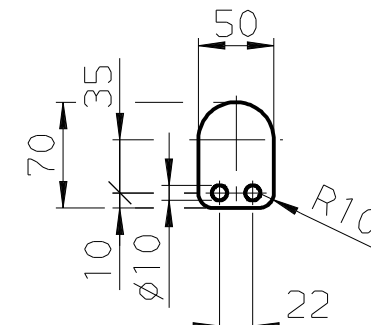
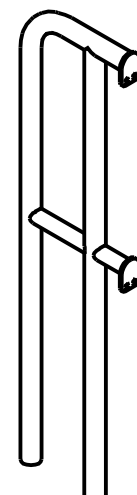
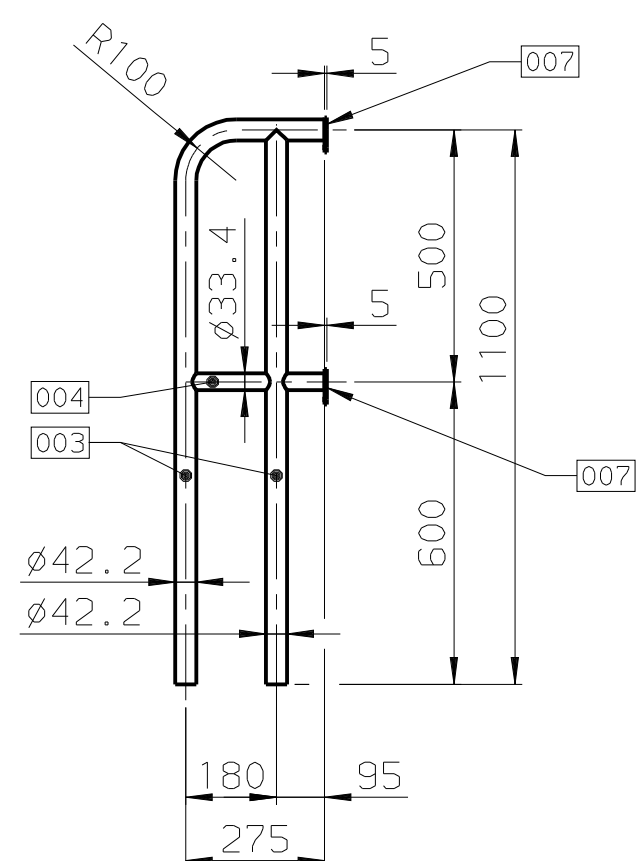


RAILING 4

RAILING 7

a	b	c	d	e	f	g	h	i	j	k	l	m	n	o	p	q	r	s	t	u	v	w	x	y	z														
1	2	3	4	5	6	7	8	9	10	11	12	13	14	15	16	17	18	19	20	21	22	23	24	25	26														
Name		Date		Name		Date		Name		Date		Name		Date		Name		Date		Name		Date		Name		Date													
Supp.pts List										Design group										 																			
Replaced by										Subst. for										Orig. scale 1:15																			
SLP250V-SA										STEEL STRUCTURE L2 RAILING AND GRATING MABY-Glo - NON-LUBE COMP. ITEM NO. : C-001										Drawn: 13-07-2022 TONELLI_M																			
																				Verified: 15-09-2023 SABOGAL_A																			
																				Standards conform:																			
L-0184 ASME										Part-No.										Bar - Code																			
CAD-Drawing																																							
 Borchhardt Hampt										E										0-125.619.962										4 - d d									