


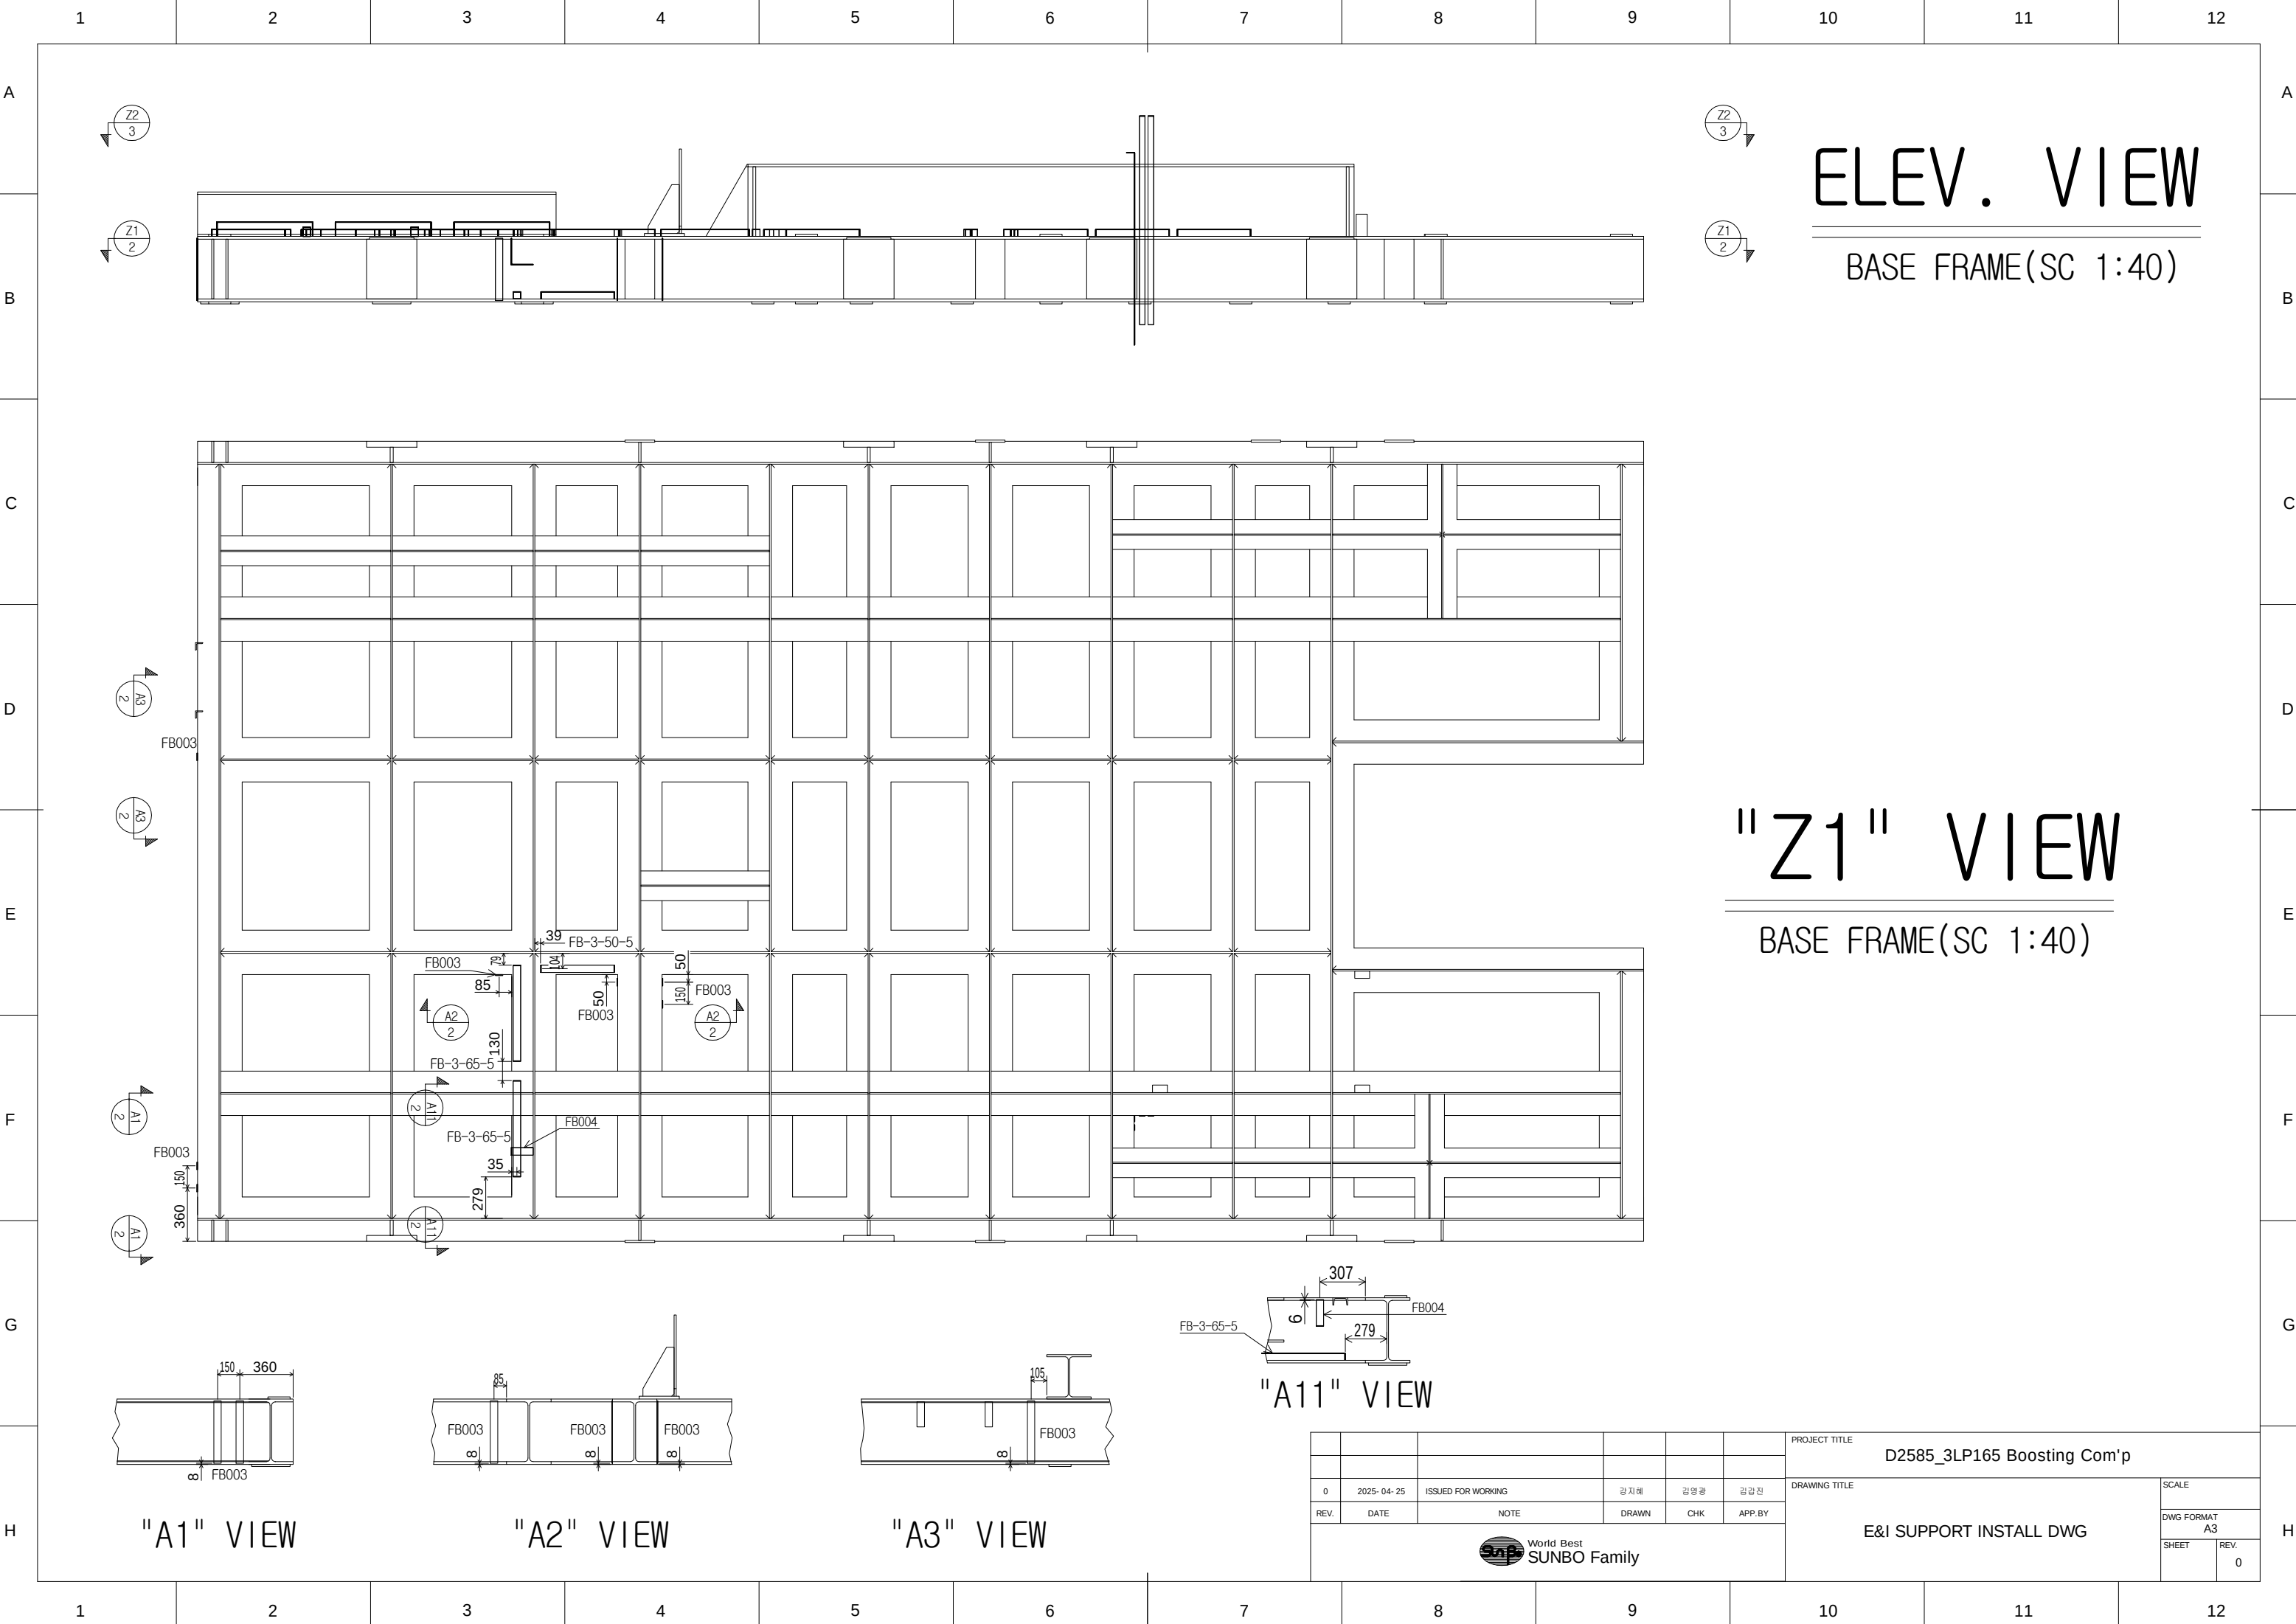

ELEV. VIEW

BASE FRAME(SC 1:40)

"Z1" VIEW

BASE FRAME(SC 1:40)

"A1" VIEW

"A2" VIEW

"A3" VIEW

"A11" VIEW

						PROJECT TITLE				D2585_3LP165 Boosting Com'p				
0	2025- 04- 25	ISSUED FOR WORKING		강지혜	김영광	김갑진	DRAWING TITLE				SCALE			
REV.	DATE	NOTE		DRAWN	CHK	APP.BY	E&I SUPPORT INSTALL DWG				DWG FORMAT A3			
											SHEET		REV. 0	