
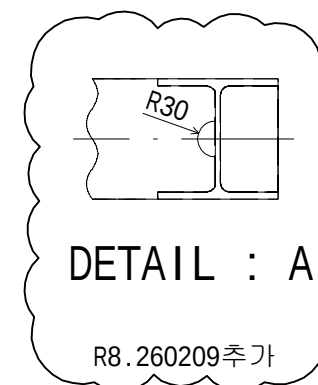
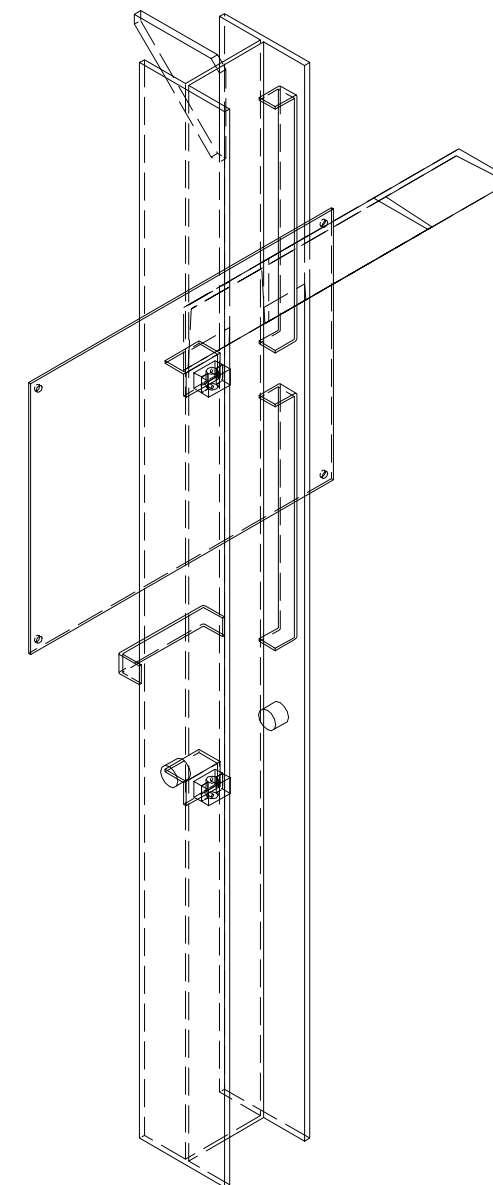
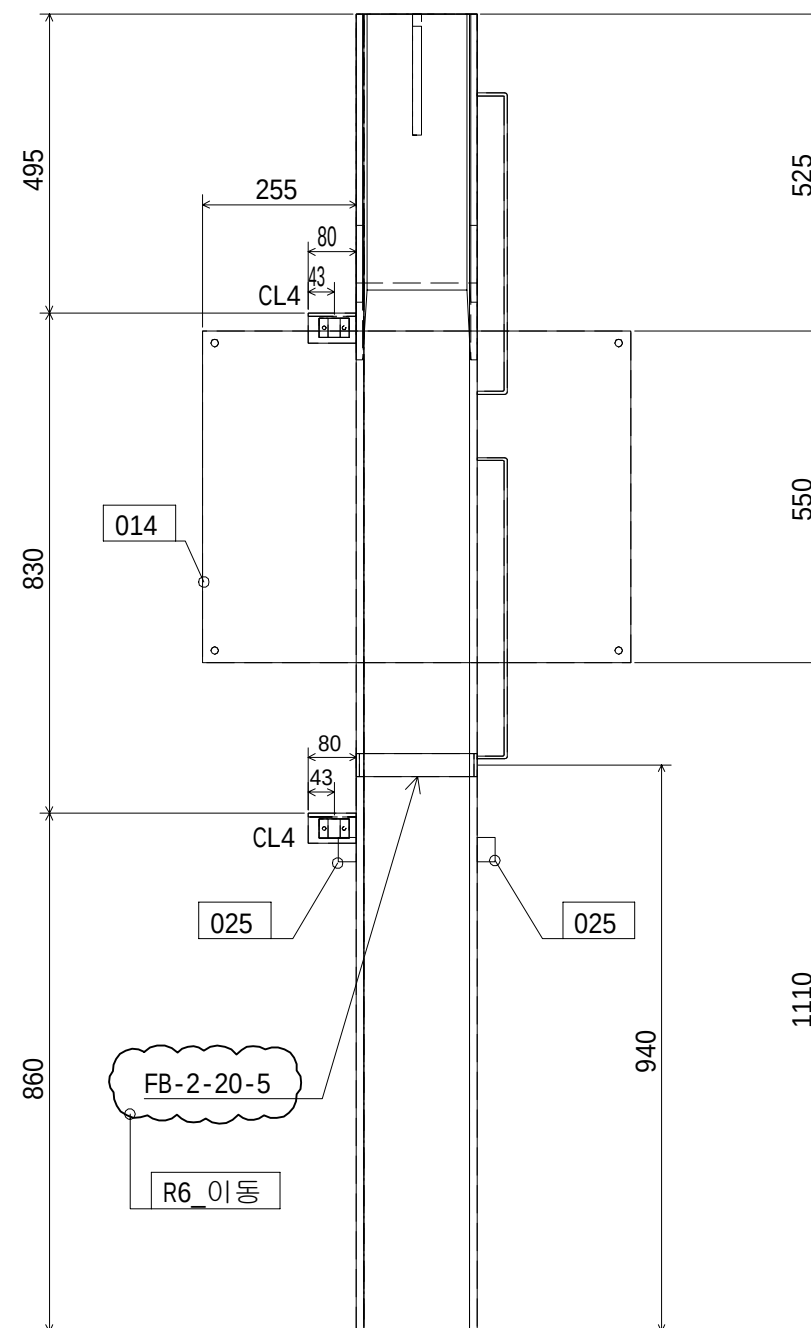


PIL-09

R8. 물빠짐홀 추가

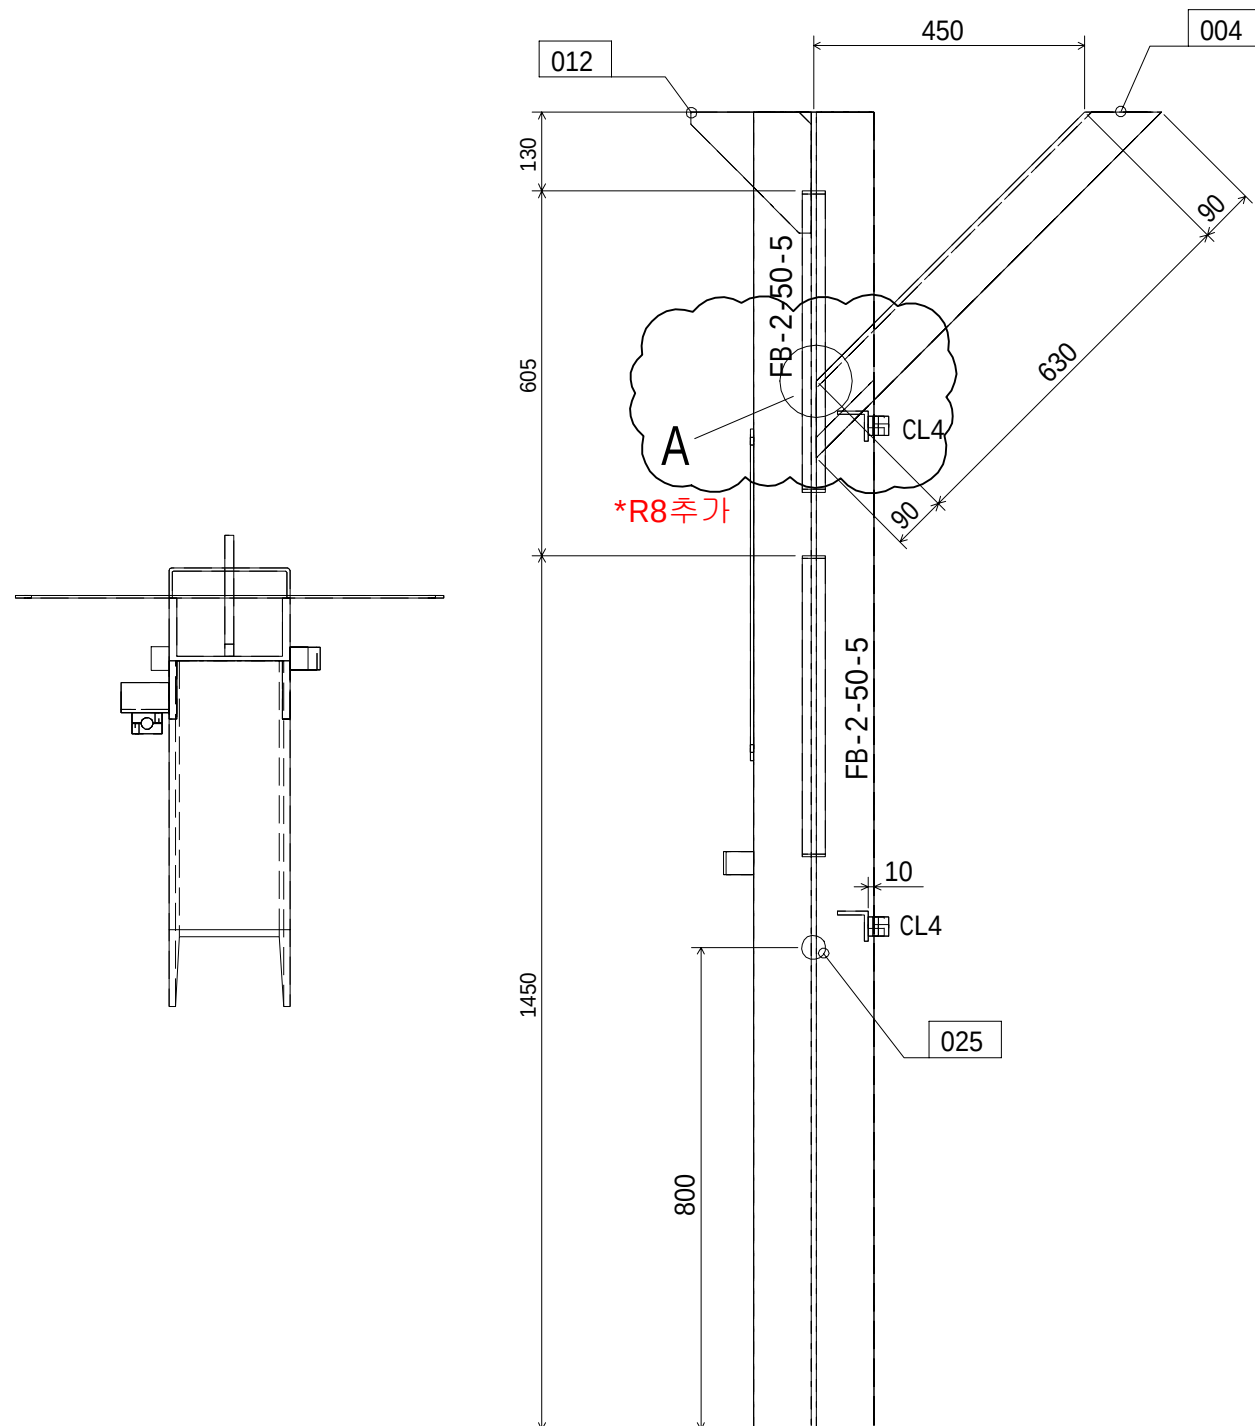

ALL NON MARKED SLOT HOLE Ø8X20L
 ALL NON MARKED H-BEAMS H200x200
 ALL NON MARKED U-BEAMS CH100x50
 ALL NON MARKED L-BEAMS L50x50
 ALL NON MARKED STIFFENER FOR H200x200

001
 006
 008
 009

APPROVED 김 감 진	PROJECT NO. D2585 3LP165
CHECKED 김 영 광	NAME OF DRAWING
DRAWN 강 지 해	STEEL STRUCTURE SUPPORTS & PILARS
TEL. NO. +82-51-260-5640	CLASS DNV
DRAWING NO. SB-	SCALE .
SUNBO UNITECH CO., LTD.	