
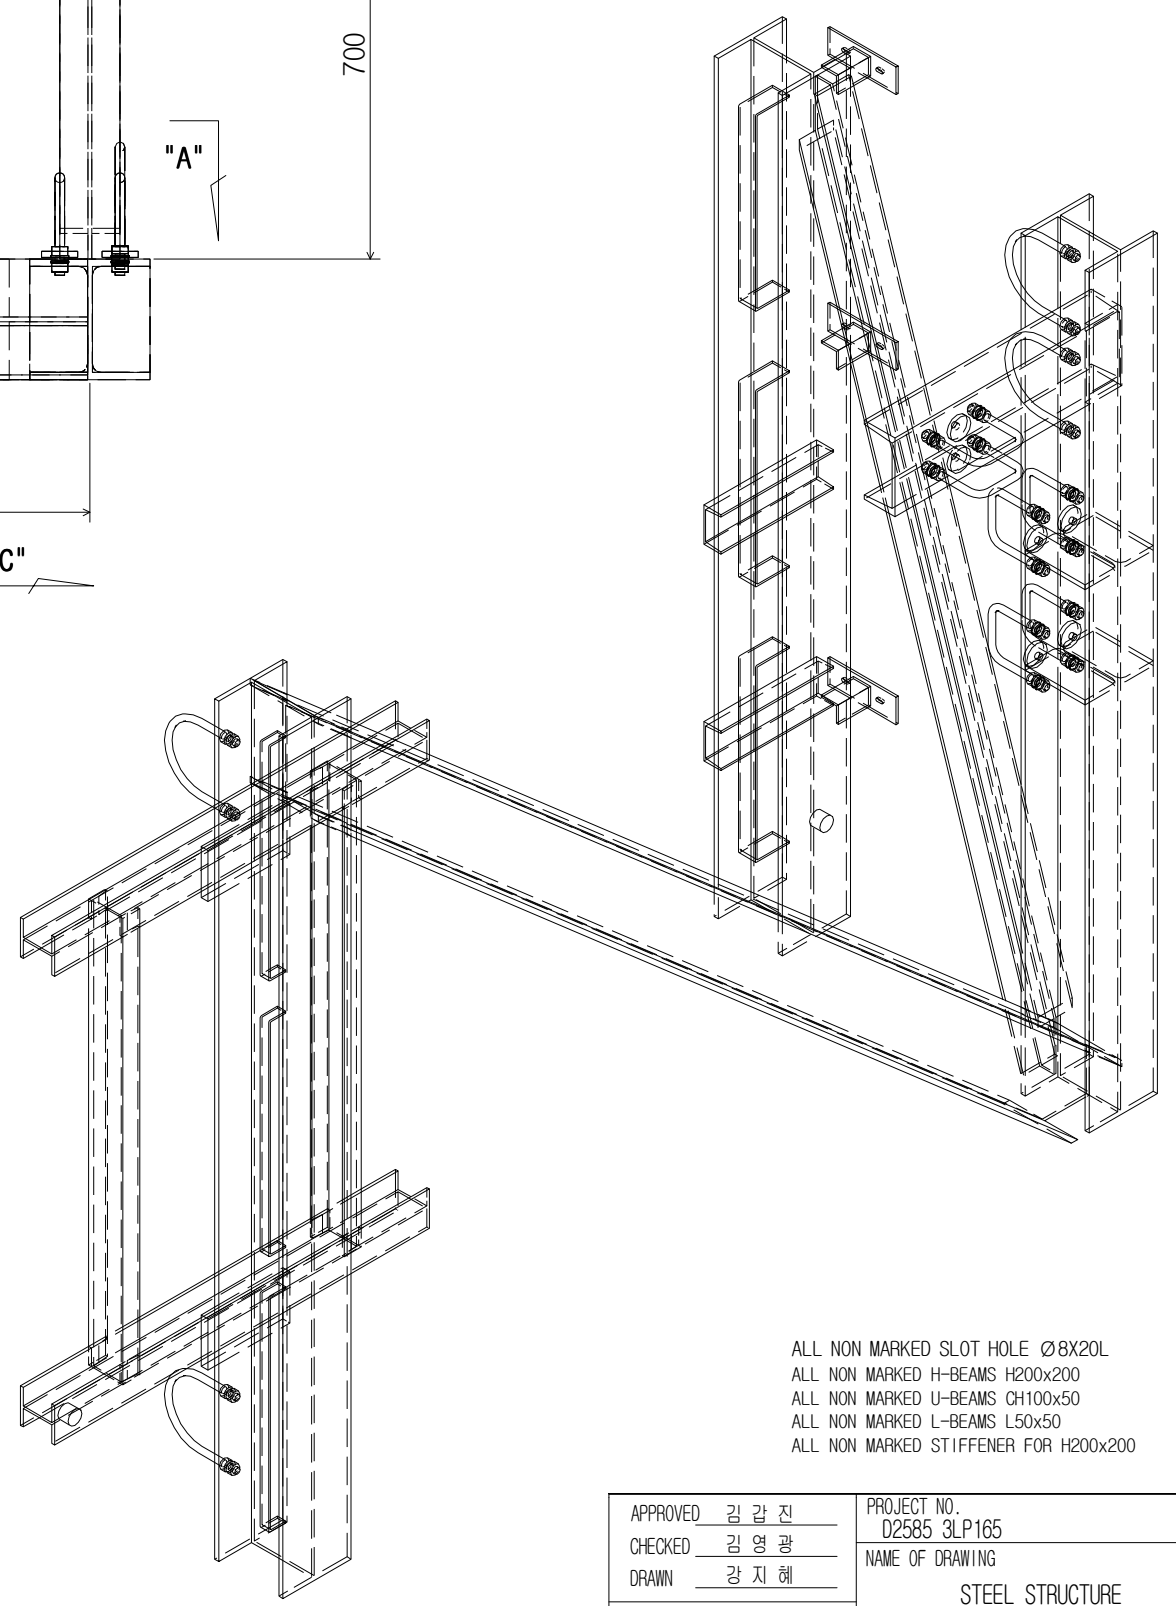
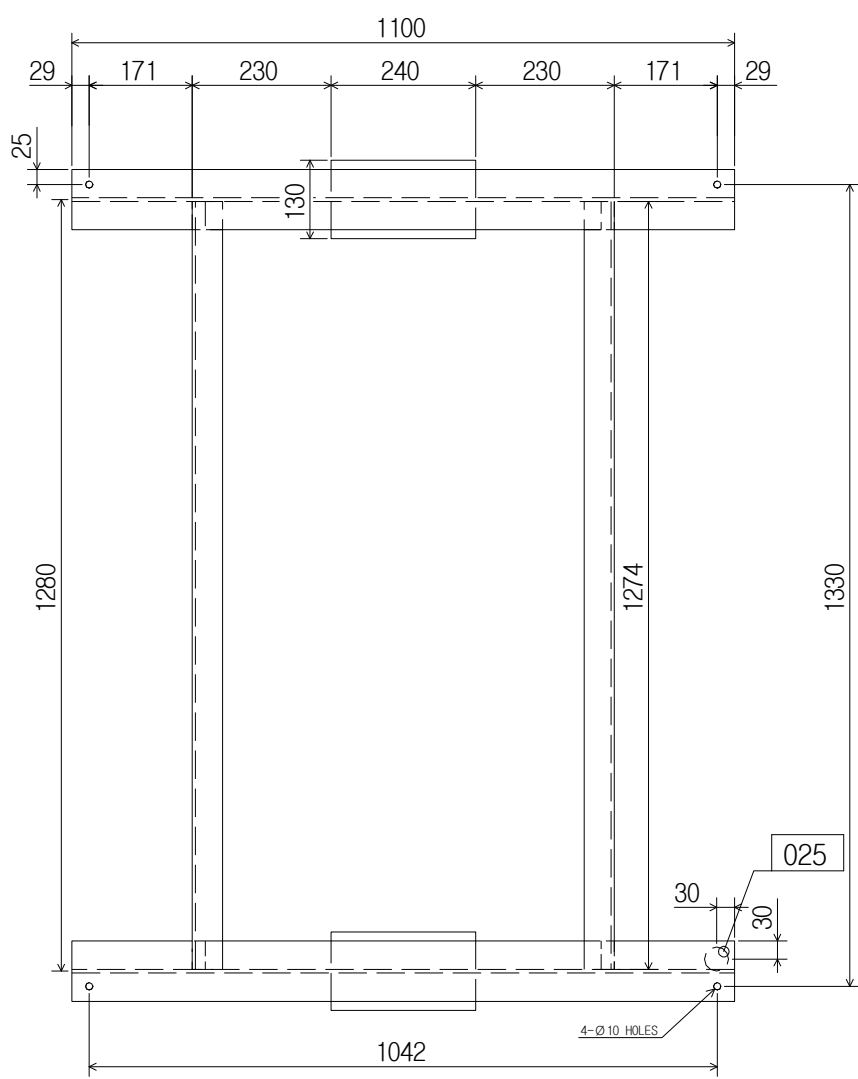


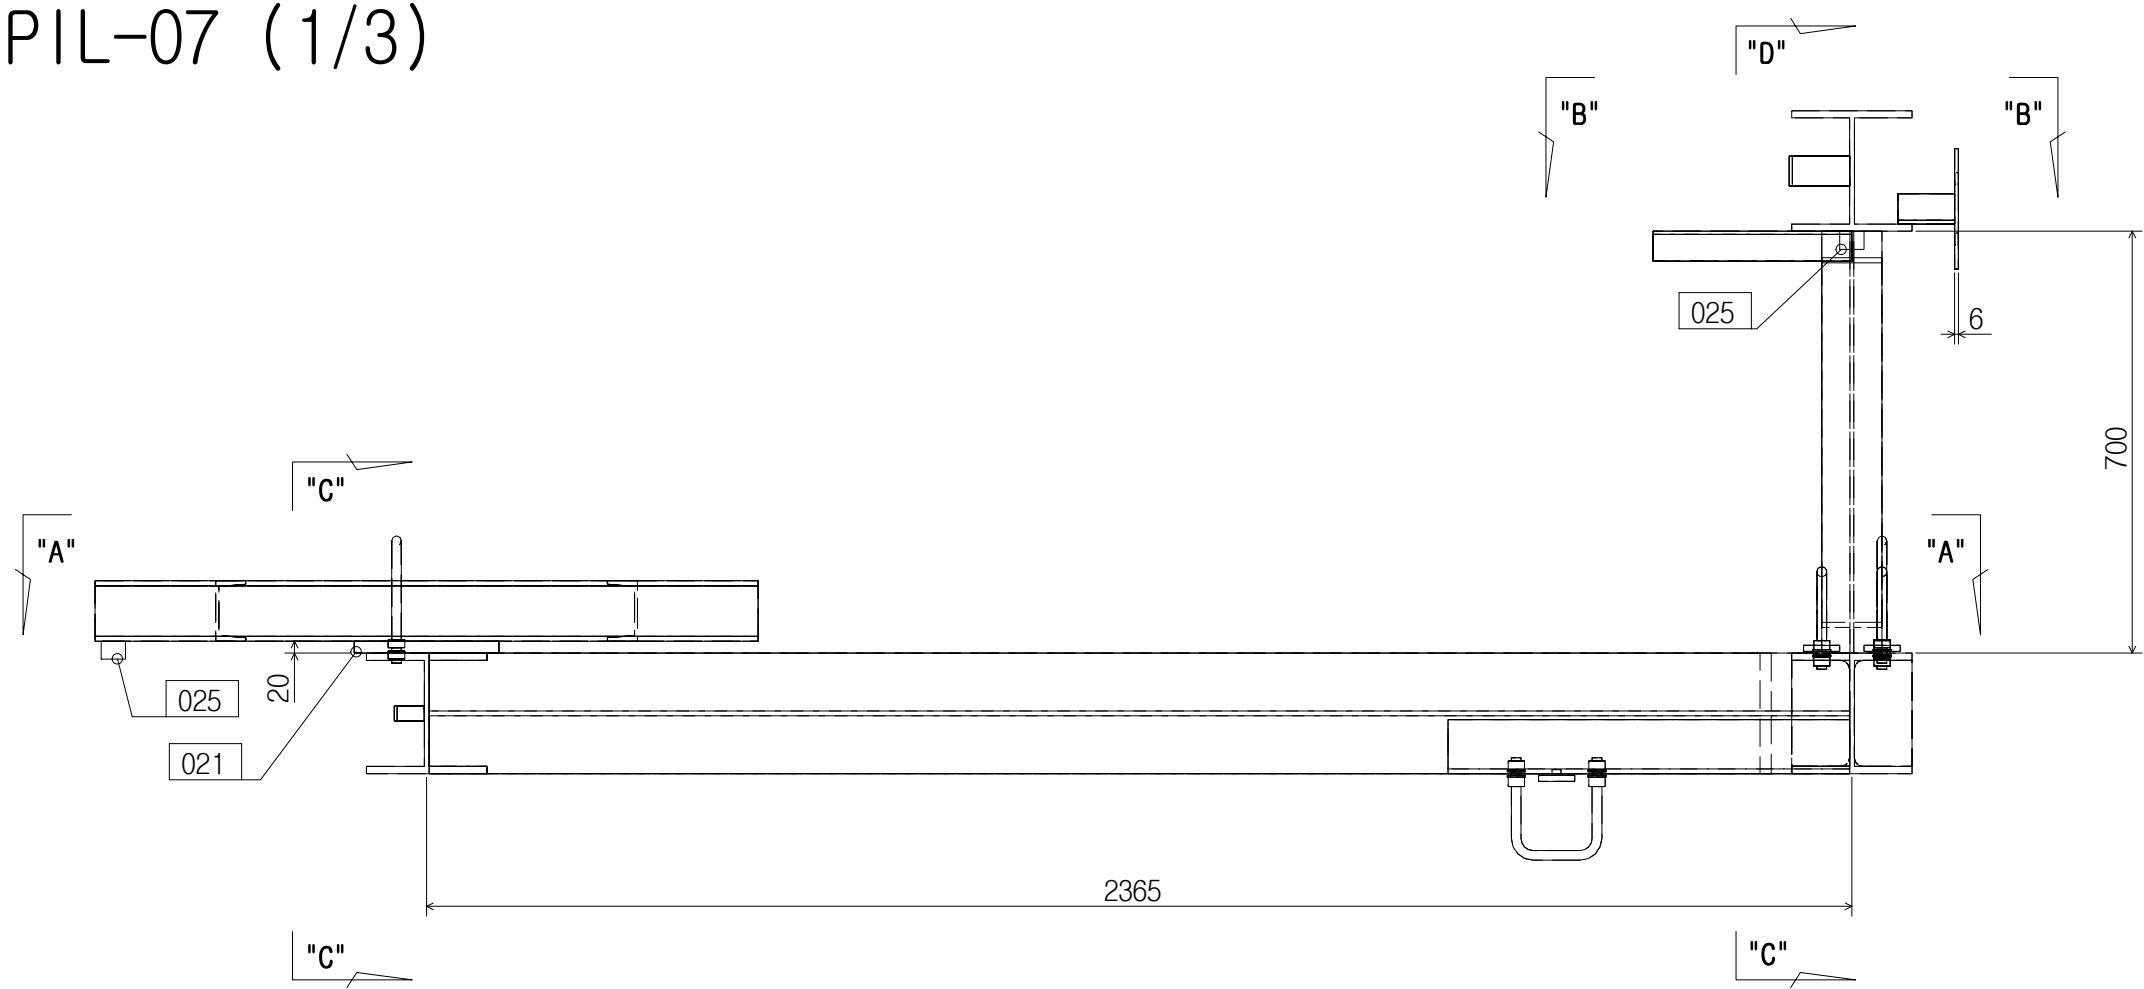

ALL NON MARKED SLOT HOLE Ø8X20L
ALL NON MARKED H-BEAMS H200x200
ALL NON MARKED U-BEAMS CH100x50
ALL NON MARKED L-BEAMS L50x50
ALL NON MARKED STIFFENER FOR H200x200

001
006
008
009

APPROVED 김갑진	PROJECT NO. D2585 3LP165
CHECKED 김영광	NAME OF DRAWING STEEL STRUCTURE
DRAWN 강지혜	SUPPORTS & PILARS
TEL. NO. +82-51-260-5640	CLASS DNV
DRAWING NO. SB-	SCALE -
SUNBO UNITECH CO., LTD.	