


ELEV. VIEW

TOP FRAME(SC 1:30)

"Z3" VIEW

TOP FRAME(SC 1:30)
(비정규 BASE)

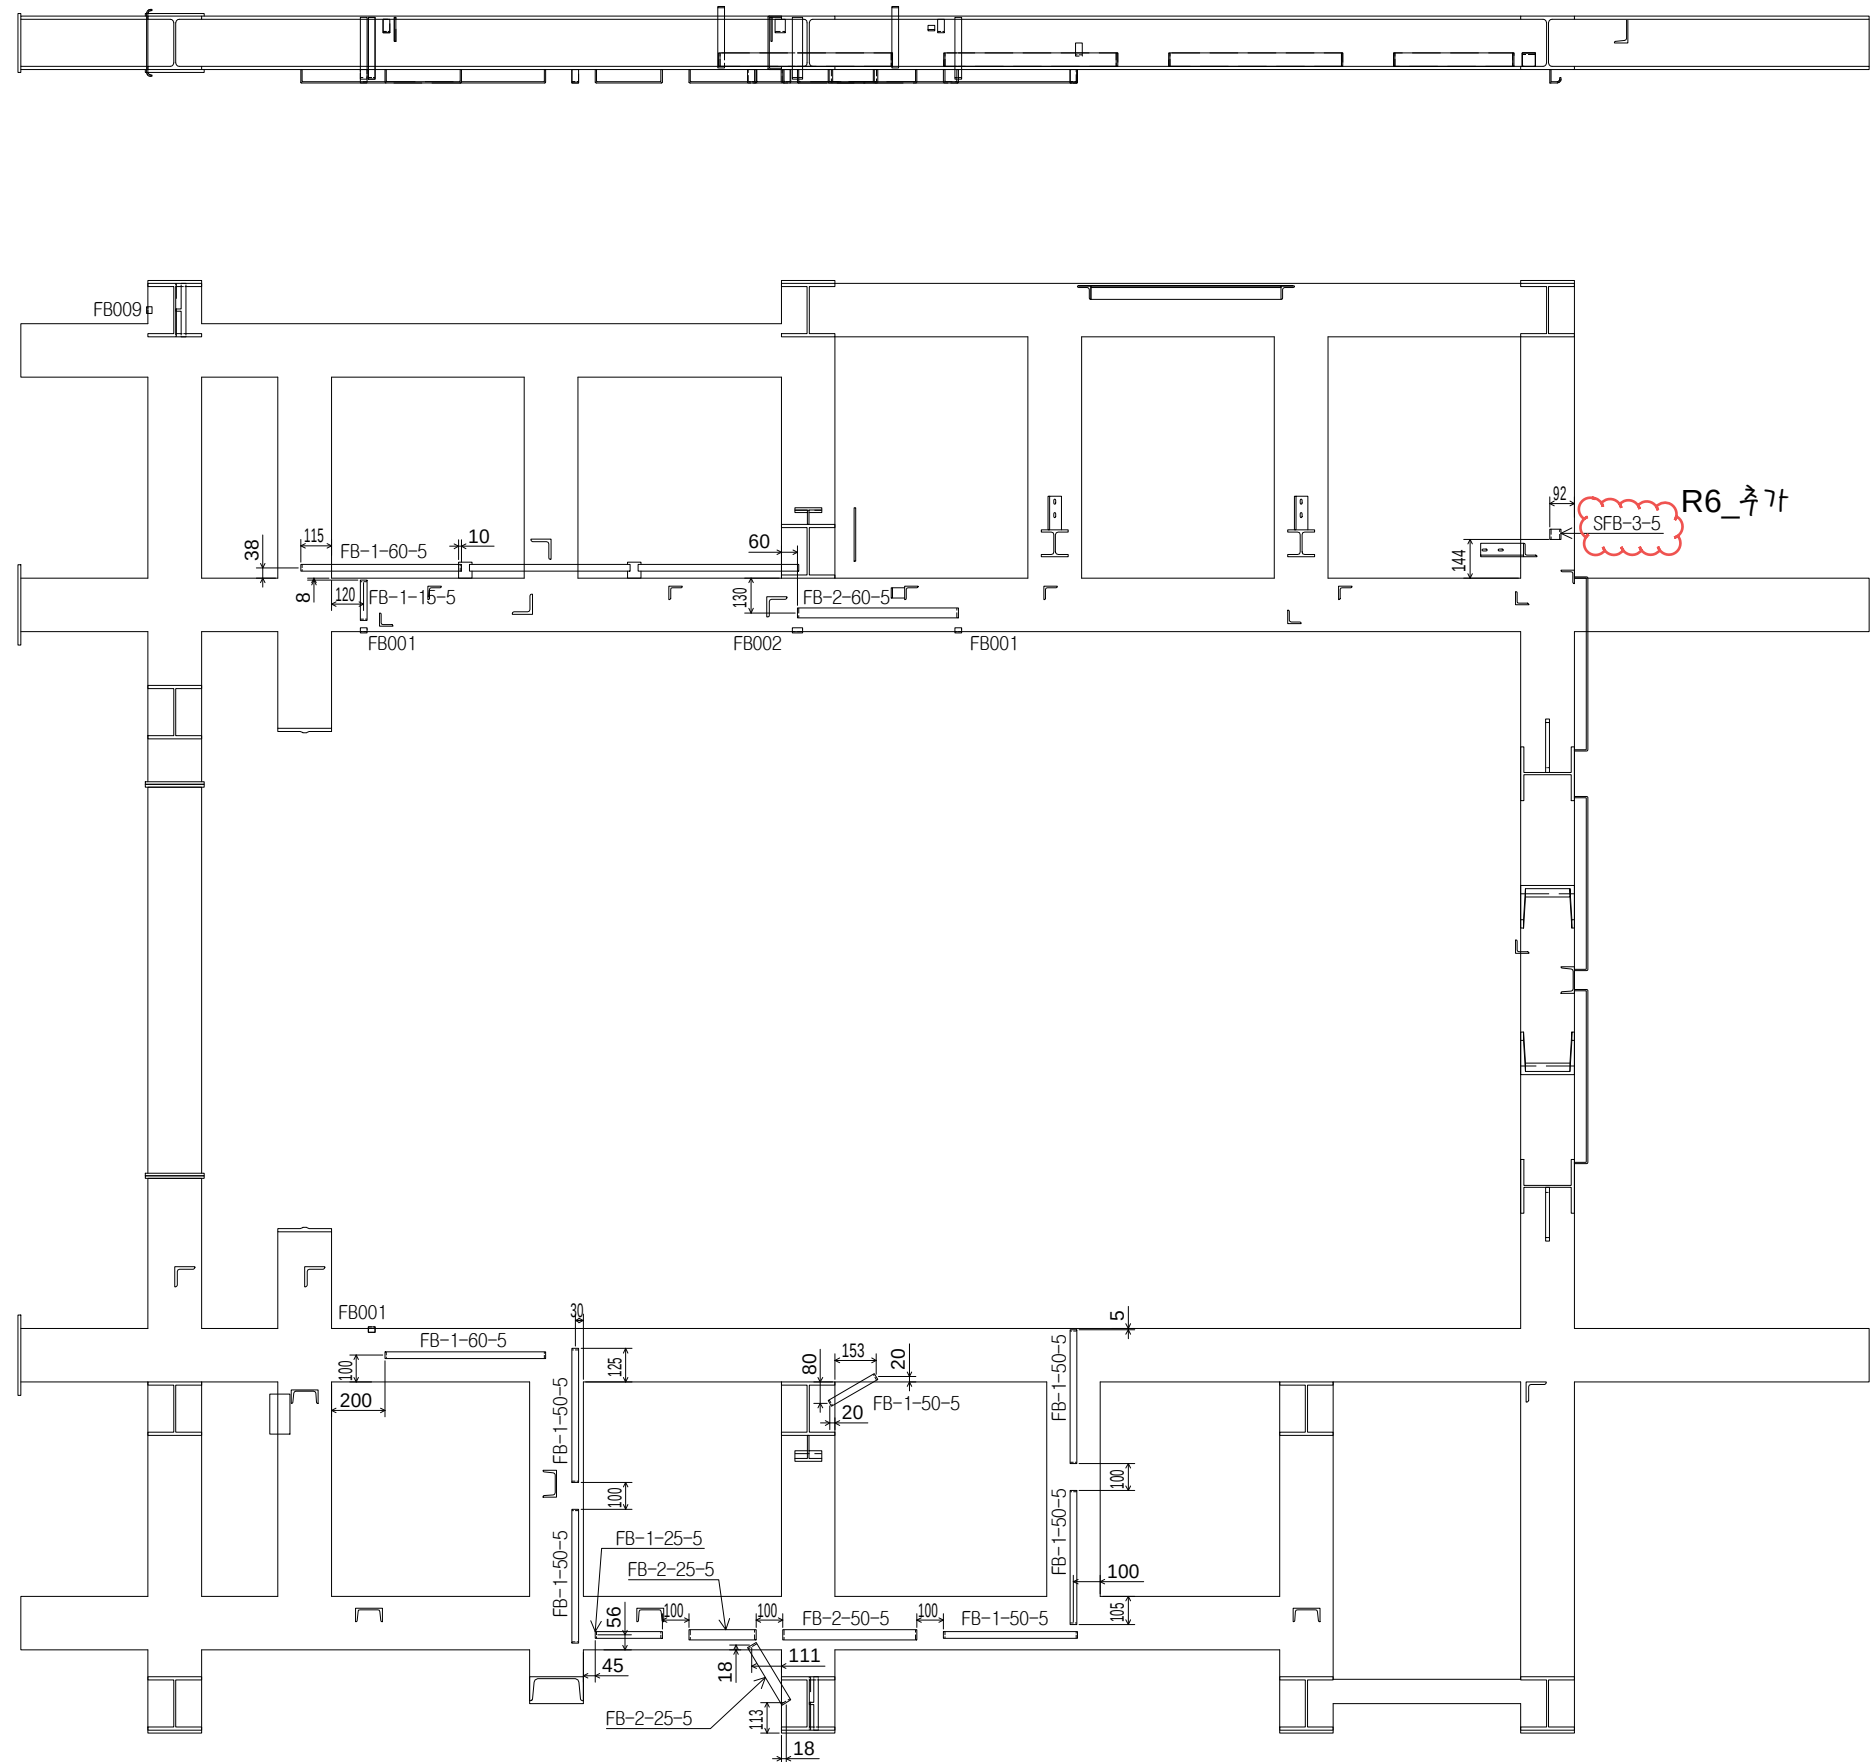

						PROJECT TITLE D2585_3LP165 Boosting Com'p				
0	2025-04-25	ISSUED FOR WORKING	강지혜	김영광	김갑진	DRAWING TITLE E&I SUPPORT INSTALL DWG			SCALE	
REV.	DATE	NOTE	DRAWN	CHK	APP.BY				DWG FORMAT A3	
 World Best SUNBO Family									SHEET	REV. 0