Drawing 0-125.629.716

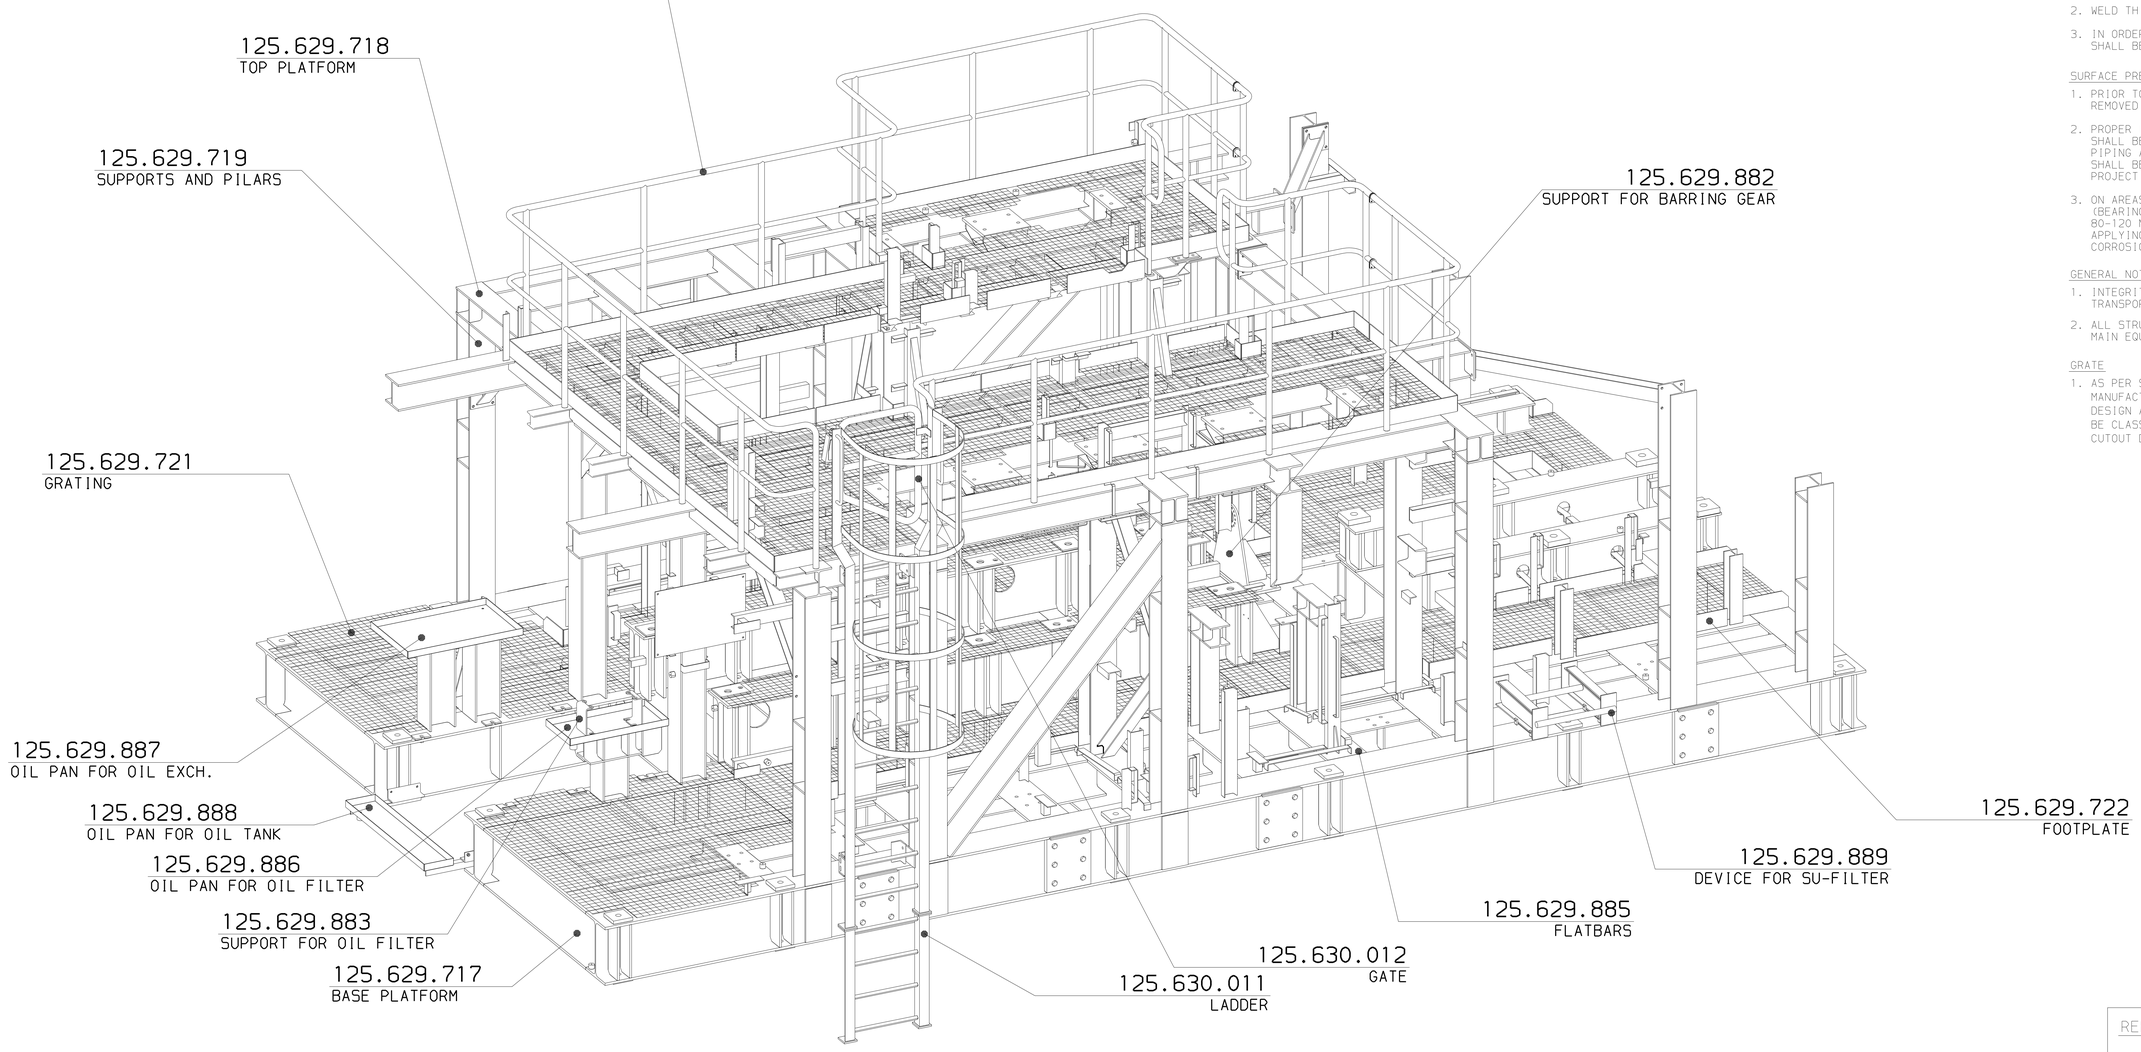

SCOPE OF SUPPLY

1. FOUNDATION BOLTS FOR FIXATION OF MODULES TO DECK STRUCTURE SUPPLIED BY SKIDDER, EXCEPT COMPRESSOR AND MOTOR BOLTS, SEE FOUNDATION DWG FOR DETAILS

WELDING OF PIPE SUPPORTS

1. WELDING OF PIPE SUPPORTS AND STEEL CONSTRUCTION SHALL BE DONE ACC. TO EN288 OR ASME IX.
2. WELD THICKNESS SHALL BE ACC. TO BELOW SHOWN WELDING DETAIL.
3. IN ORDER TO PREVENT RUSTING THE JOINTS BETWEEN TWO BEAMS SHALL BE CONTINUOUSLY WELDED.

SURFACE PREPARATION AND PAINTING

1. PRIOR TO FINAL PAINTING ALL RUST MUST BE CAREFULLY REMOVED FROM ALL CARBON STEEL BEAMS BY SAND BLASTING.
2. PROPER INTERMEDIATE AND FINAL PAINTING OF ALL SUPPORTS SHALL BE DONE ONLY AFTER THE WELDING AND ERECTION OF ALL PIPING AND SUPPORTS HAVE BEEN COMPLETLY FINISHED. PAINTING SHALL BE DONE BY PACKAGER ACC. SPECIFICATION DESCRIBED IN PROJECT SPECIFIC CLIENT INFO SHEET FOR COMPRESSOR MODULES.
3. ON AREAS MARKED WITH (*) AVOID EXCESSIVE PAINT LAYERS (BEARING SURFACE OF WASHERS). RECOMMENDED LAYER THICKNESS 80-120 MICRONS. MASK SURFACE AREA OF DIAMETER 80mm BEFORE APPLYING INTER LAYER AND TOP COATING. APPLY TEMPORARY CORROSION PROTECTION WITH TECTYL® 506 AFTER FINAL PAINTING.

GENERAL NOTE

1. INTEGRITY OF SKID MUST BE ENSURED DURING LIFTING AND TRANSPORT.
2. ALL STRUCTURAL MOUNTING ELEMENTS (BOLTS, NUTS, SCREWS) AND MAIN EQUIPMENT FIXATION SHALL BE PTFE COATED (XYLAN BLUE).

GRATE

1. AS PER SPECIFICATION TSP 2057179 CLAUSE 6.6. MANUFACTURER SHALL PREPARE ALL NECESSARY DRAWINGS FOR DESIGN AND FABRICATION OF MODULES. GRATING SEGMENTS SHALL BE CLASS SOCIETY APPROVED. NECESSARY OPENINGS ETC. SHALL BE CUTOUT DURING FINAL ASSEMBLY PHASE.

Burckhardt Compression

FOR INFORMATION

Changes until final documentation status may occur and are not recoverable from Burckhardt Compression.

IMPORTANT NOTE:

FLATTENING / STRAIGHTENING OF MODULE REQUIRED AFTER WELDING, SO THAT SUPPORT POINTS OF MODULE ARE WITHIN ± 2mm.

REFERENCE DRAWINGS

GEN. ARRANGEMENT OVER ALL	DWG.NO. 0-125.627.009
GEN. ARRANGEMENT ELEC. INTERFACE	DWG.NO. 0-125.629.175
GEN. ARRANGEMENT LIFTING	DWG.NO. 0-125.629.097
FOUNDATION	DWG.NO. 0-125.627.282

STEELWORK DRAWINGS

STEEL STRUCTURE OVERVIEW	DWG.NO. 0-125.629.716
STEEL STRUCTURE BASE PLATFORM	DWG.NO. 0-125.629.717
STEEL STRUCTURE TOP PLATFORM	DWG.NO. 0-125.629.718
STEEL STRUCTURE SUPPORTS & PILARS	DWG.NO. 0-125.629.719
STEEL STRUCTURE RAILING	DWG.NO. 0-125.629.720
STEEL STRUCTURE GRATING	DWG.NO. 0-125.629.721
STEEL STRUCTURE FOOTPLATE	DWG.NO. 0-125.629.722
STEEL STRUCTURE SUPPORT FOR BARRING GEAR	DWG.NO. 2-125.629.882
STEEL STRUCTURE SUPPORT FOR OIL FILTER	DWG.NO. 2-125.629.883
STEEL STRUCTURE SUPPORT FOR COMP. DRAIN	DWG.NO. 2-125.629.884
STEEL STRUCTURE FLATBARS	DWG.NO. 0-125.629.885
STEEL STRUCTURE OIL PAN FOR FILTER	DWG.NO. 1-125.629.886
STEEL STRUCTURE OIL PAN FOR EXCHANGER	DWG.NO. 1-125.629.887
STEEL STRUCTURE OIL PAN FOR TANK	DWG.NO. 1-125.629.888
STEEL STRUCTURE DEVICE FOR SU-FILTER	DWG.NO. 2-125.629.889
STEEL STRUCTURE DEVICE FOR LIFTING	DWG.NO. 2-125.629.890
STEEL STRUCTURE DEVICE FOR SHIPPING	DWG.NO. 2-125.629.891
STEEL STRUCTURE EQUIP. ALIGNEMENT	DWG.NO. 0-125.629.892
STEEL STRUCTURE LADDER	DWG.NO. 0-125.630.011
STEEL STRUCTURE GATE LEFT	DWG.NO. 0-125.630.012

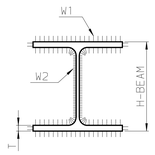

PROFILE	T	W1	W2
H-582x300	17	7.1	5.7
H-440x300	18	7.1	5.7
H-300x300	15	7.1	5.7
H-200x200	12	7.1	5.7
H-150x150	10	5.7	4.2
H-100x100	8	4.2	4.2

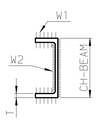

PROFILE	T	W1	W2
CH-200x90	13.5	7.1	5.7
CH-150x75	10	5.0	3.0
CH-100x50	7.5	4.0	3.0

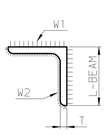

PROFILE	T	W1	W2
L-75x75	9	5.0	5.0
L-50x50	6	3.0	3.0

W1: THINNER THICKNESS BETWEEN PLATE AND FLANGE OF BEAM MINUS 2mm, BUT NOT LESS THAN INDICATED BELOW

W2: THINNER THICKNESS BETWEEN PLATE AND WEB OF BEAM MINUS 2mm, BUT NOT LESS THAN INDICATED BELOW

THICKNESS OF THICKER PART JOINED	MIN. W1/W2
THX ≤20mm	6.0
THX >20mm	8.0

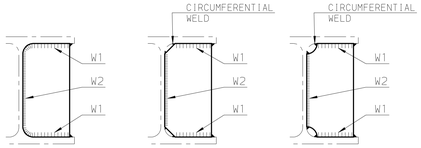

Name	Date	Name	Date	Name	Date	Name	Date
Sep.parts list		Design group					
Replaced by		Subst. for		Orig. scale 1:15			

HANWHA OCEAN 3LP165E-3C26	STEEL STRUCTURE OVERVIEW	Drawn: 23-02-2025 TONELLI_M
L-0234 ASME	BOG-BOOSTER - COMPRESSOR ITEM NO.: C-001	Verified: 01-04-2025 FUNK_A
		Standards conform:
CAD-Drawing	Part-No.	Bar - Code
Burckhardt Compression	E	0-125.629.716 1 - 1

This drawing is entrusted to the recipient personally, but the copyright remains with us. It must not be copied, reproduced or in any way communicated or made accessible to third parties without our written consent.

Similar Dwg.

Machining regulations see Drawing Standards.