



ALL NON MARKED H-BEAMS H100x100
1) FULL PENETRATION WELDED


SECTION C-C

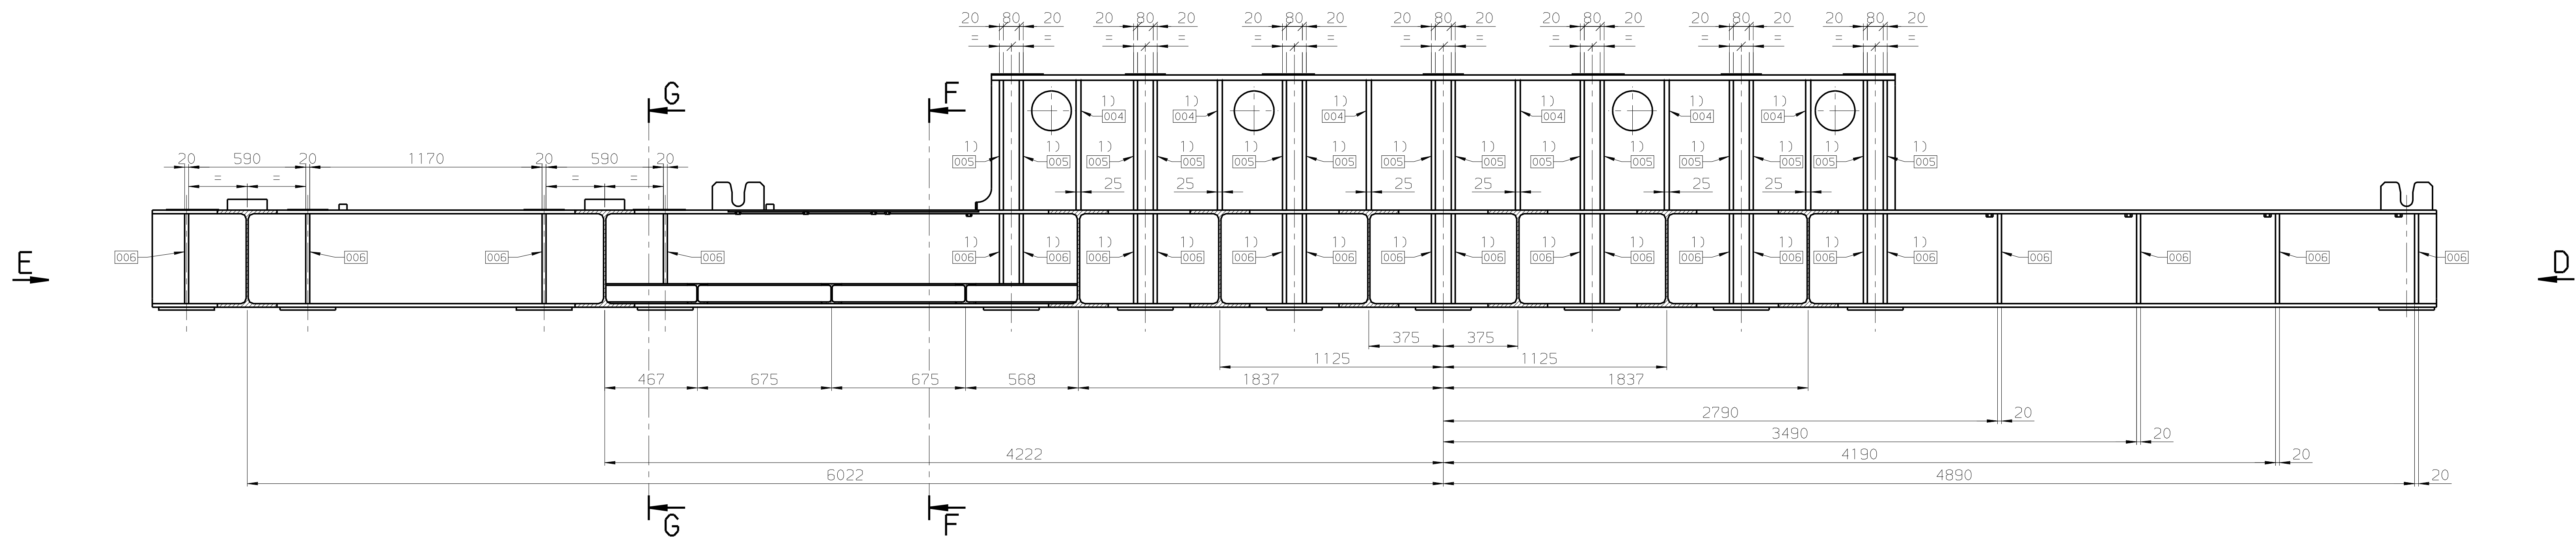


VIEW D

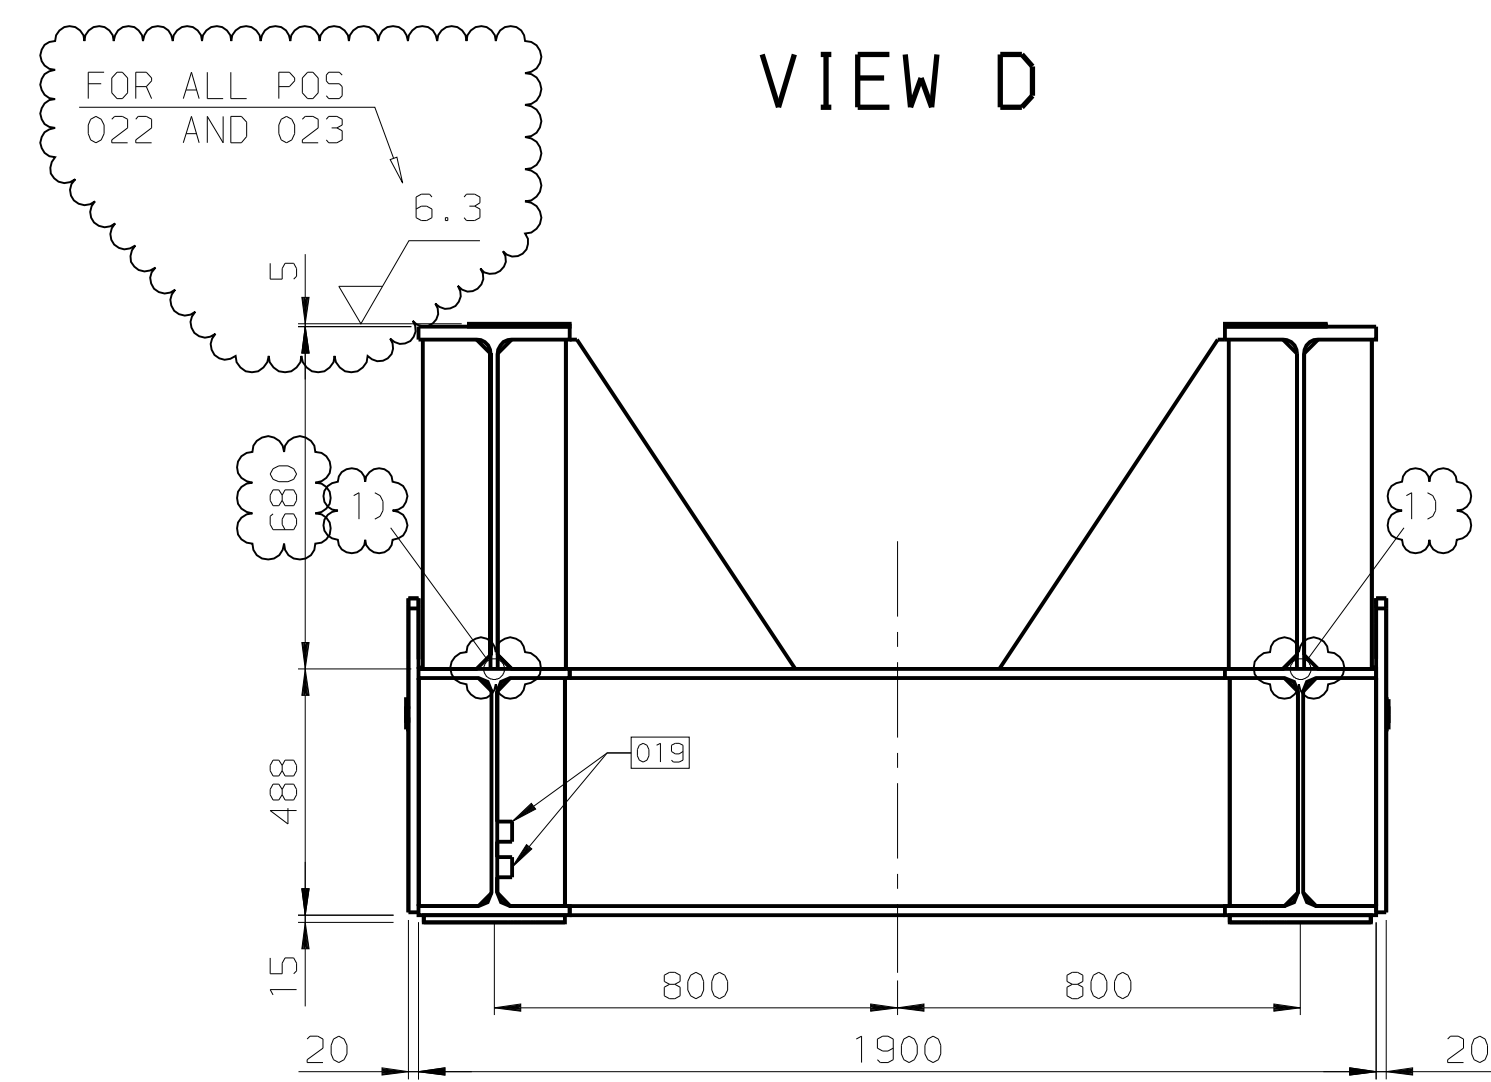


VIEW E

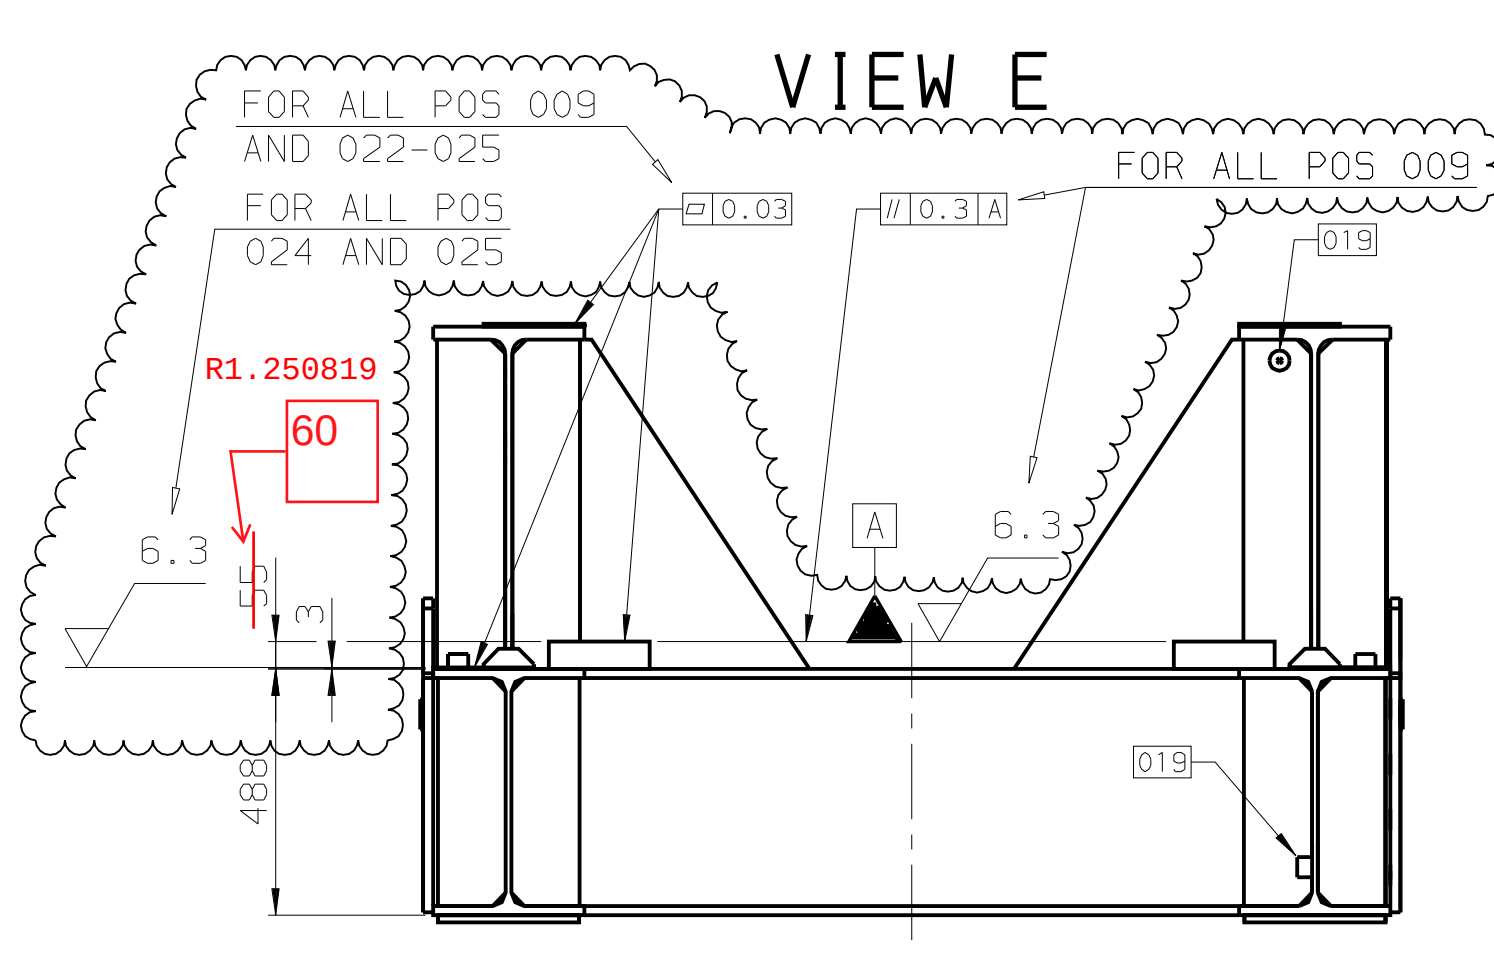

SECTION F-F

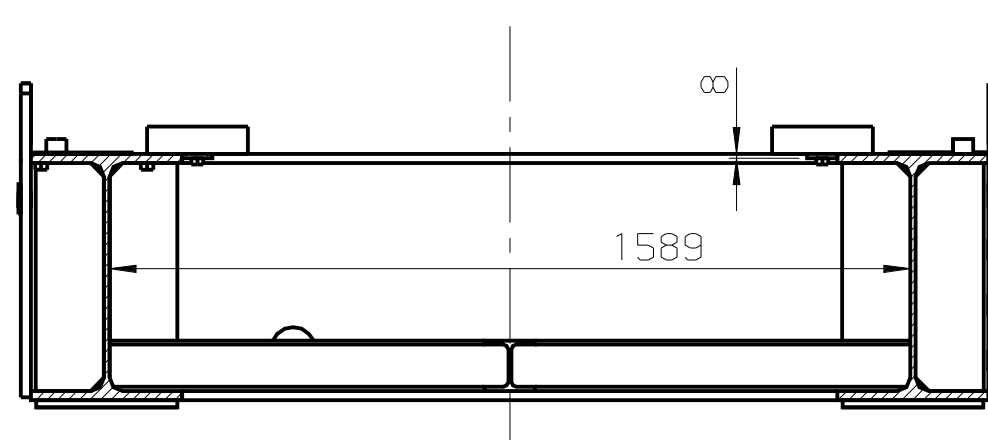


SECTION G-G

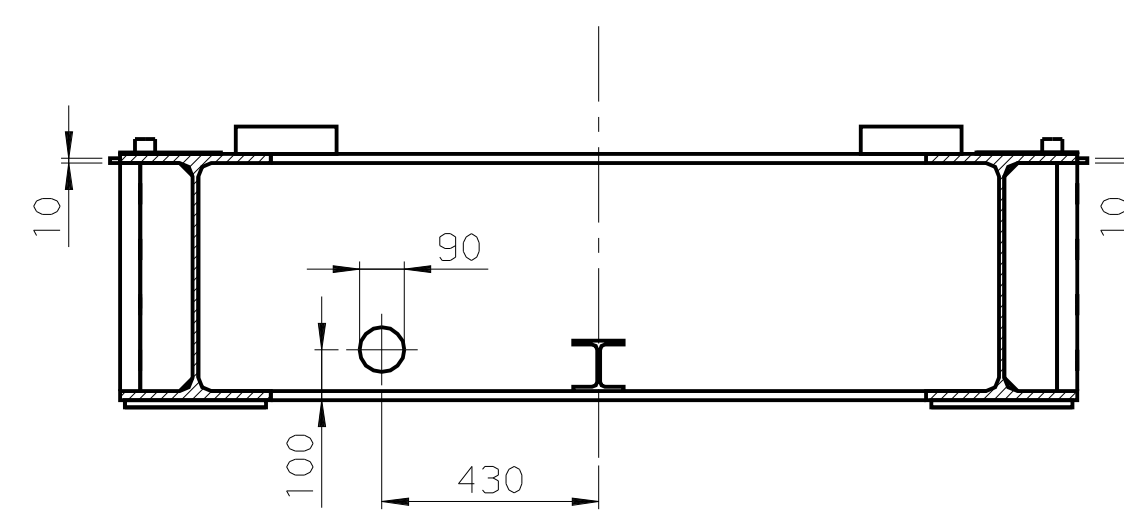


POS 004

THICKNESS 25mm
(SCALE 1:10)

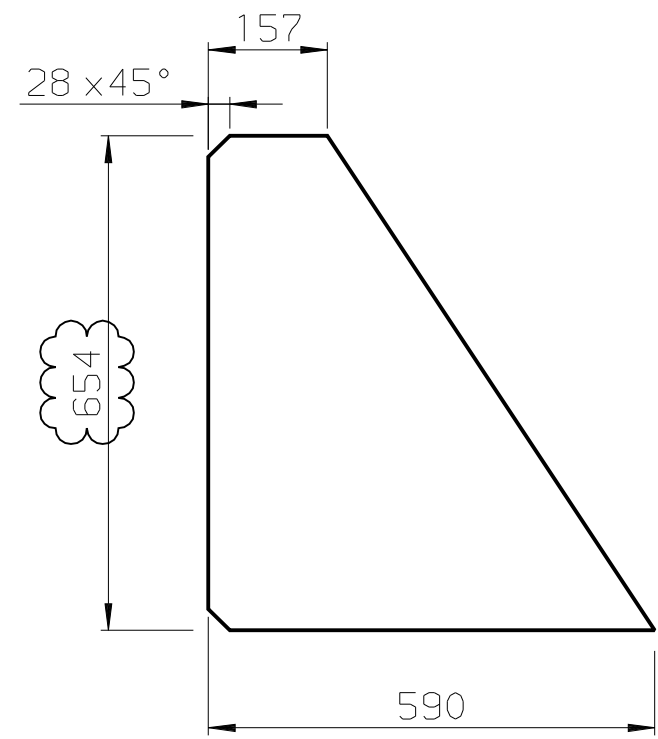


POS 005

THICKNESS 20mm
(SCALE 1:10)

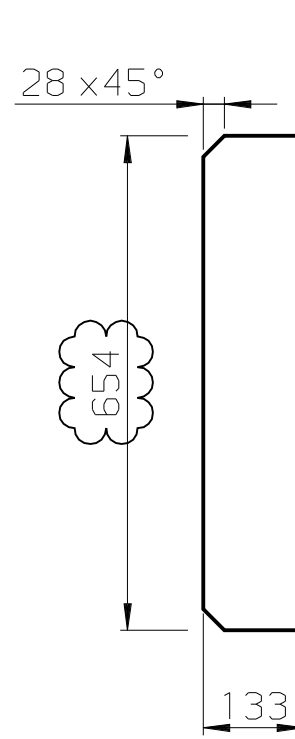


POS 006

THICKNESS 20mm
(SCALE 1:10)

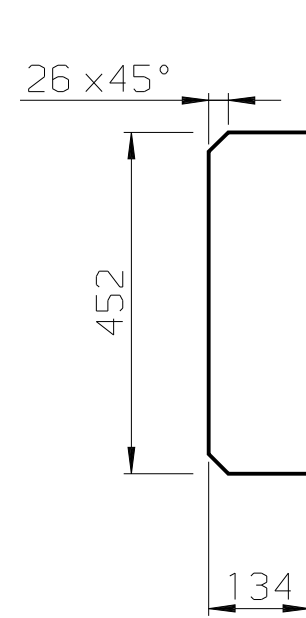


POS 010

THICKNESS 40mm
(SCALE 1:10)

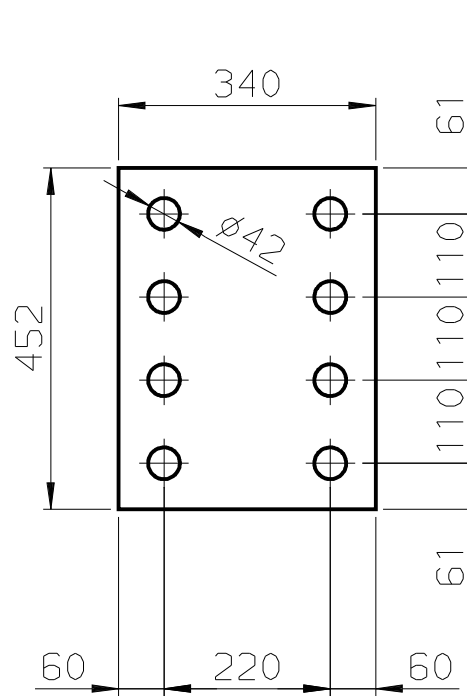


POS 011

(SCALE 1:10)

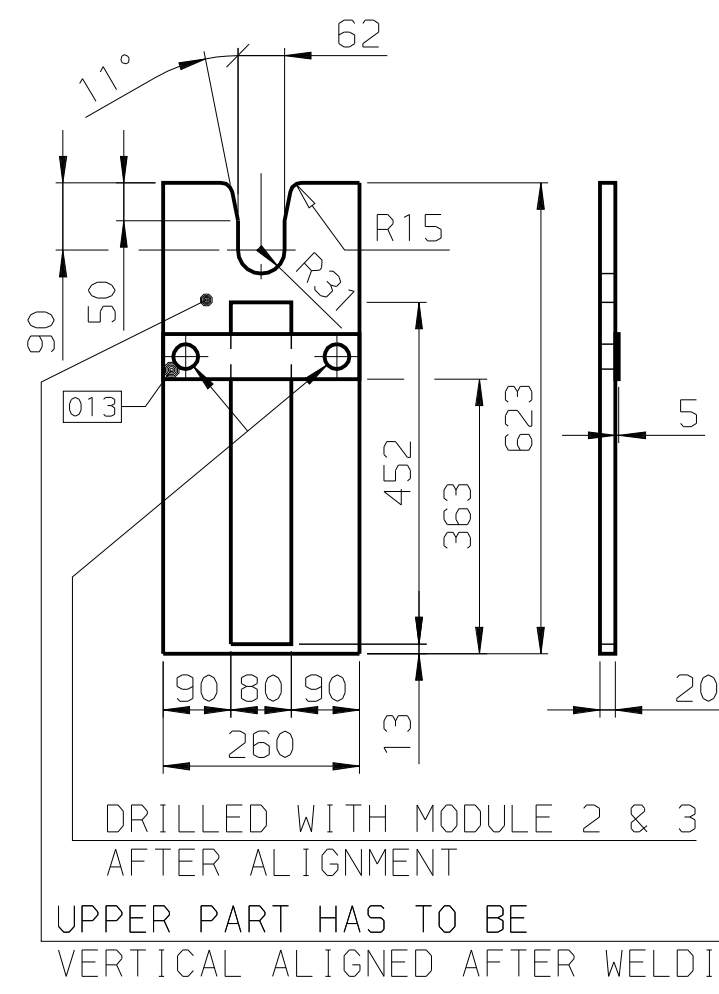


POS 012

(SCALE 1:10)

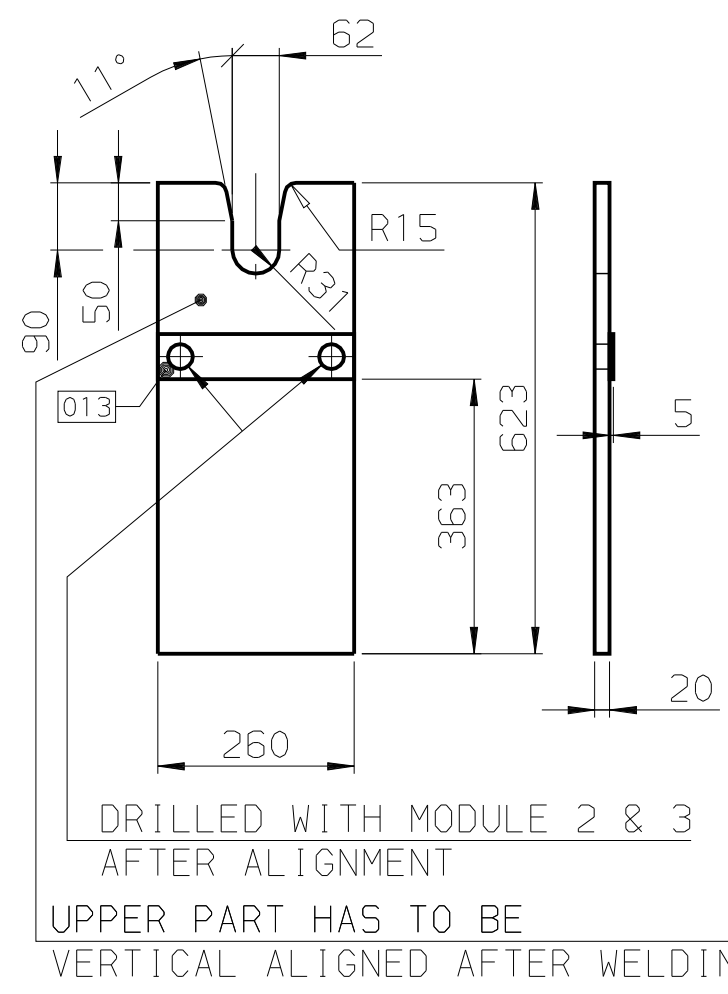


POS 007

THICKNESS 20mm
(SCALE 1:10)

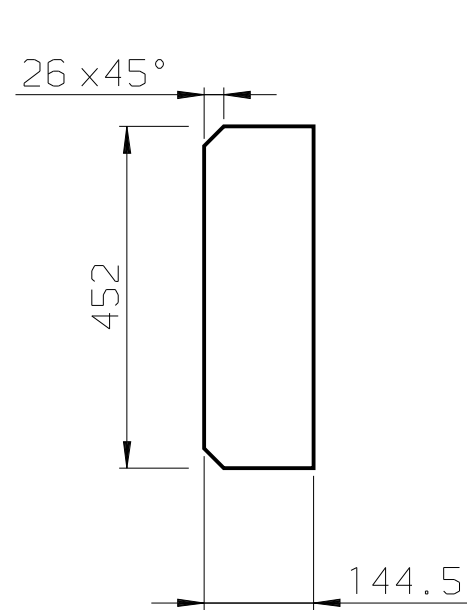


POS 008

THICKNESS 20mm
(SCALE 1:10)

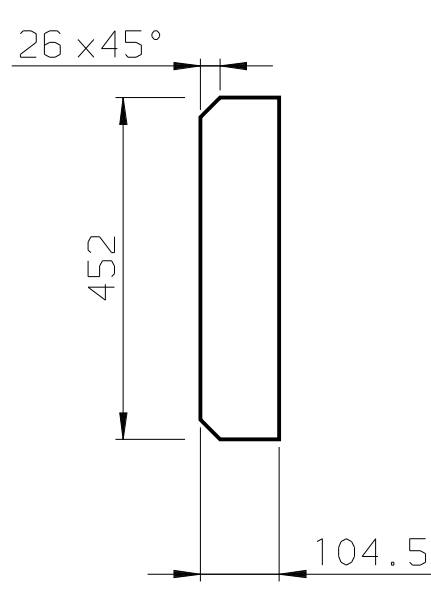


POS 017

THICKNESS 8mm
(SCALE 1:5)

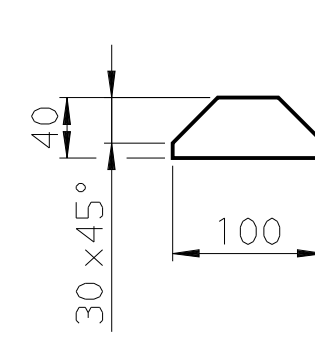


POS 019

EARTHING CONNECTION
(SCALE 1:2)

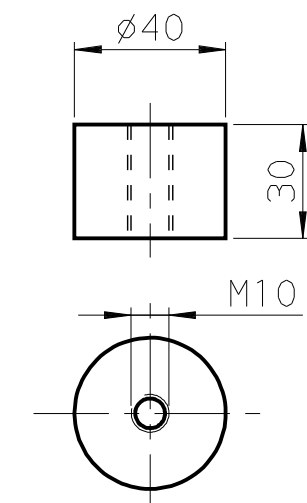

POS 011

(SCALE 1:10)

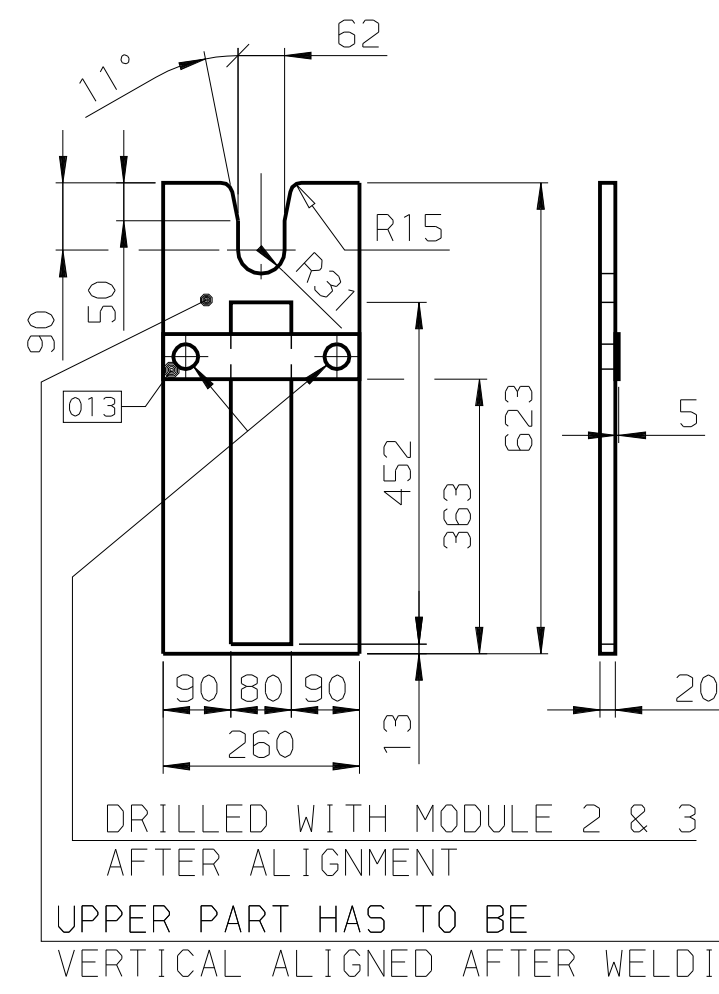

POS 012

(SCALE 1:10)


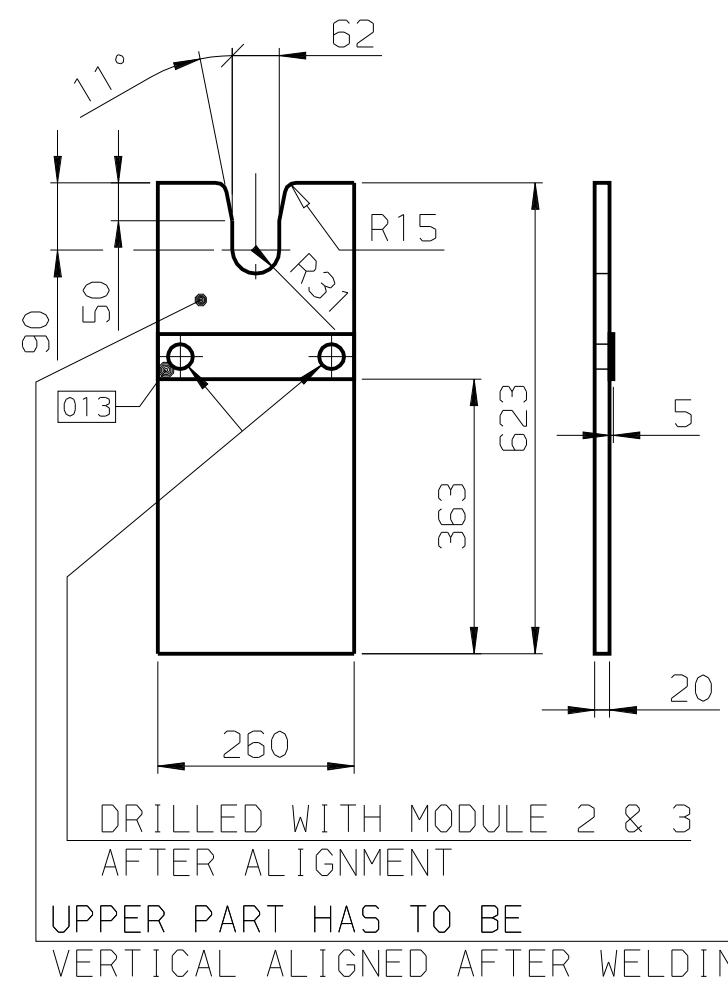


PLATE HAS BE TACK WELDED
AFTER ALIGNIG
THICKNESS 5mm

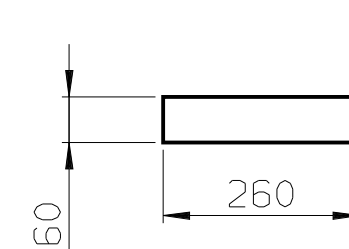

Rev. / Pos. / Date	Rev. / Pos. / Date	Rev. / Pos. / Date	Rev. / Pos. / Date	Rev. / Pos. / Date	Rev. / Pos. / Date	Rev. / Pos. / Date	Rev. / Pos. / Date
1 / 1 / 19-04-2022	2 / 1 / 22-02-2023	3 / 1 / 22-02-2023	4 / 1 / 22-02-2023	5 / 1 / 22-02-2023	6 / 1 / 22-02-2023	7 / 1 / 22-02-2023	8 / 1 / 22-02-2023
TONELLI, M.	TONELLI, M.	TONELLI, M.	TONELLI, M.	TONELLI, M.	TONELLI, M.	TONELLI, M.	TONELLI, M.
Name	Name	Name	Name	Name	Name	Name	Name
Date	Date	Date	Date	Date	Date	Date	Date
Replaced by	Subst. For	Orig. scale	1:15				
SLP250V-SA	STEEL STRUCTURE M1 BASE FRAME	Drawn:	19-04-2022	TONELLI, M.			
L-0184 ASME	LABY-GI - NON-LUBE COMP. ITEM NO.: C-001	Verified:	22-02-2023	SABOGAL, A			
		Standards	conform:				
CAD-Drawing	Part-No.	Bar - Code					
Burckhardt Compression	E	0-125.619.945	3-3 c				