


MAIN FRAME (9/16)

PLAN VIEW "F" (FRAME ONLY)

*DET. 'z-1', 'z-2' : SEE PAGE MAIN FRAME 7

* 특기 외 ⑮ 자재 사용할 것 (H.350x350x12x19)
* BASE FRAME하부 마스킹 (유첨참조)

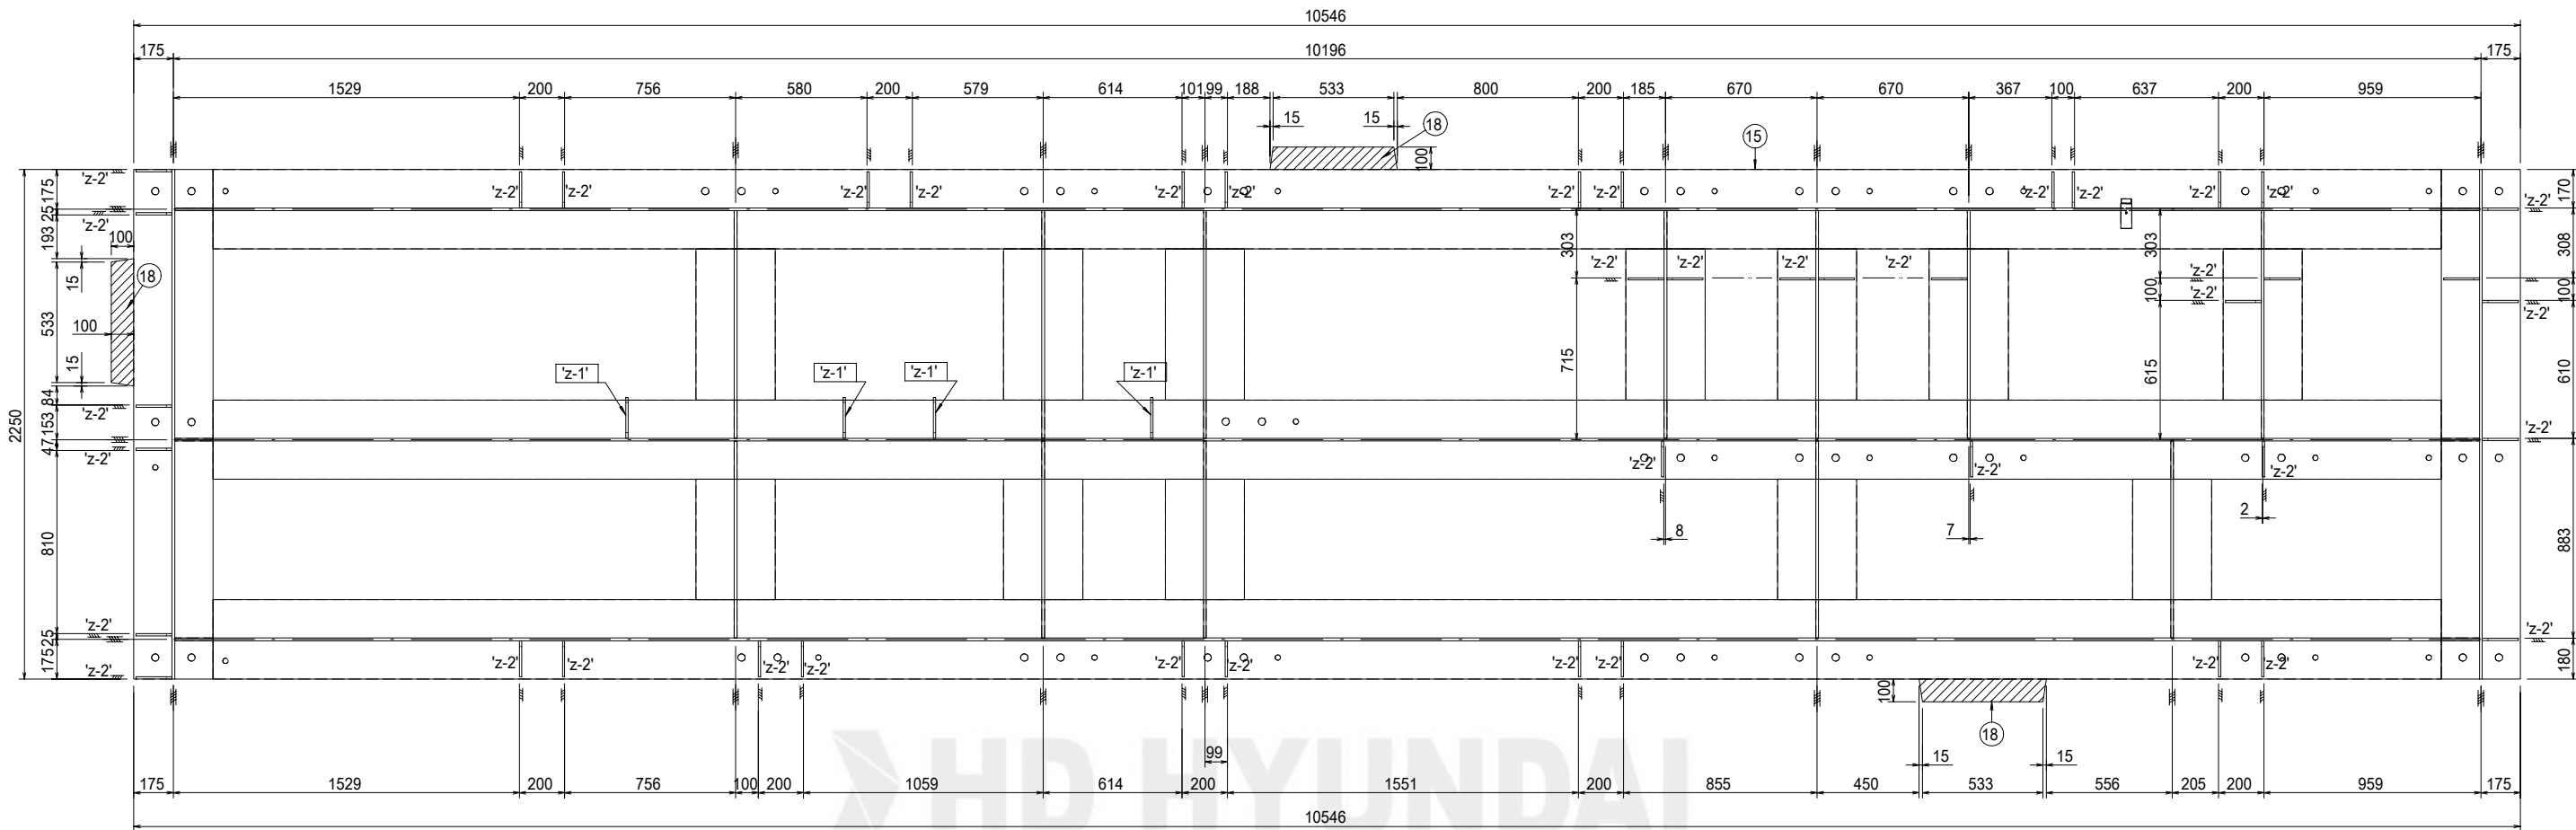

PLAN VIEW "F" (HOLE & COAMING)

*VIEW "F-1", "F-2" : SEE PAGE MAIN FRAME 8

