



Execution Code Number		Fig.No.	Designation	Source of Supply	Rev.
		Date	Material and Remarks	Approx.	Letter
Number					
4.54		001	GRATING (THK 25)	/	/
APPROX WEIGHT				m	Kg


NOTE:
1) ALL LISTE MATERIAL ARE WITHOUT ALLOWANCE.

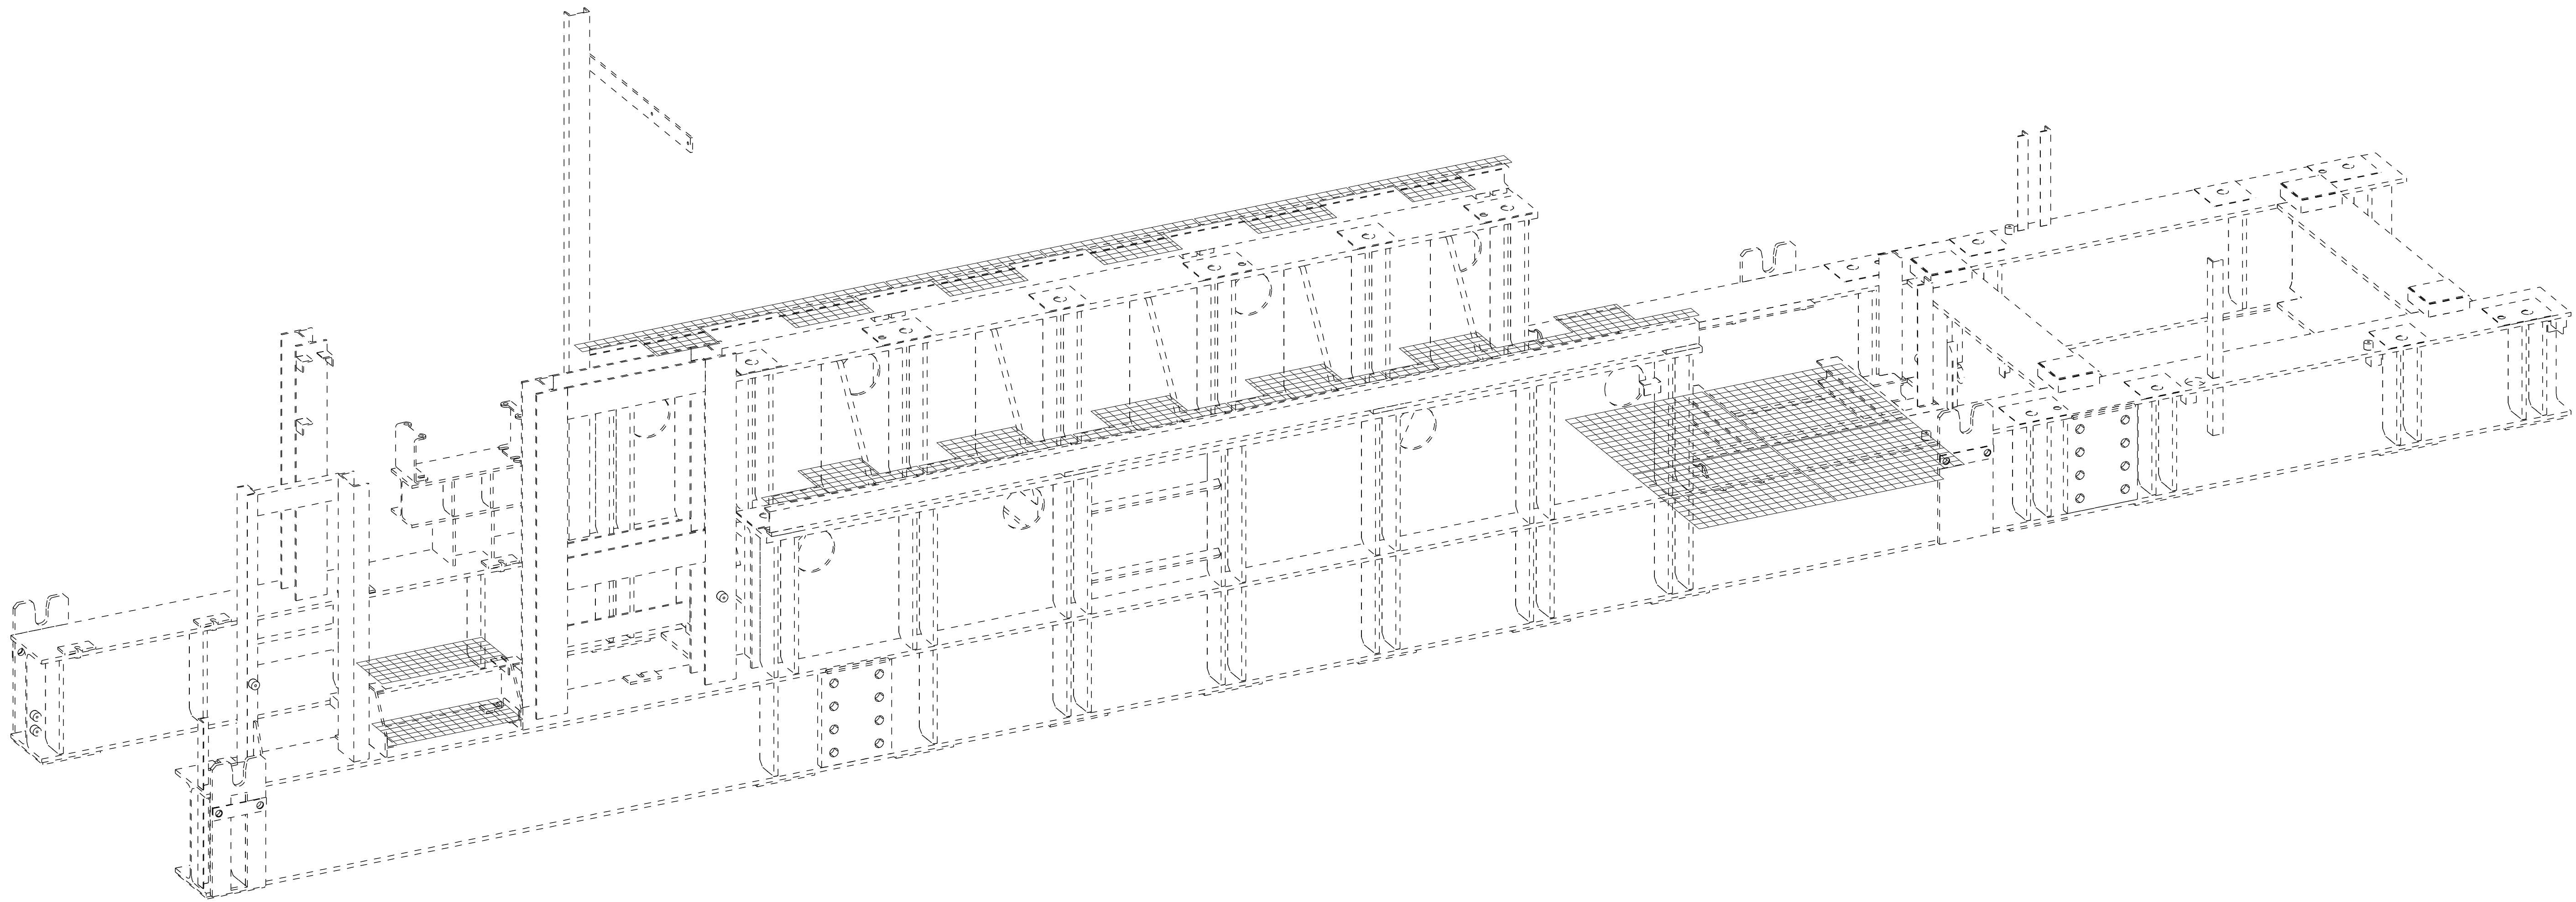


참고도면

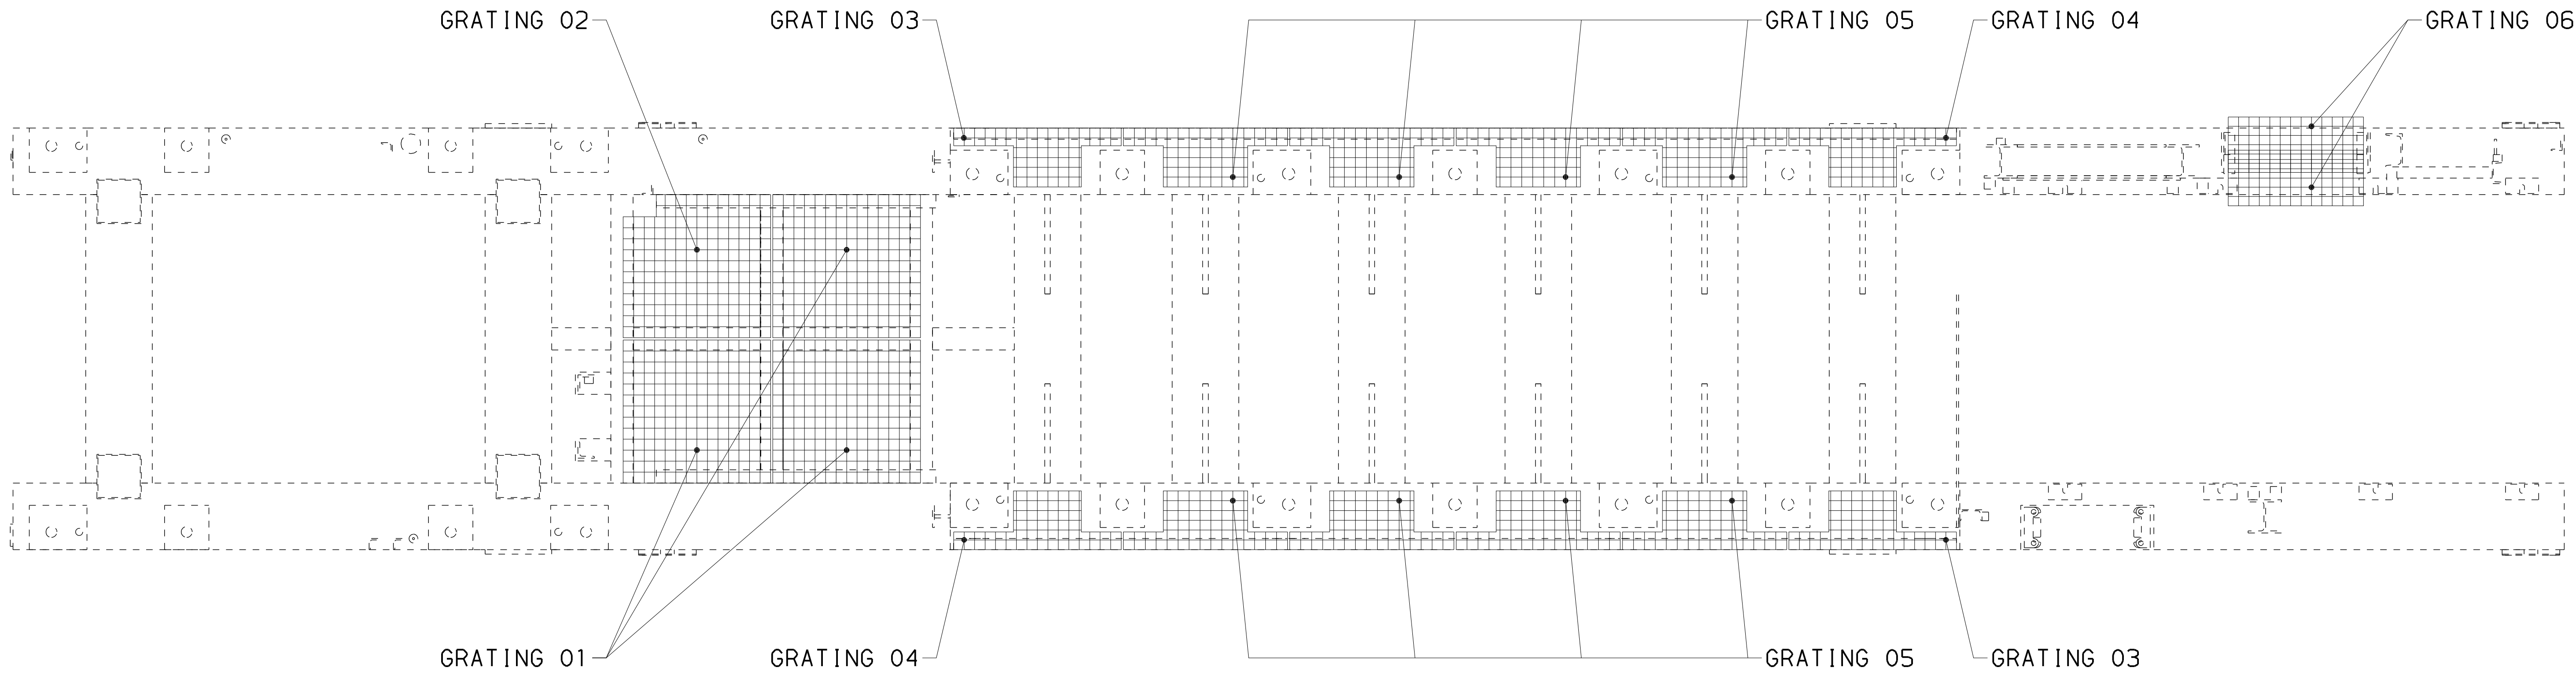


001
GRATING 01 (QTY 3)
THICKNESS 25mm
(SCALE 1:20)

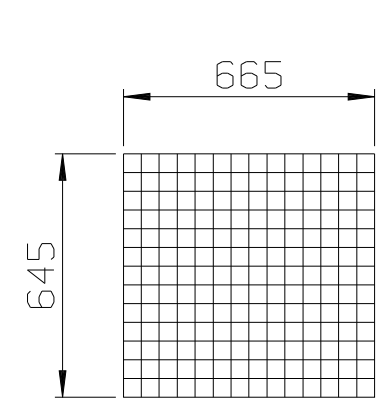


001
GRATING 02
THICKNESS 25mm
(SCALE 1:20)

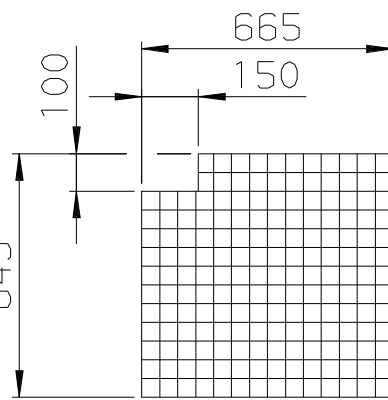


001
GRATING 03 (QTY 2)
THICKNESS 25mm
(SCALE 1:20)

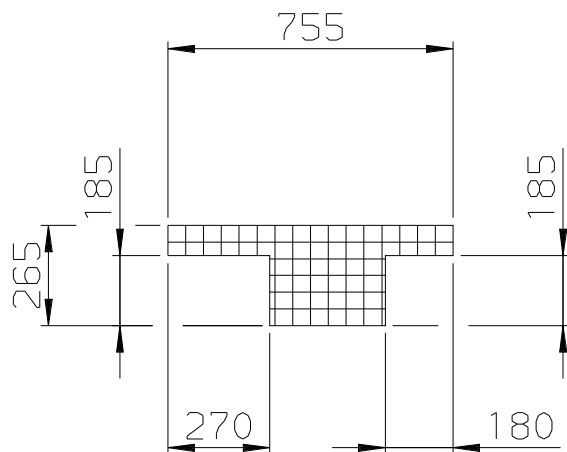


001
GRATING 04 (QTY 2)
THICKNESS 25mm
(SCALE 1:20)

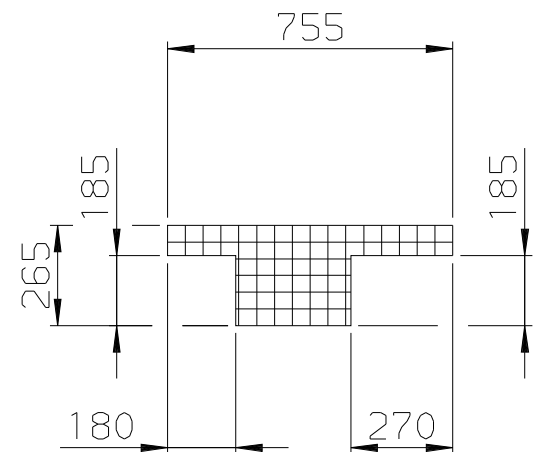

001
GRATING 05 (QTY 8)
THICKNESS 25mm
(SCALE 1:20)

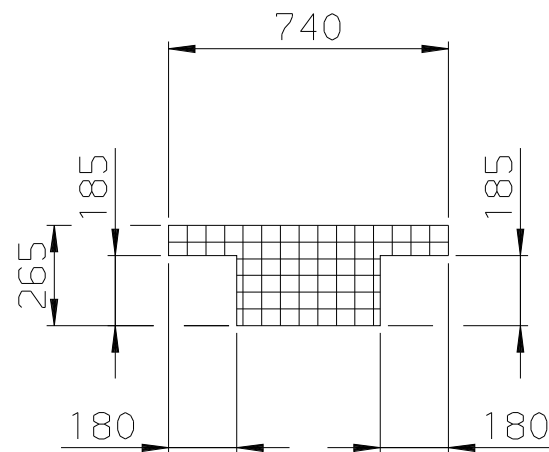

001
GRATING 06 (QTY 2)
THICKNESS 25mm
(SCALE 1:20)

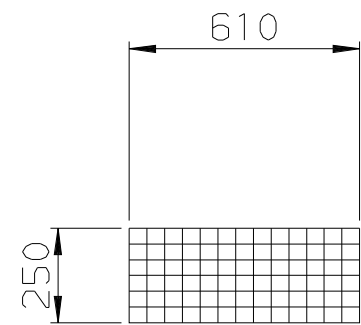

Rev. No.	0	1	2	3	4	5	6	7	8
Rev. Description	TONELLI_M								
Name	Date	Name	Date	Name	Date	Name	Date	Name	Date
Replaced by	Design group	Subst. For	Orig. scale	1:15					
SLP250V-SA		STEEL STRUCTURE	14-04-2022	Drawn:	TONELLI_M				
L-0184		M1 GRATING		Verified:	10-03-2023	SABOGAL_A			
ASME		LABY-G1 - NON-LUBE COMP.		Standards	conform:				
ITEM NO.: C-001									
CAD-Drawing	Part-No.	Bar - Code							
Burckhardt Compression	E	0-125.619.947							