


SUPPORT 취부도 (4 / 14)

해당표기 SUPP는
정위치 T/W할 것.

PLAN VIEW "B"

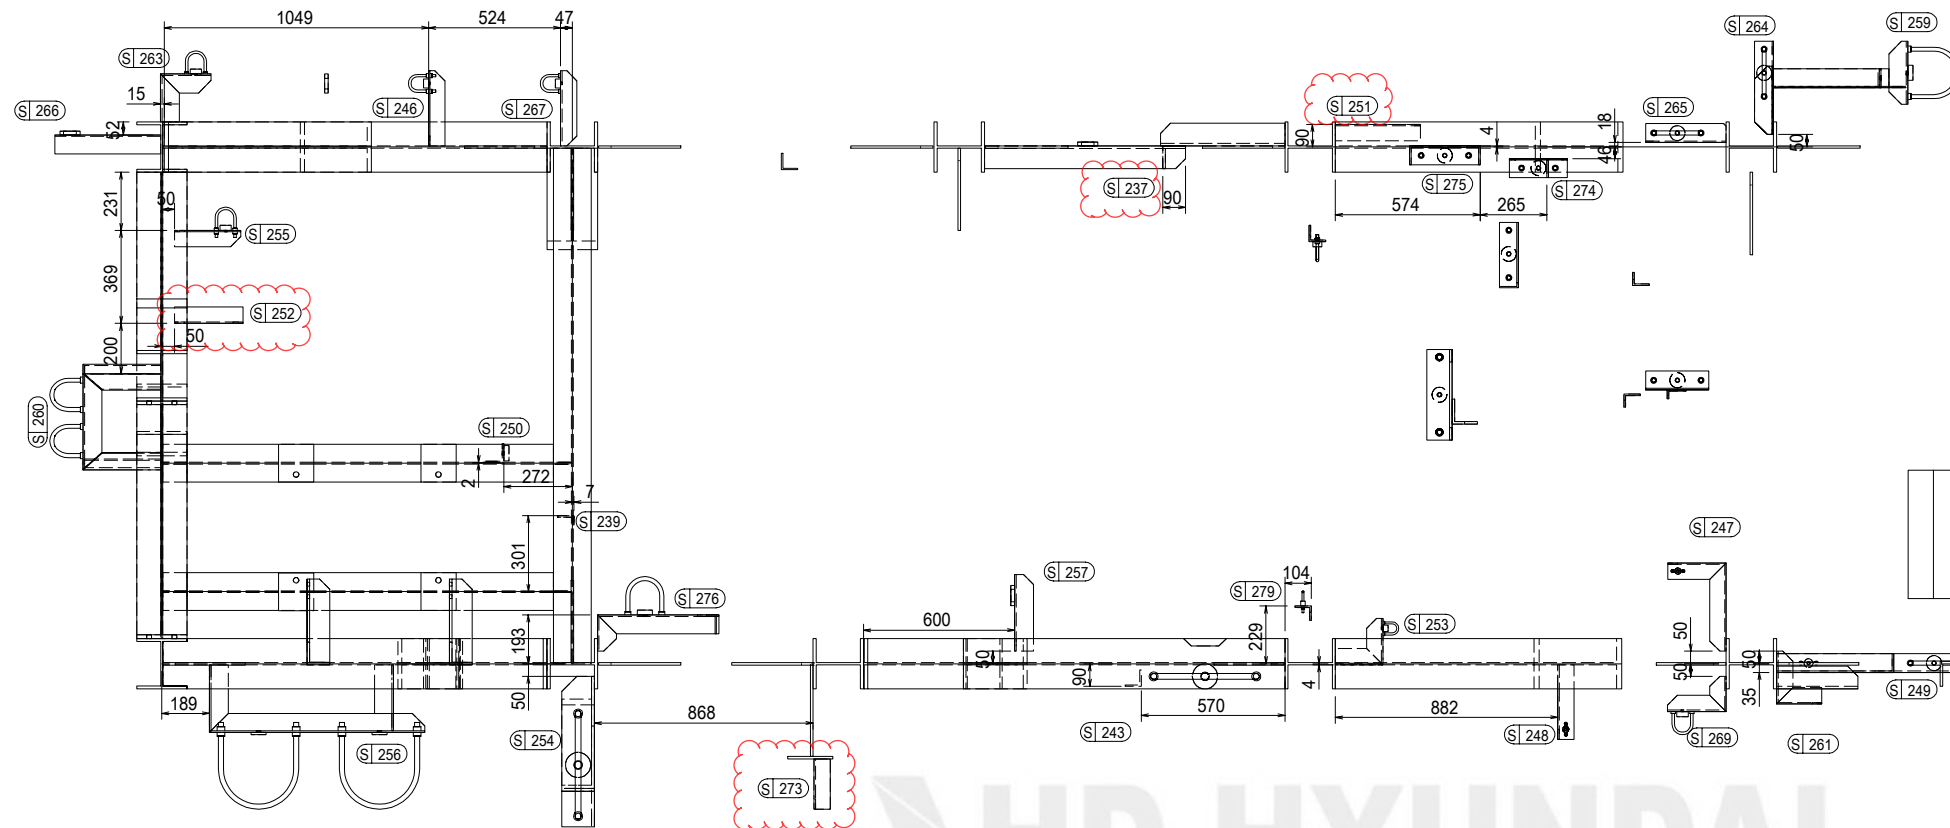

PLAN VIEW "C"

