



ALL NON MARKED H-BEAMS 100x100 002
ALL NON MARKED U-BEAMS 100x50 004
ALL NON MARKED L-BEAMS 50x50x6 008


SECTION G-G

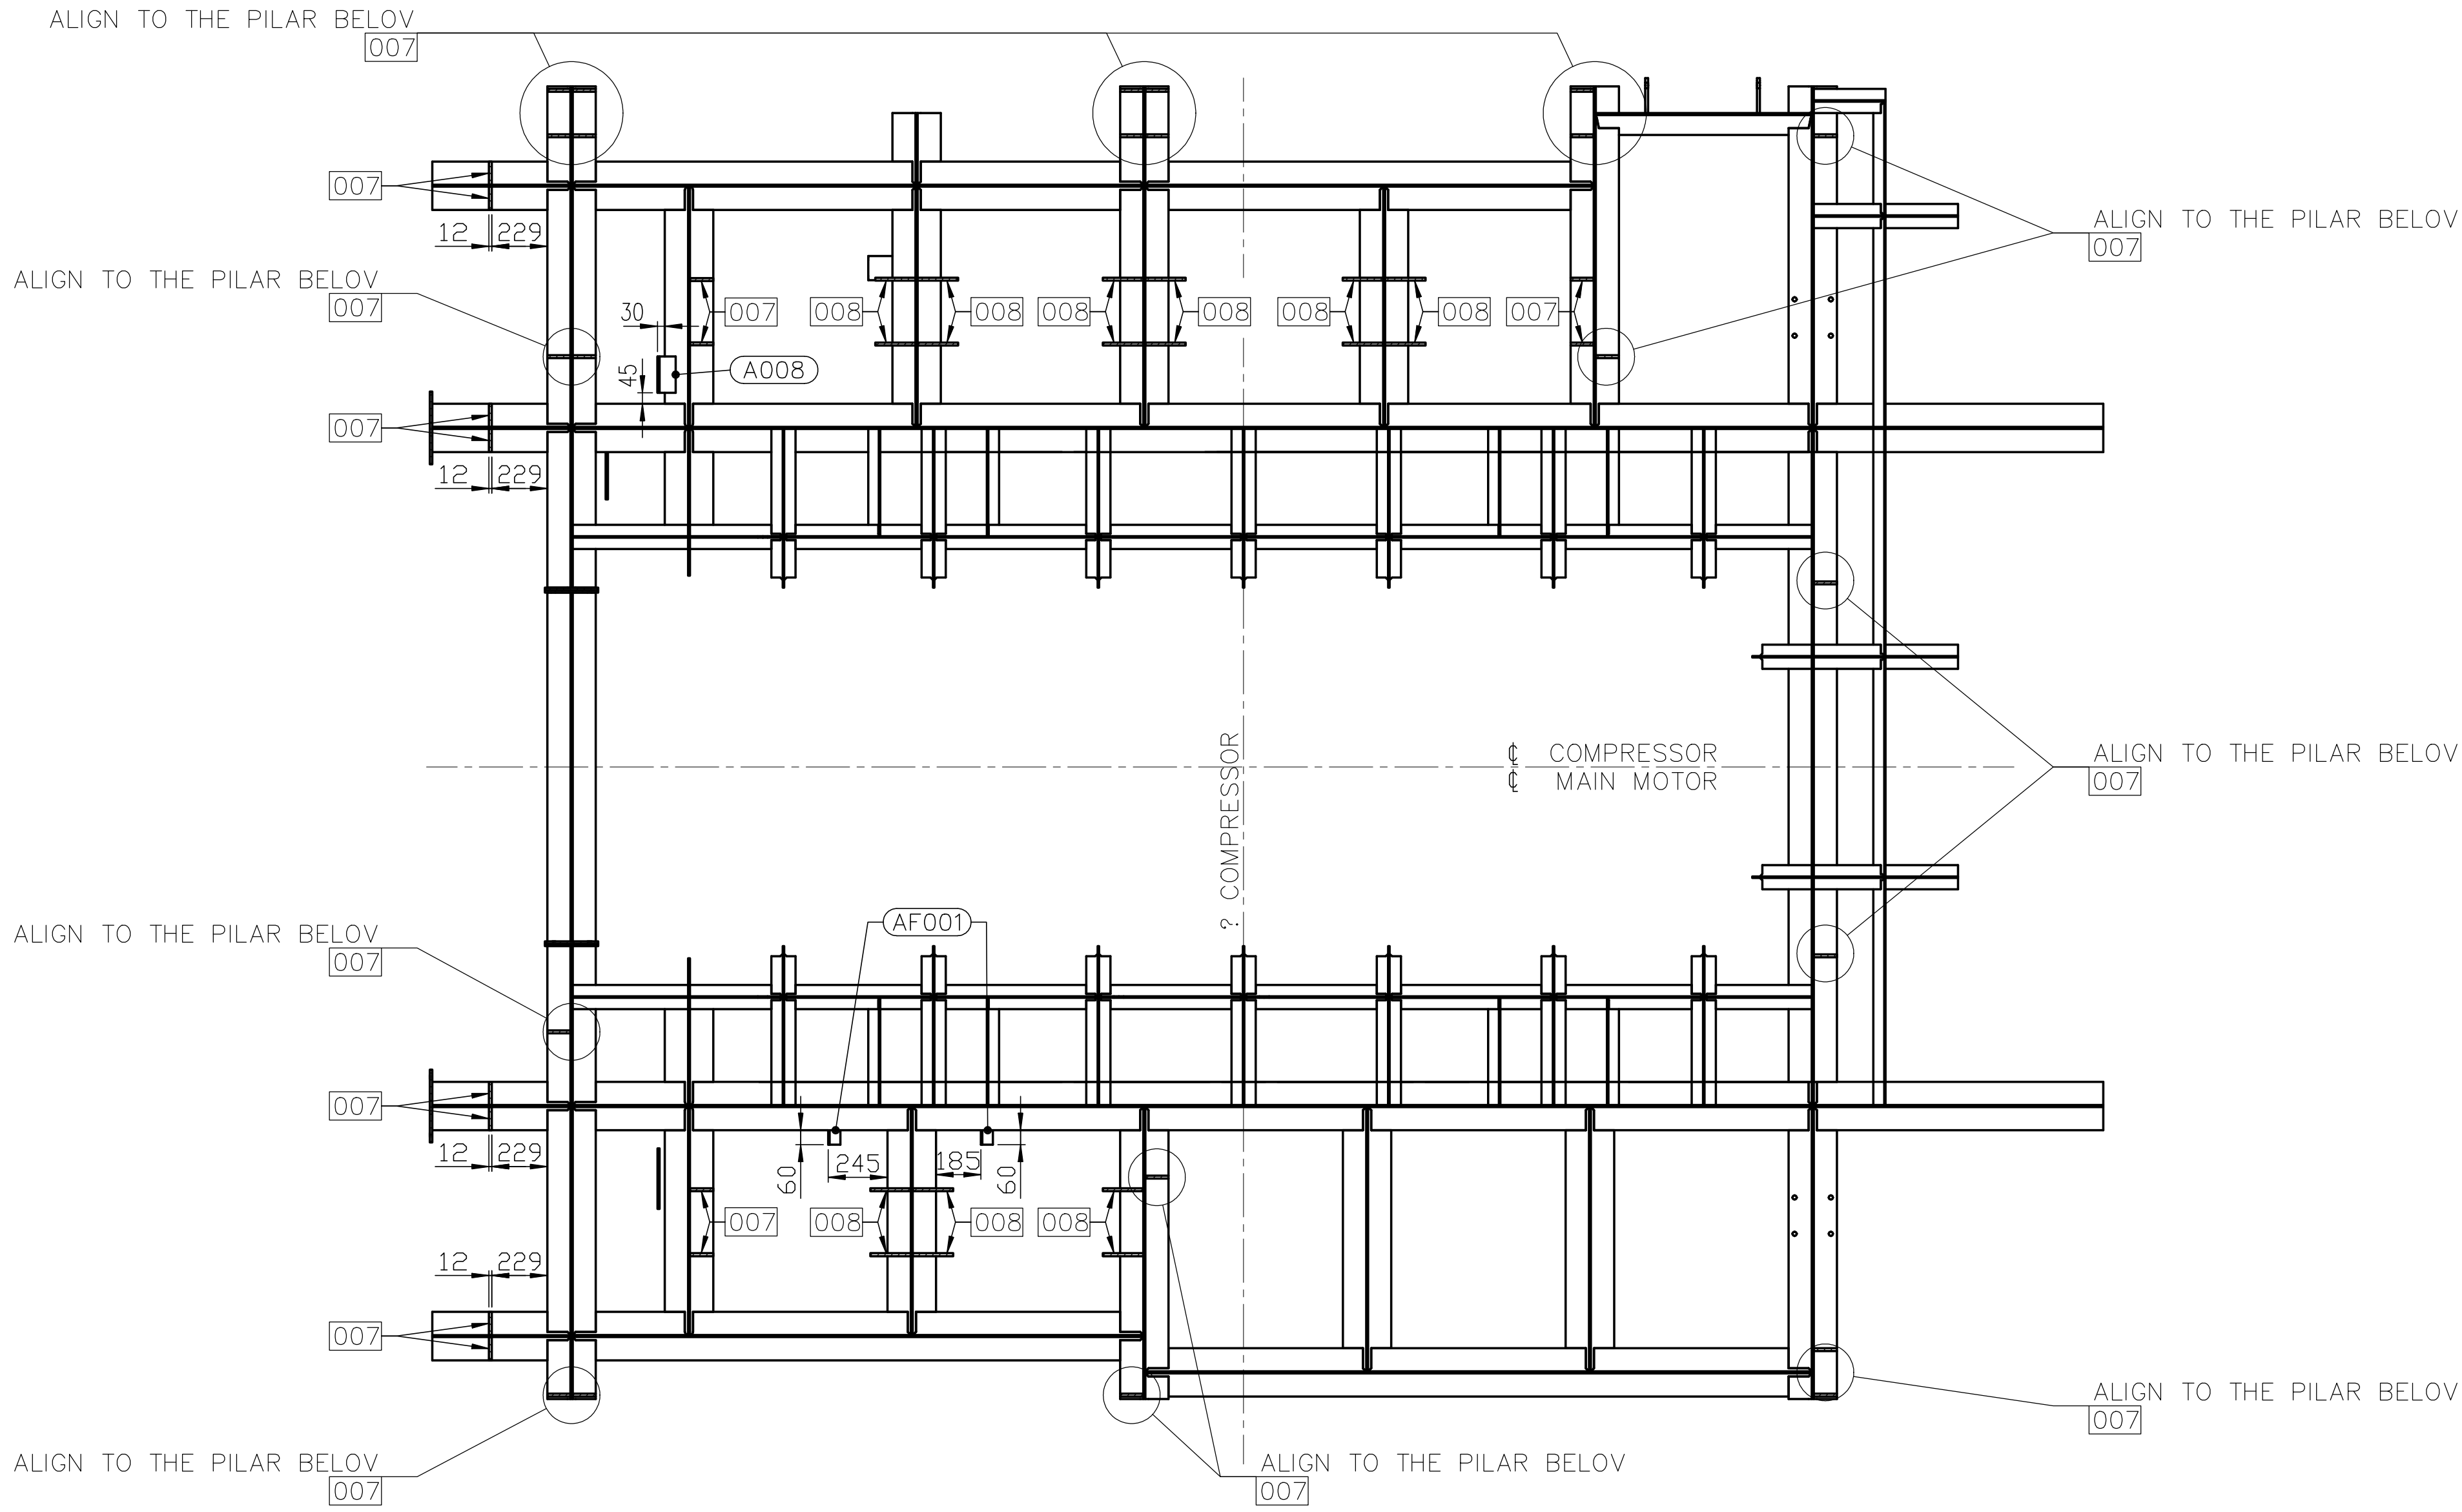


SECTION H-H

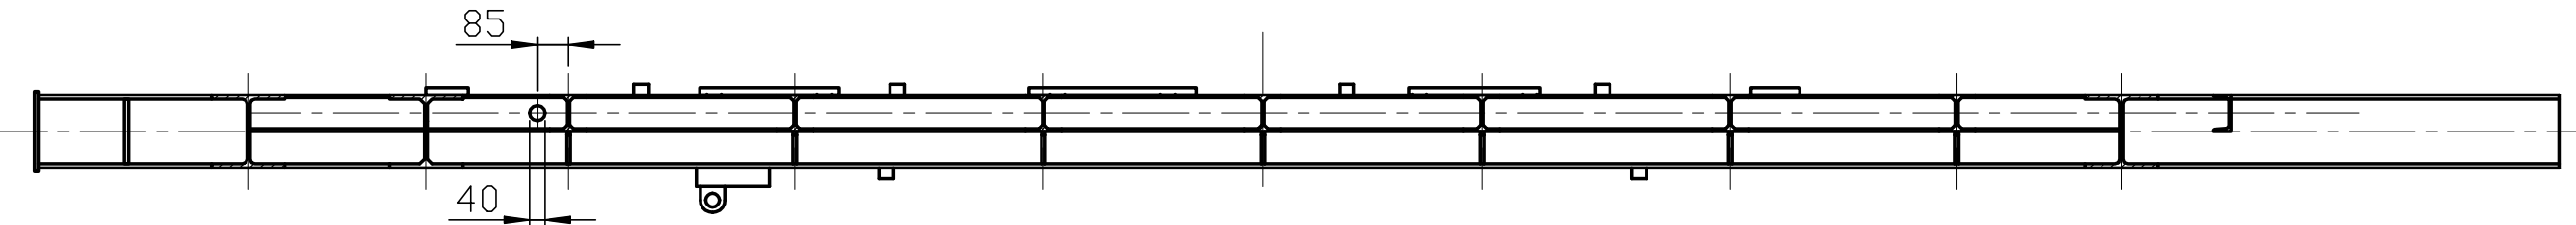


SECTION I-I

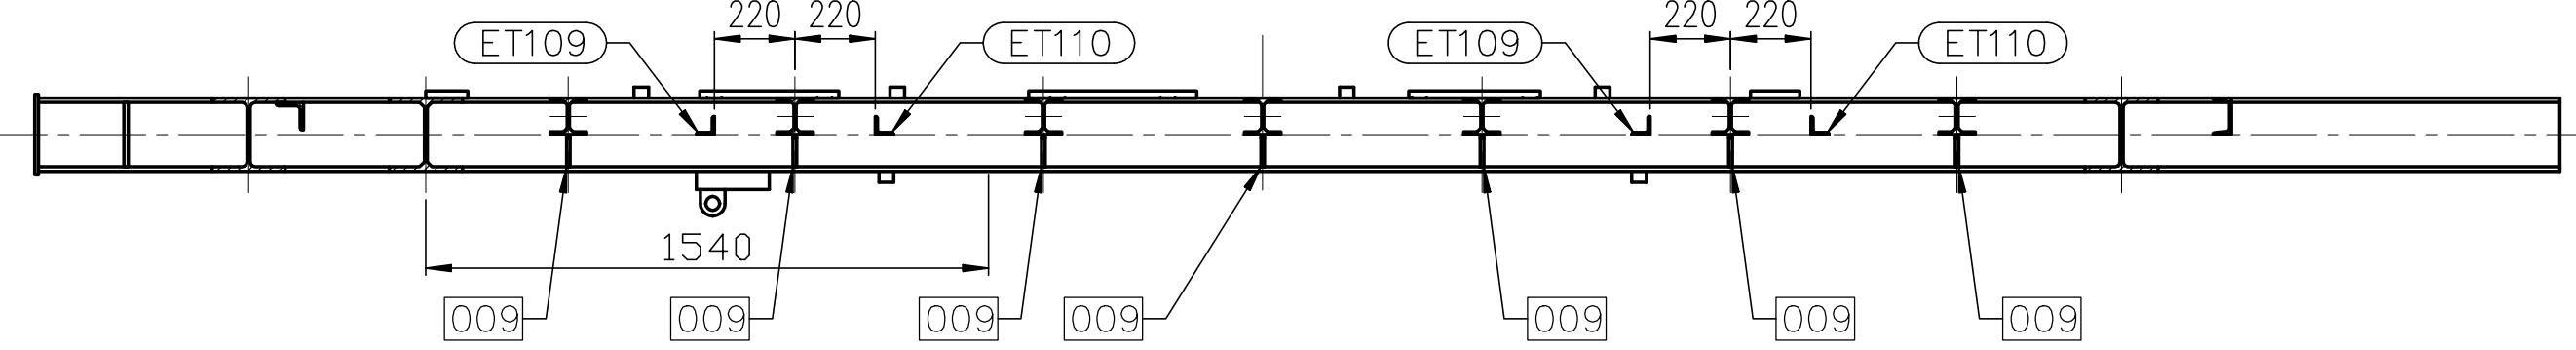


SECTION J-J

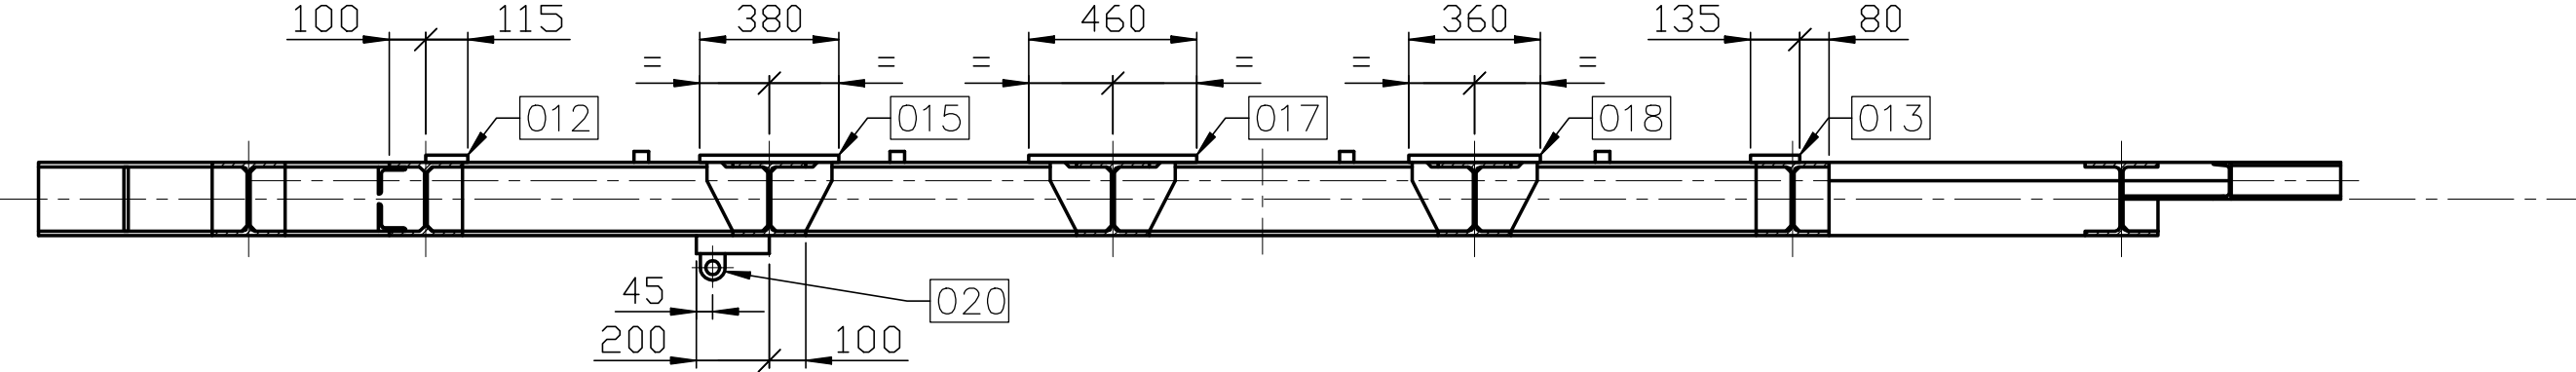


SECTION K-K

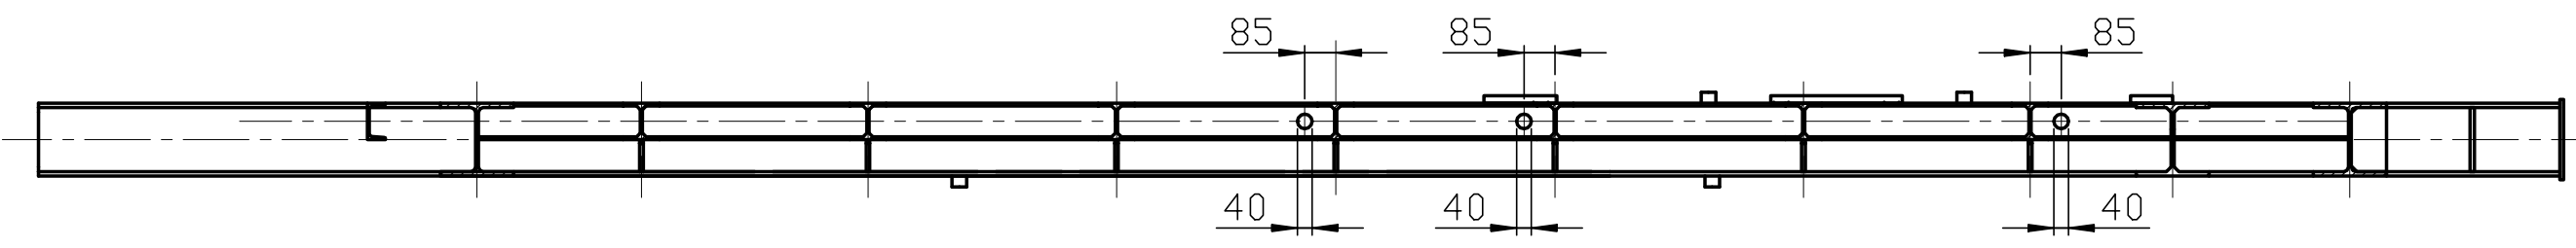

SECTION L-L

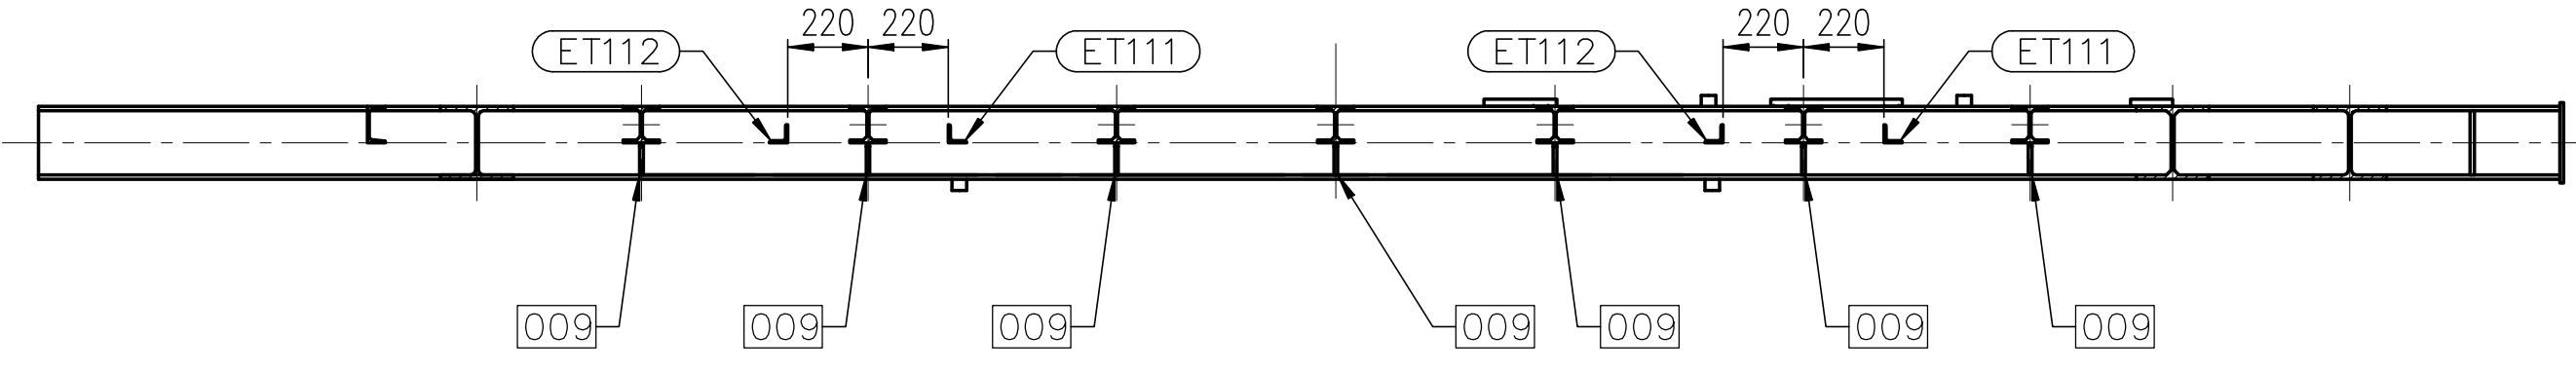


SECTION M-M

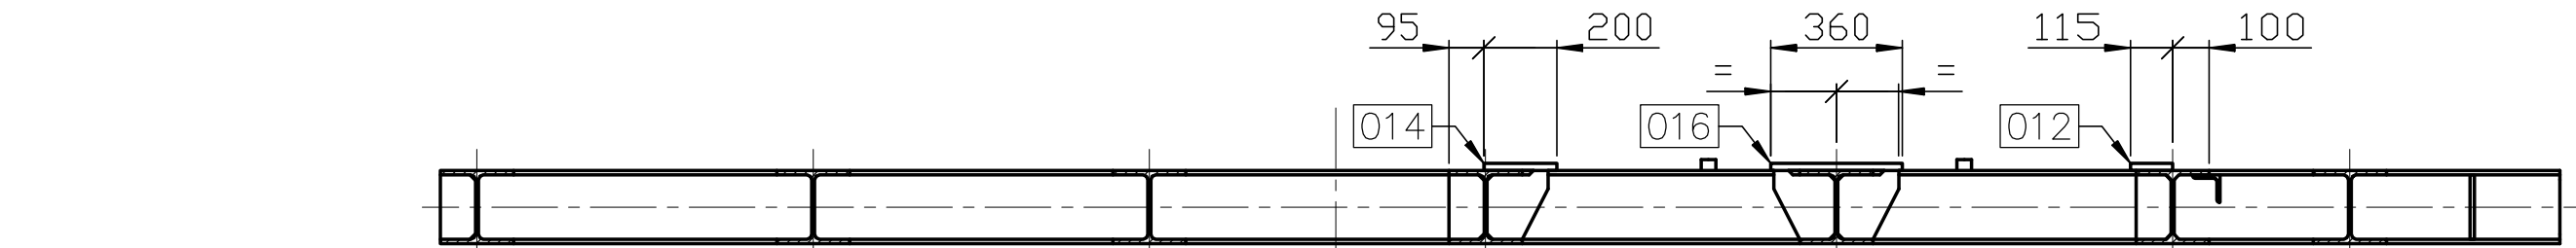


POS 007

THICKNESS 12mm
(SCALE 1:5)

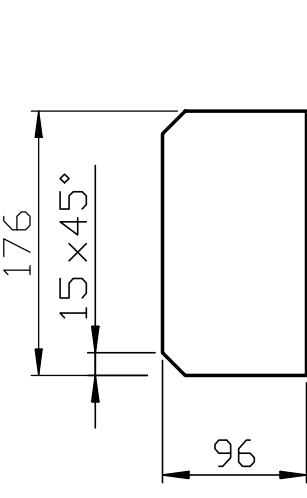


POS 008

THICKNESS 12mm
(SCALE 1:5)

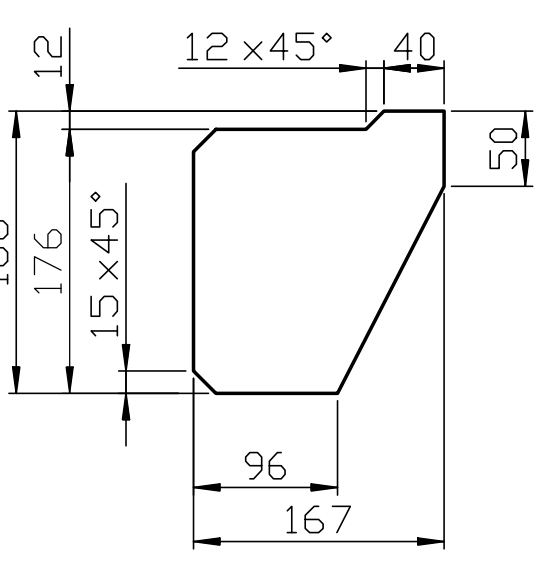


POS 009

THICKNESS 10mm
(SCALE 1:5)

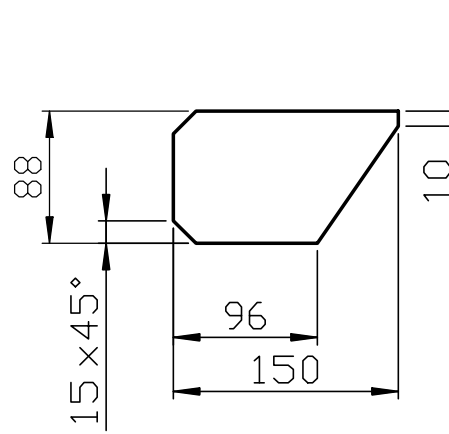


POS 010

THICKNESS 10mm
(SCALE 1:5)

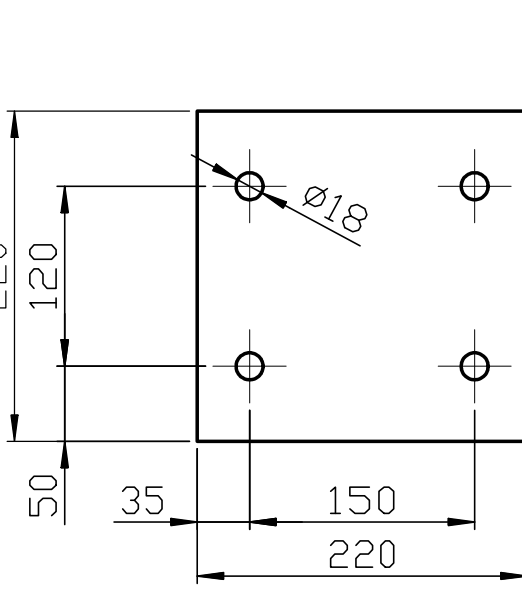


POS 011

THICKNESS 10mm
(SCALE 1:5)

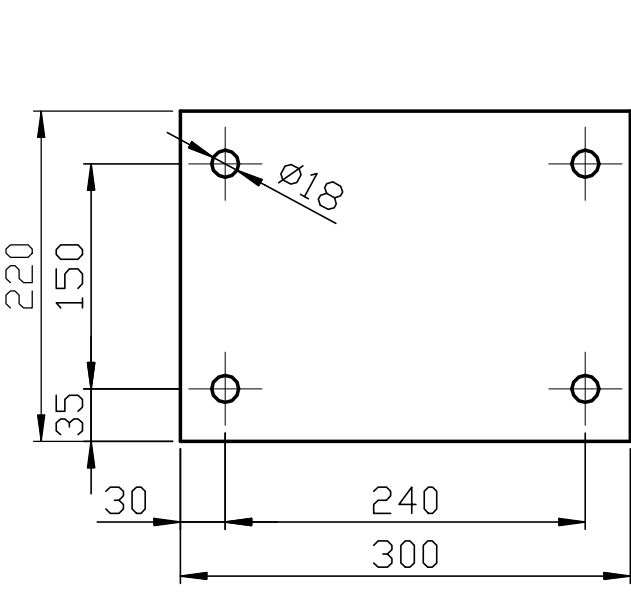


POS 012

THICKNESS 20mm
(SCALE 1:10)

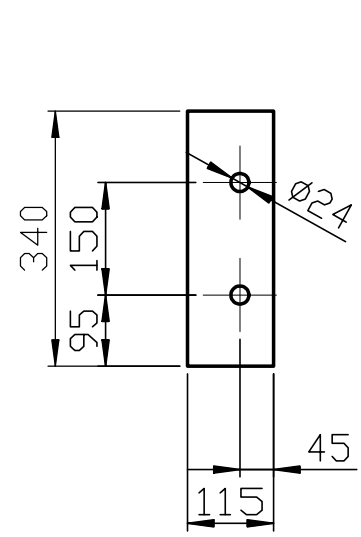


POS 013

THICKNESS 20mm
(SCALE 1:10)

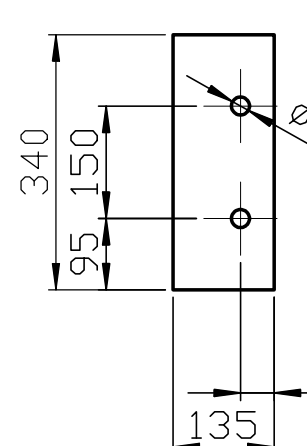


POS 014

THICKNESS 20mm
(SCALE 1:10)

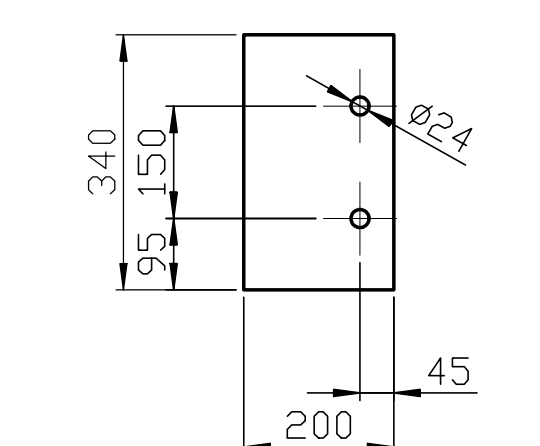


POS 015

THICKNESS 20mm
(SCALE 1:10)

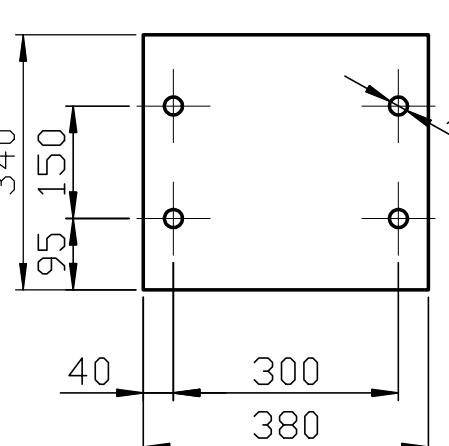


POS 016

THICKNESS 20mm
(SCALE 1:10)

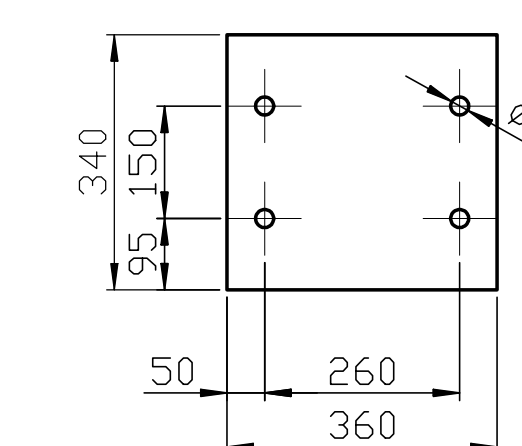


POS 017

THICKNESS 20mm
(SCALE 1:10)

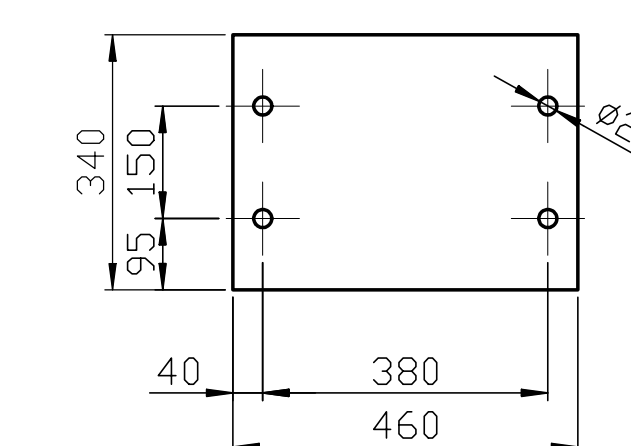


POS 018

THICKNESS 20mm
(SCALE 1:10)

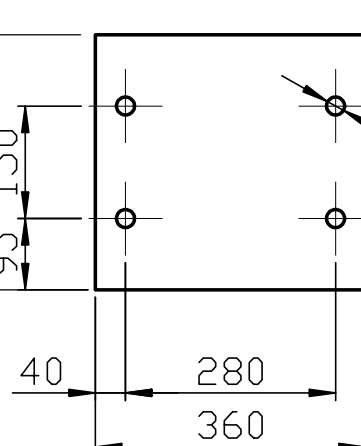


POS 019

THICKNESS 12mm
(SCALE 1:5)

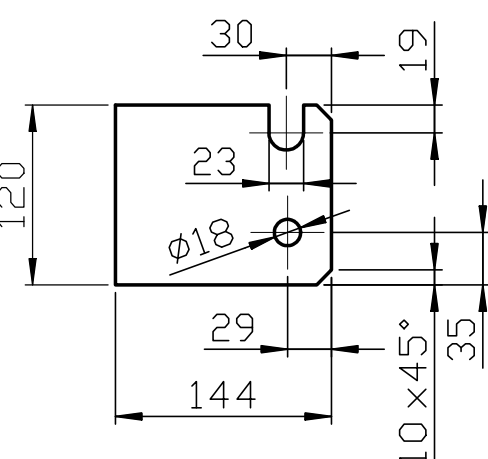


POS 020

THICKNESS 15mm
(SCALE 1:5)

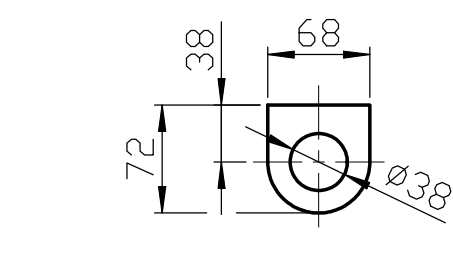


POS 021


EARTHING CONNECTION
(SCALE 1:2)

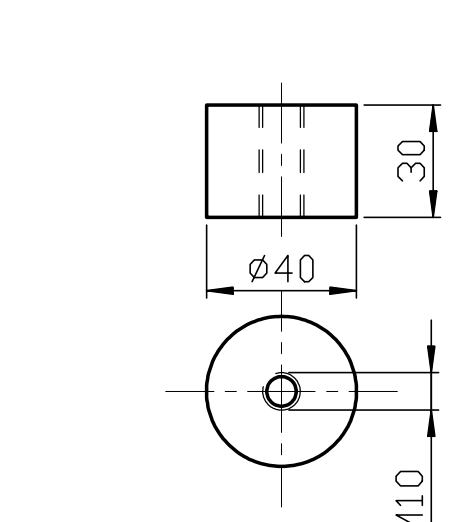


SECTION N-N

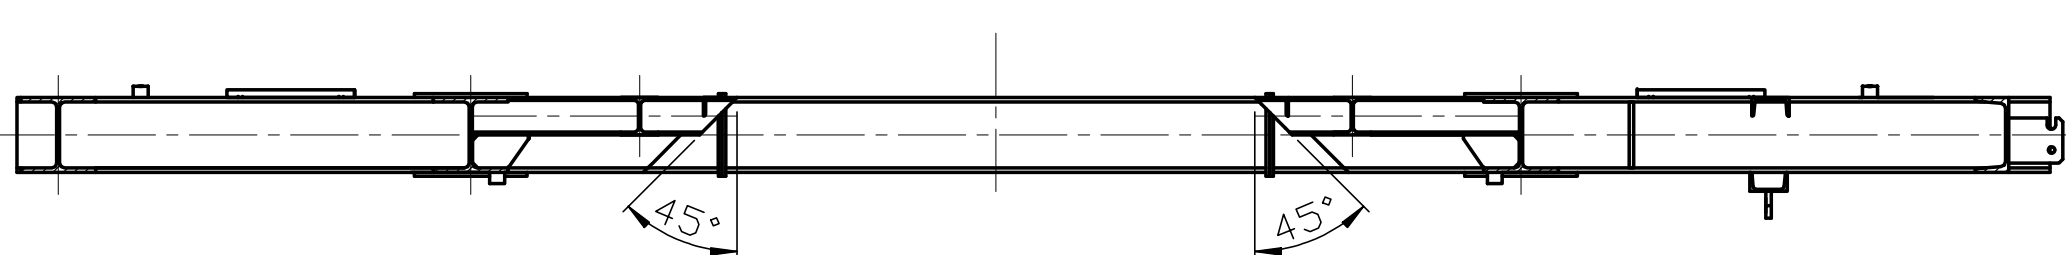


SECTION O-O

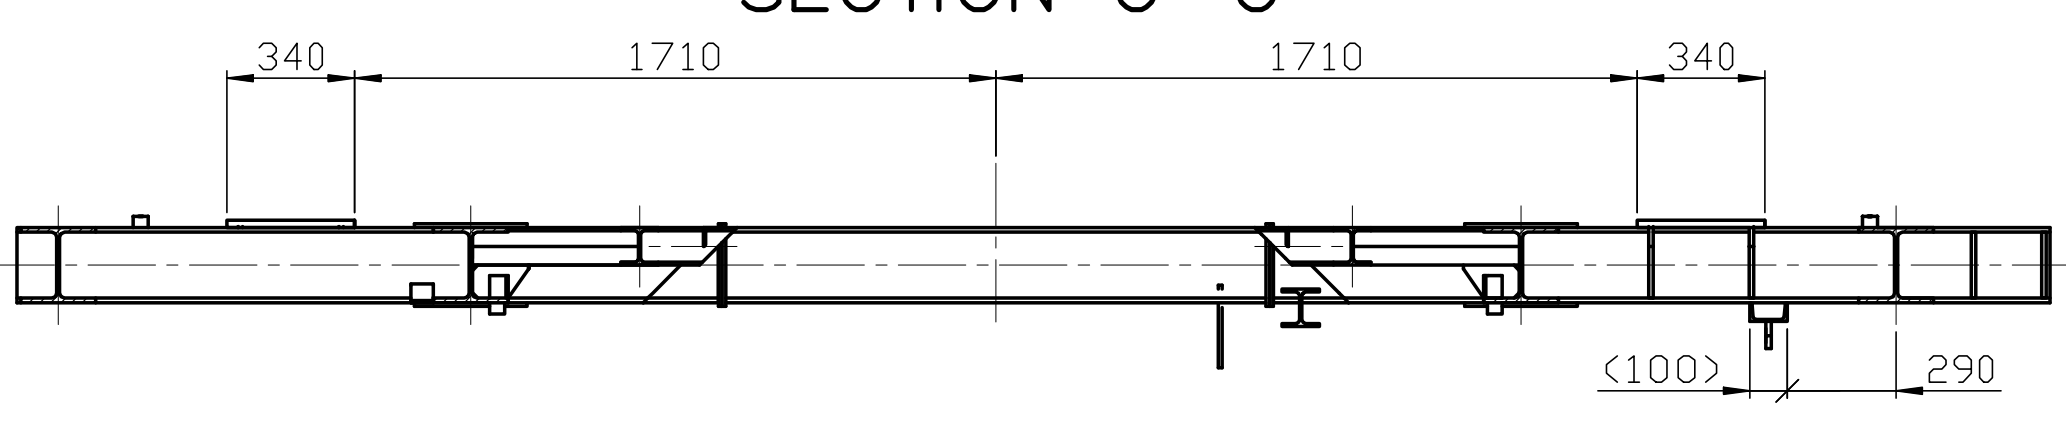


SECTION P-P

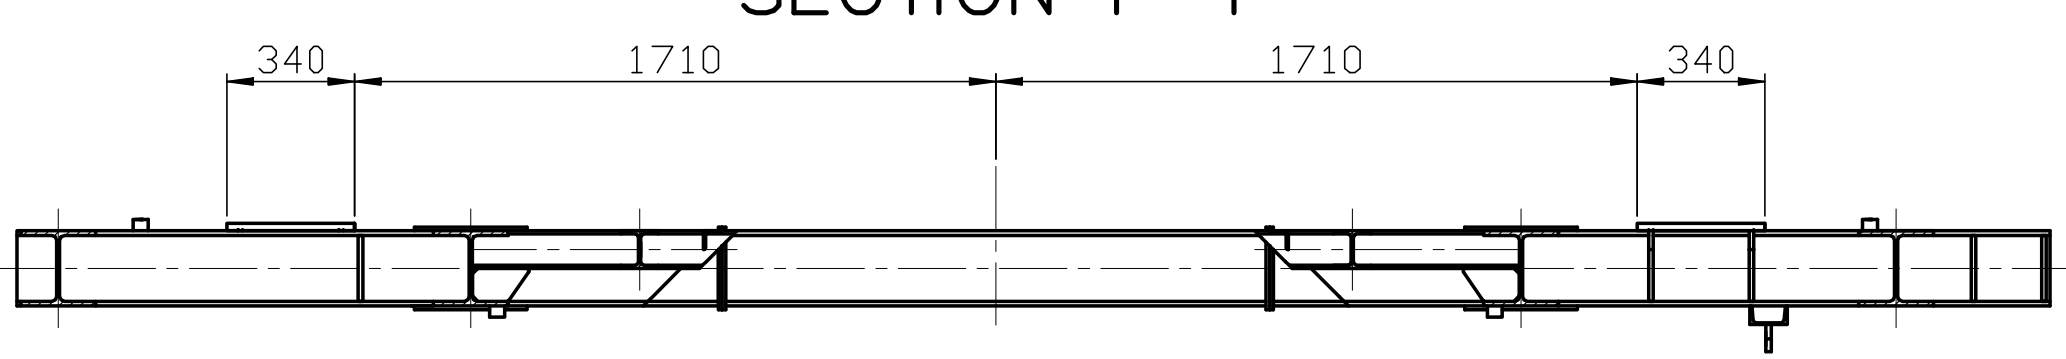

SECTION Q-Q

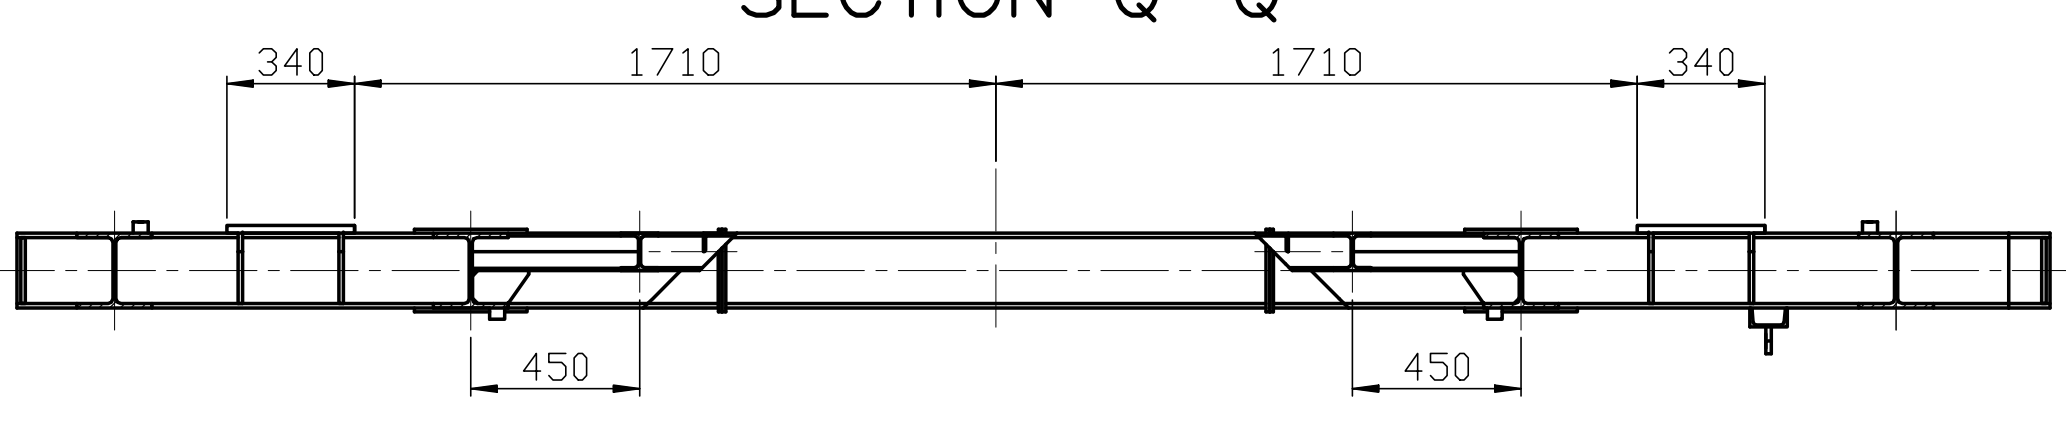

SECTION R-R

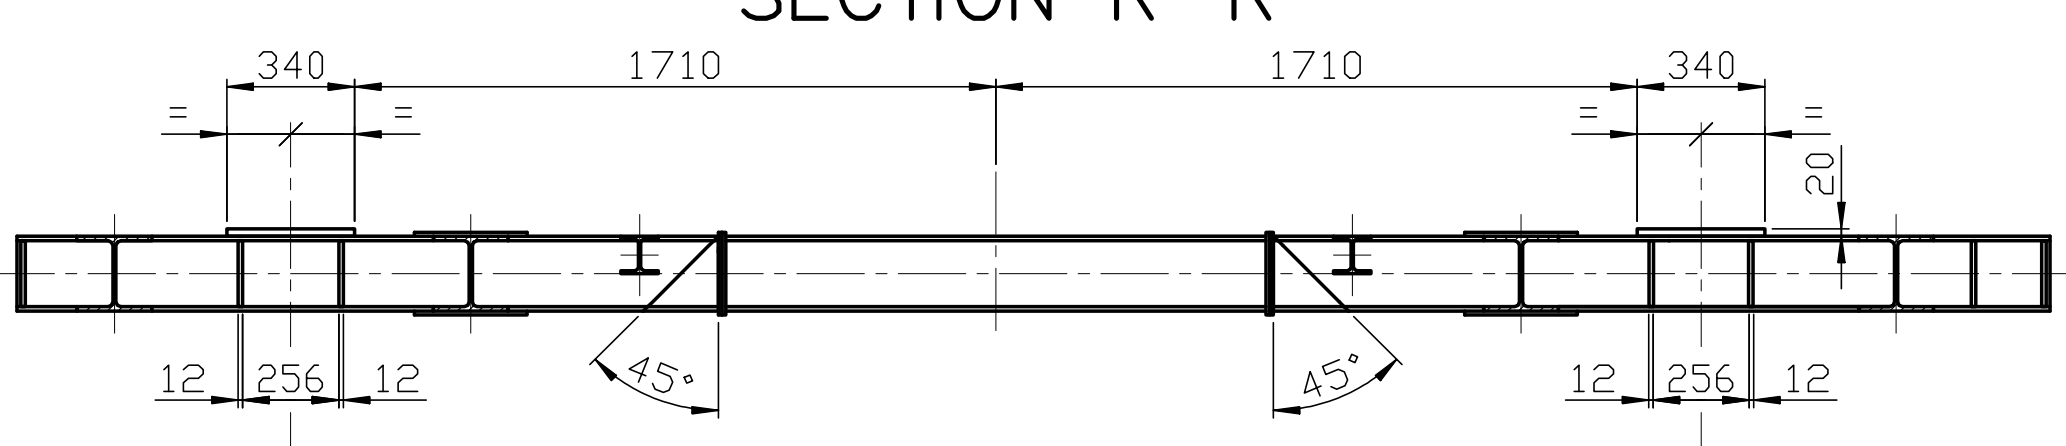

This drawing is entrusted to the recipient person-
ally, but the copyright remains with us. It must
not be copied, reproduced or in any way communi-
cated or made accessible to third parties without our
written consent.
Similar Draw.
Marking regulations see Drawing Standards.

Author		Checked		Designed		Drawn		Date	
TONELLI_M		04-08-2025							
Name		Date		Name		Date		Name	
Replaced by		Design group		Subst. for		Orig. scale			
HANWHA OCEAN		3LP165E-3C26		STEEL STRUCTURE		TOP PLATFORM		Drawn: 24-02-2025	
L-0234		ASME		BOG-BOOSTER - COMPRESSOR		ITEM NO.: C-001		Verified: 01-04-2025	
CAD-Drawing		Part-No.		Bar - Code				Standards conform:	
Burkhardt Compression		E		0-125.629.718		3-3			