




SU03

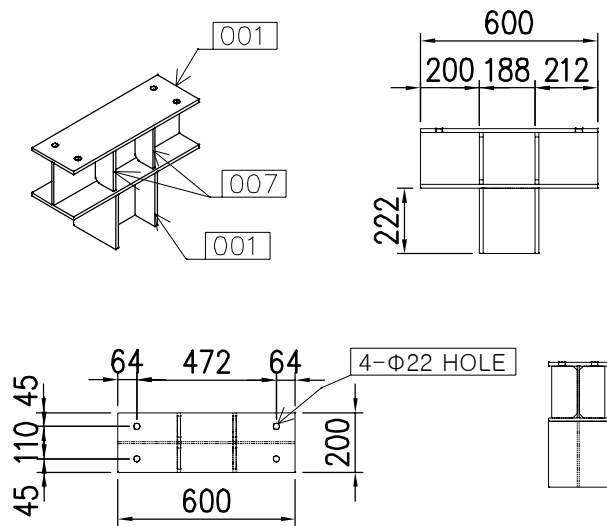


SU04

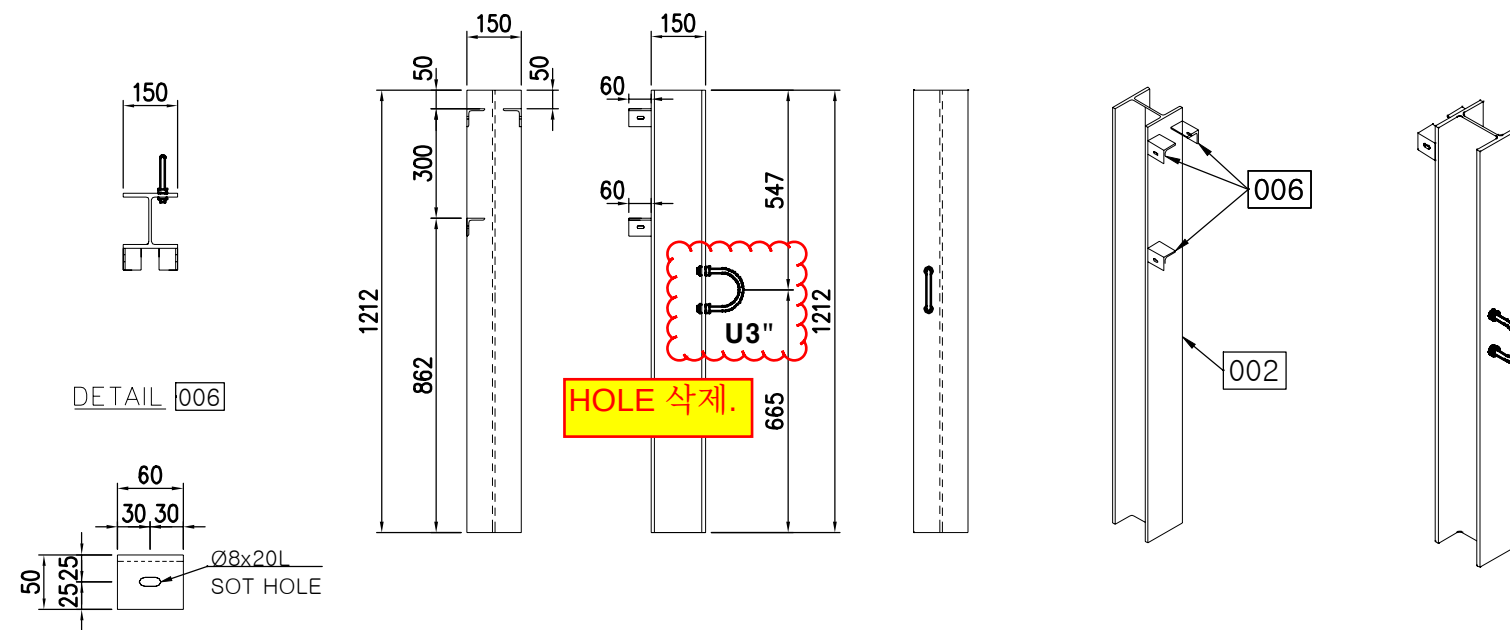

SU05

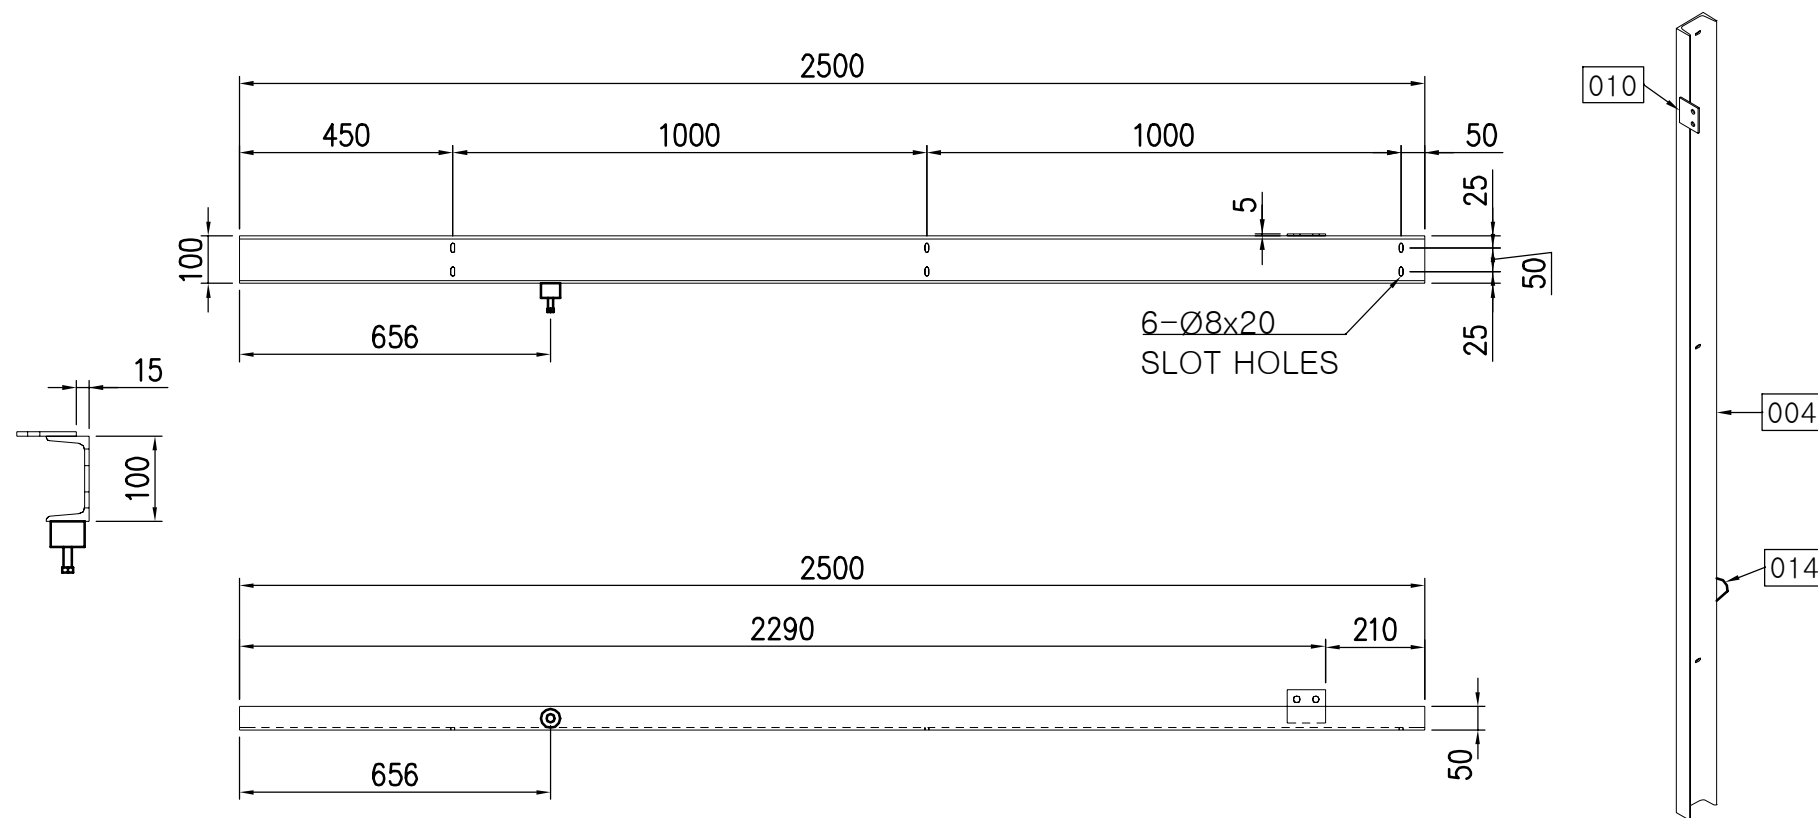

SU06

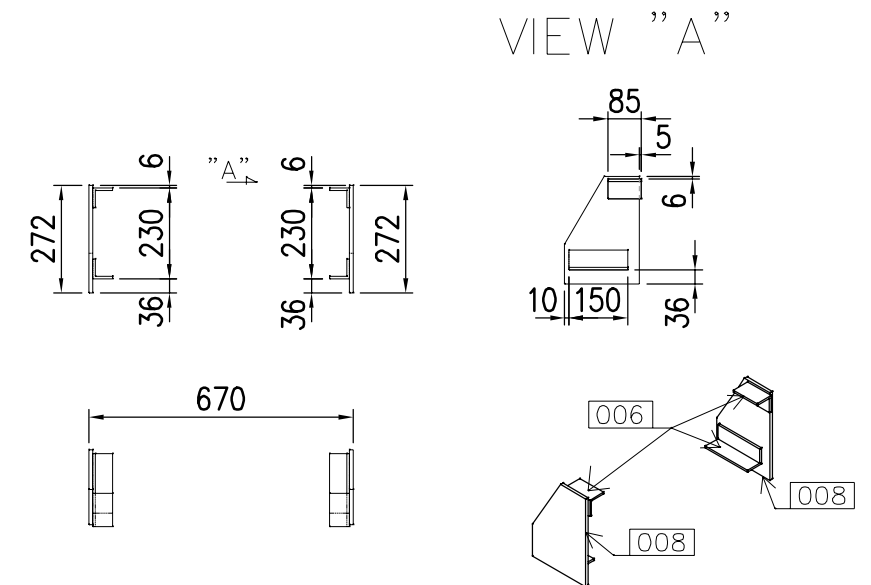

APPROVED 김 갑 진	PROJECT NO. D2537 5LP250V		
CHECKED 김 정 식	NAME OF DRAWING U-BOLT & CLAMP HOLE DWG FOR M1 SUPT(2/2)		
DRAWN 정 세 례			
TEL.NO. +82-51-260-5615			
DRAWING NO. SB-	CLASS -	SCALE -	
 SUNBO UNITECH CO., LTD.			