




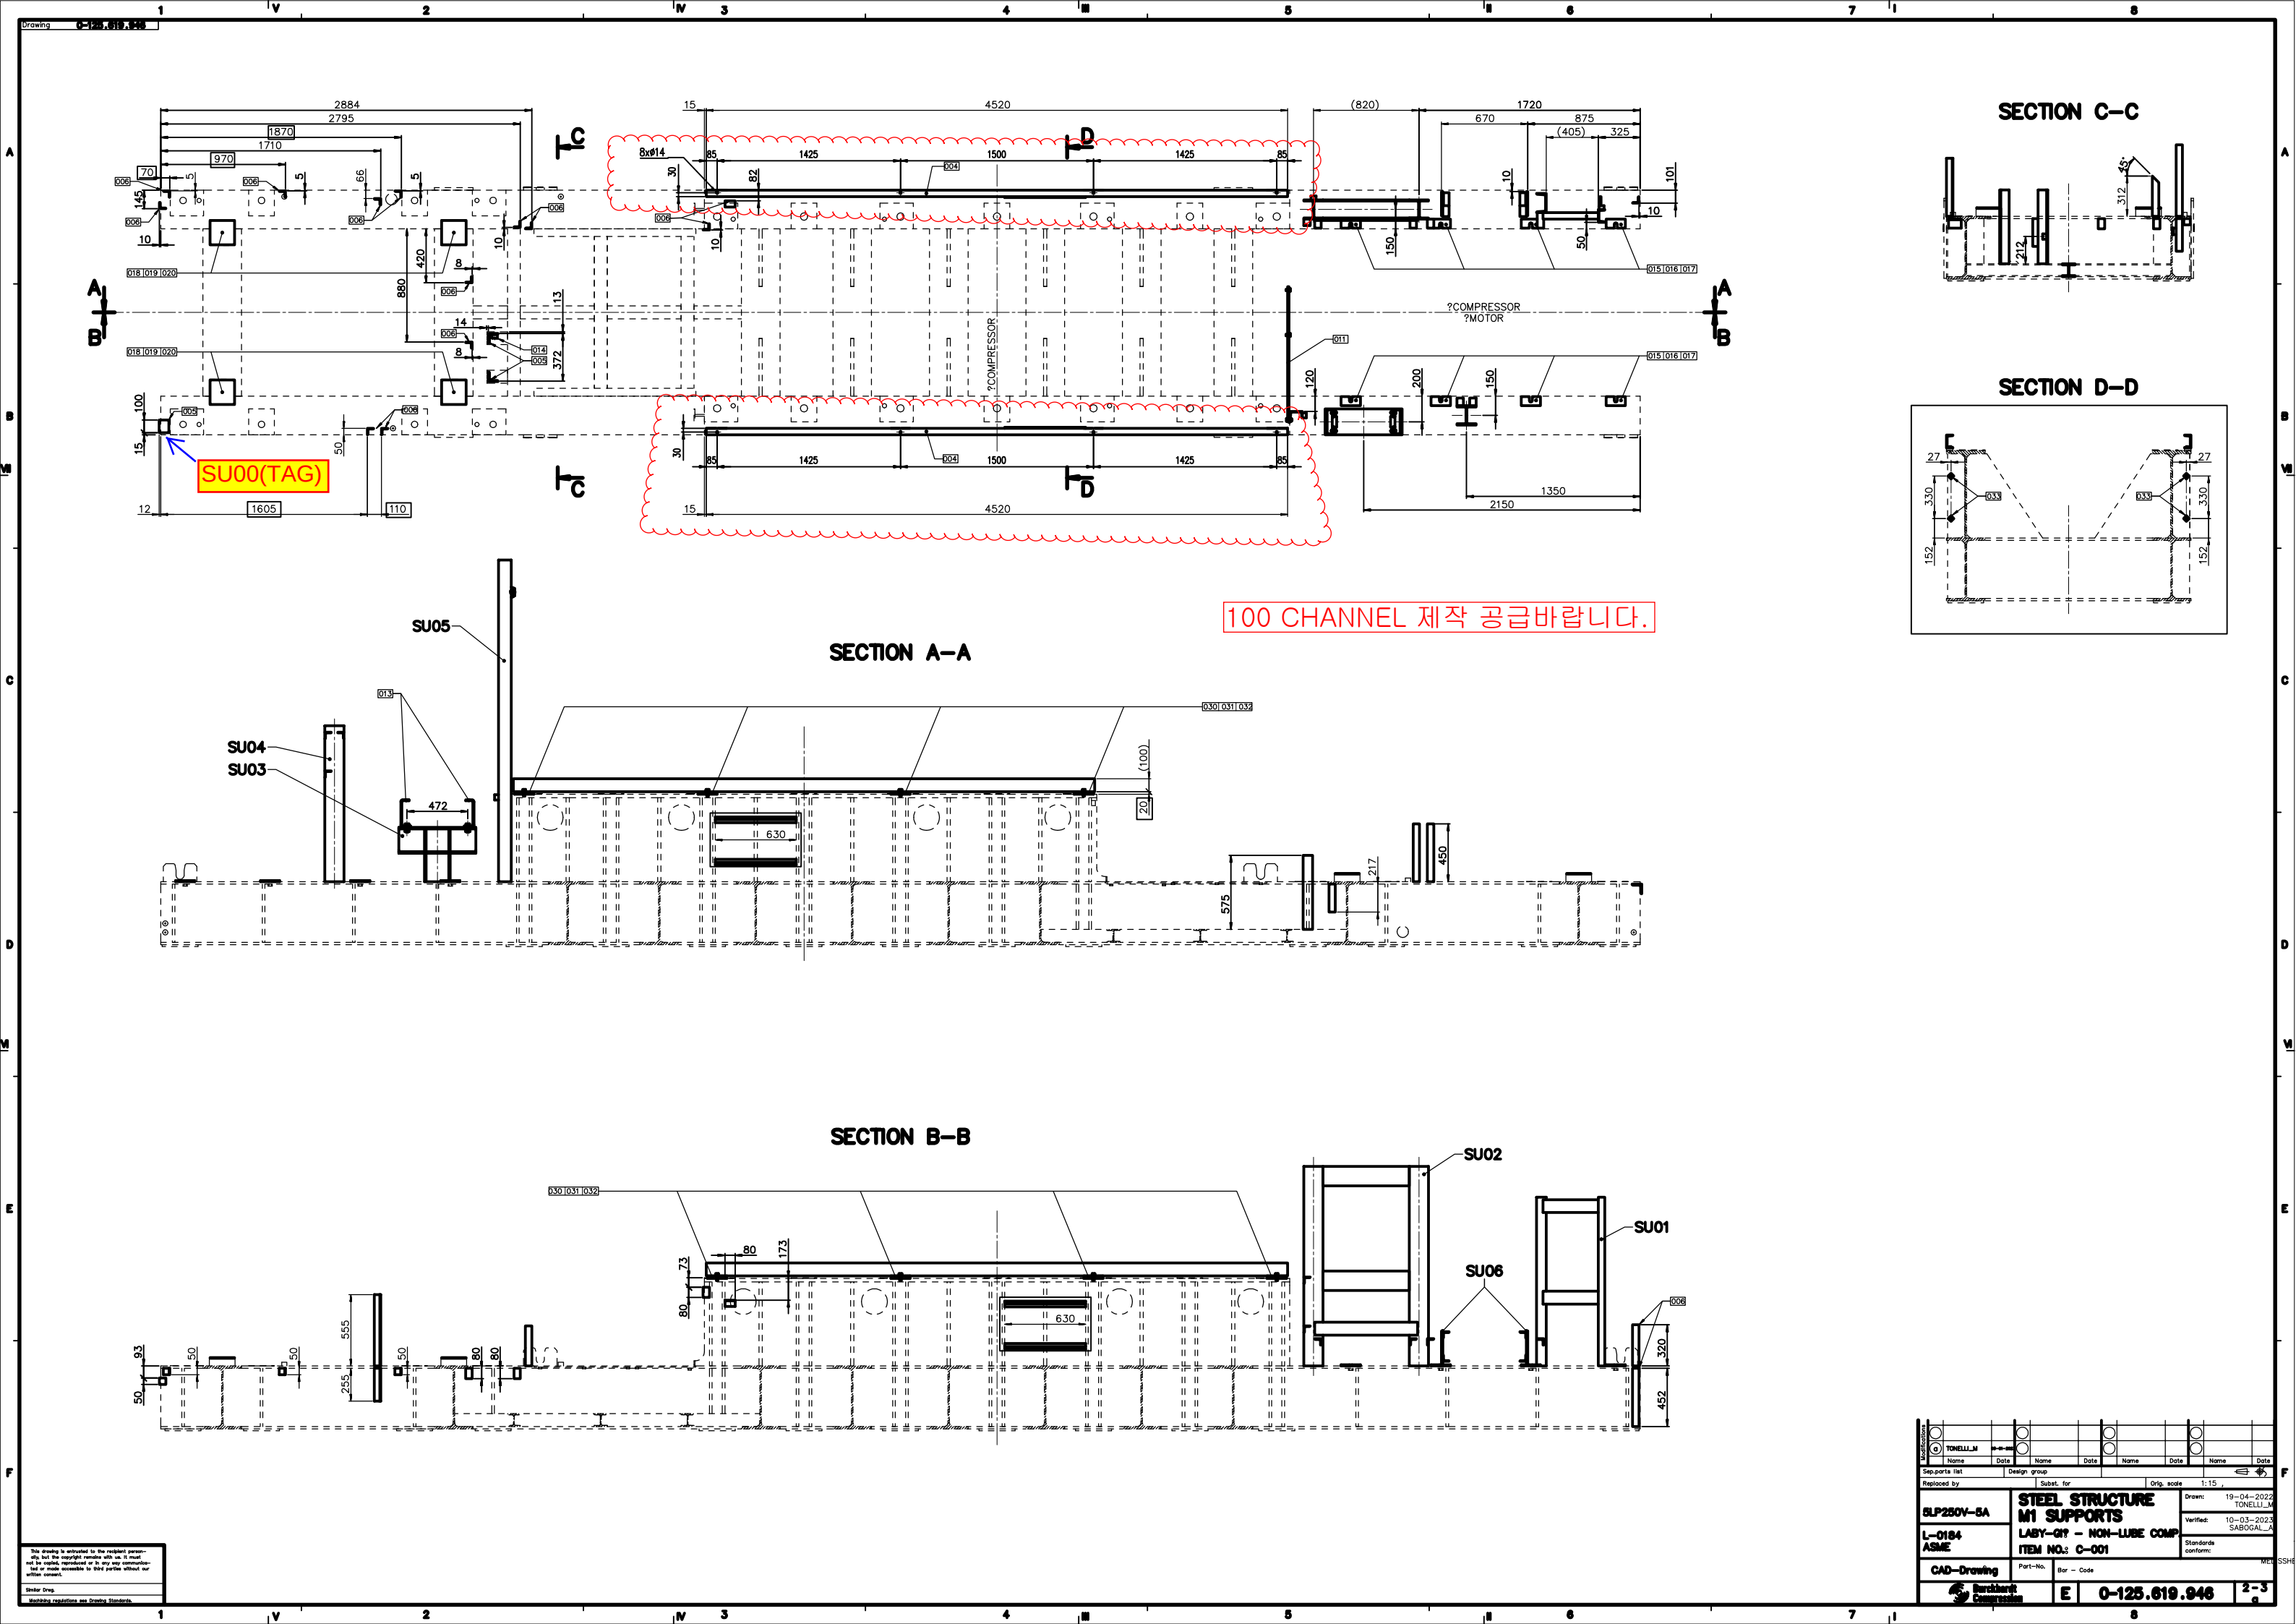


SECTION C-C

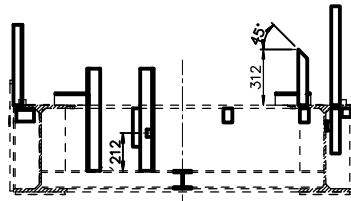


SECTION D-D

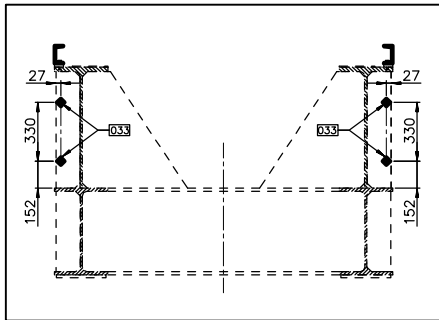

SECTION A-A

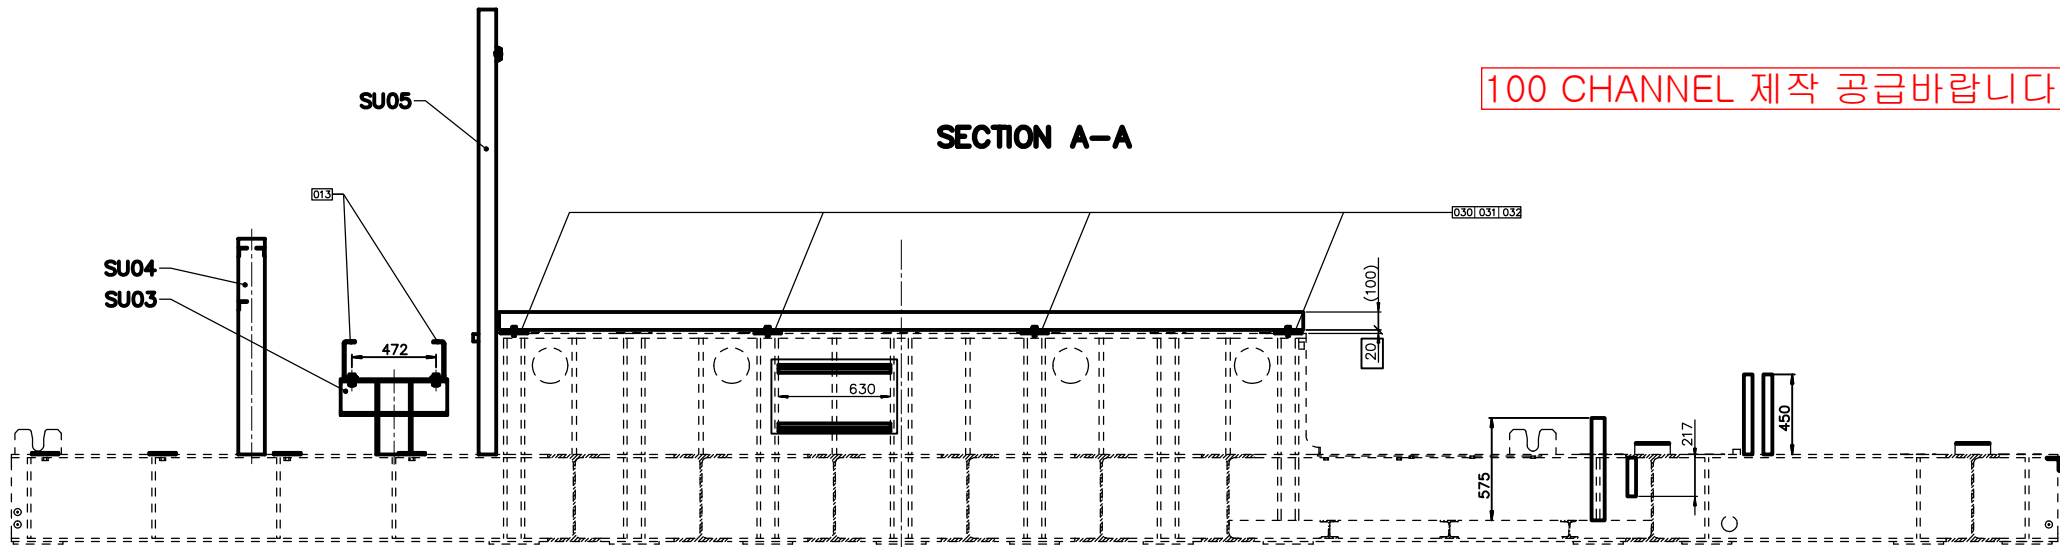

SECTION B-B

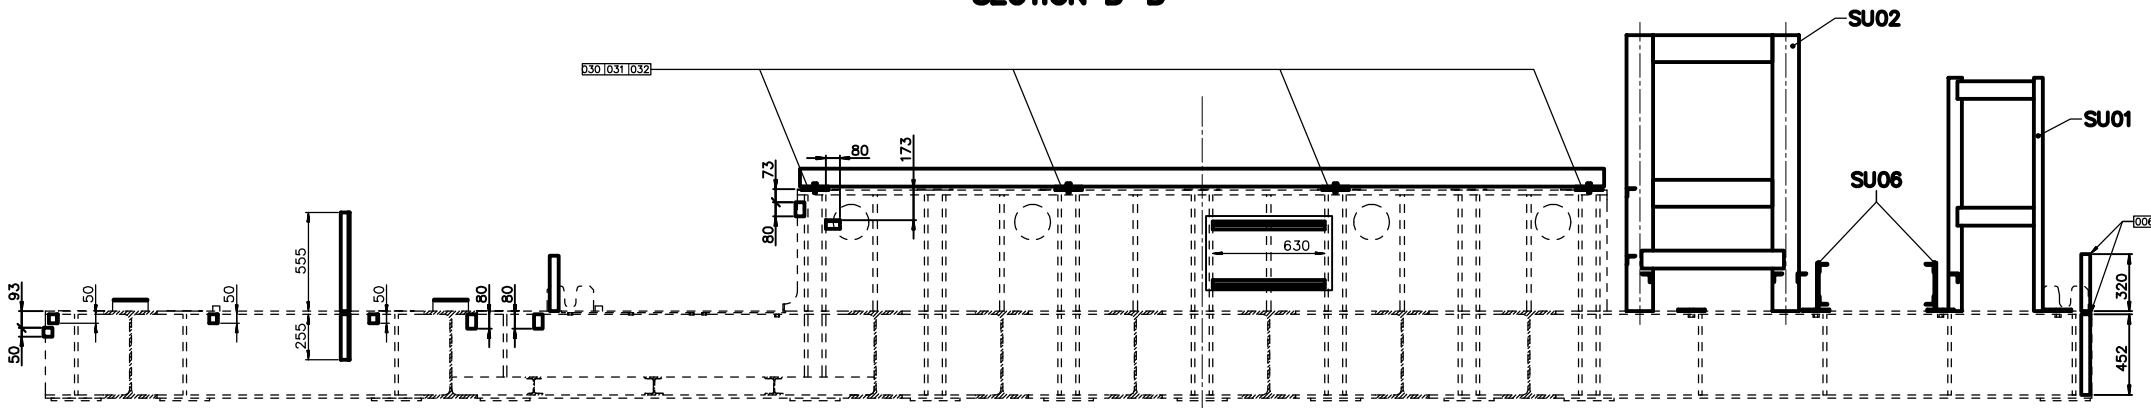

Name		Date	Name	Date	Name	Date	Name	Date
TONELLI_M								
Replaced by		Subst. for		Orig. scale		1:15		
SLP250V-6A		STEEL STRUCTURE		M1 SUPPORTS		Drawn: 19-04-2022		
L-0184		LABY-Q17 - NON-LUBE COMP		ITEM NO. C-001		Verified: 10-03-2023		
ASME						Standards conform:		
CAD-Drawing		Part-No.		Bar - Code				
Burchard Construction		E		0-125.619.946		2-3		

This drawing is submitted to the recipient as a design concept only. It is not to be used for construction or for any other purpose without the written consent of the design firm.

Similar Design

Working regulations are Drawing Standards