

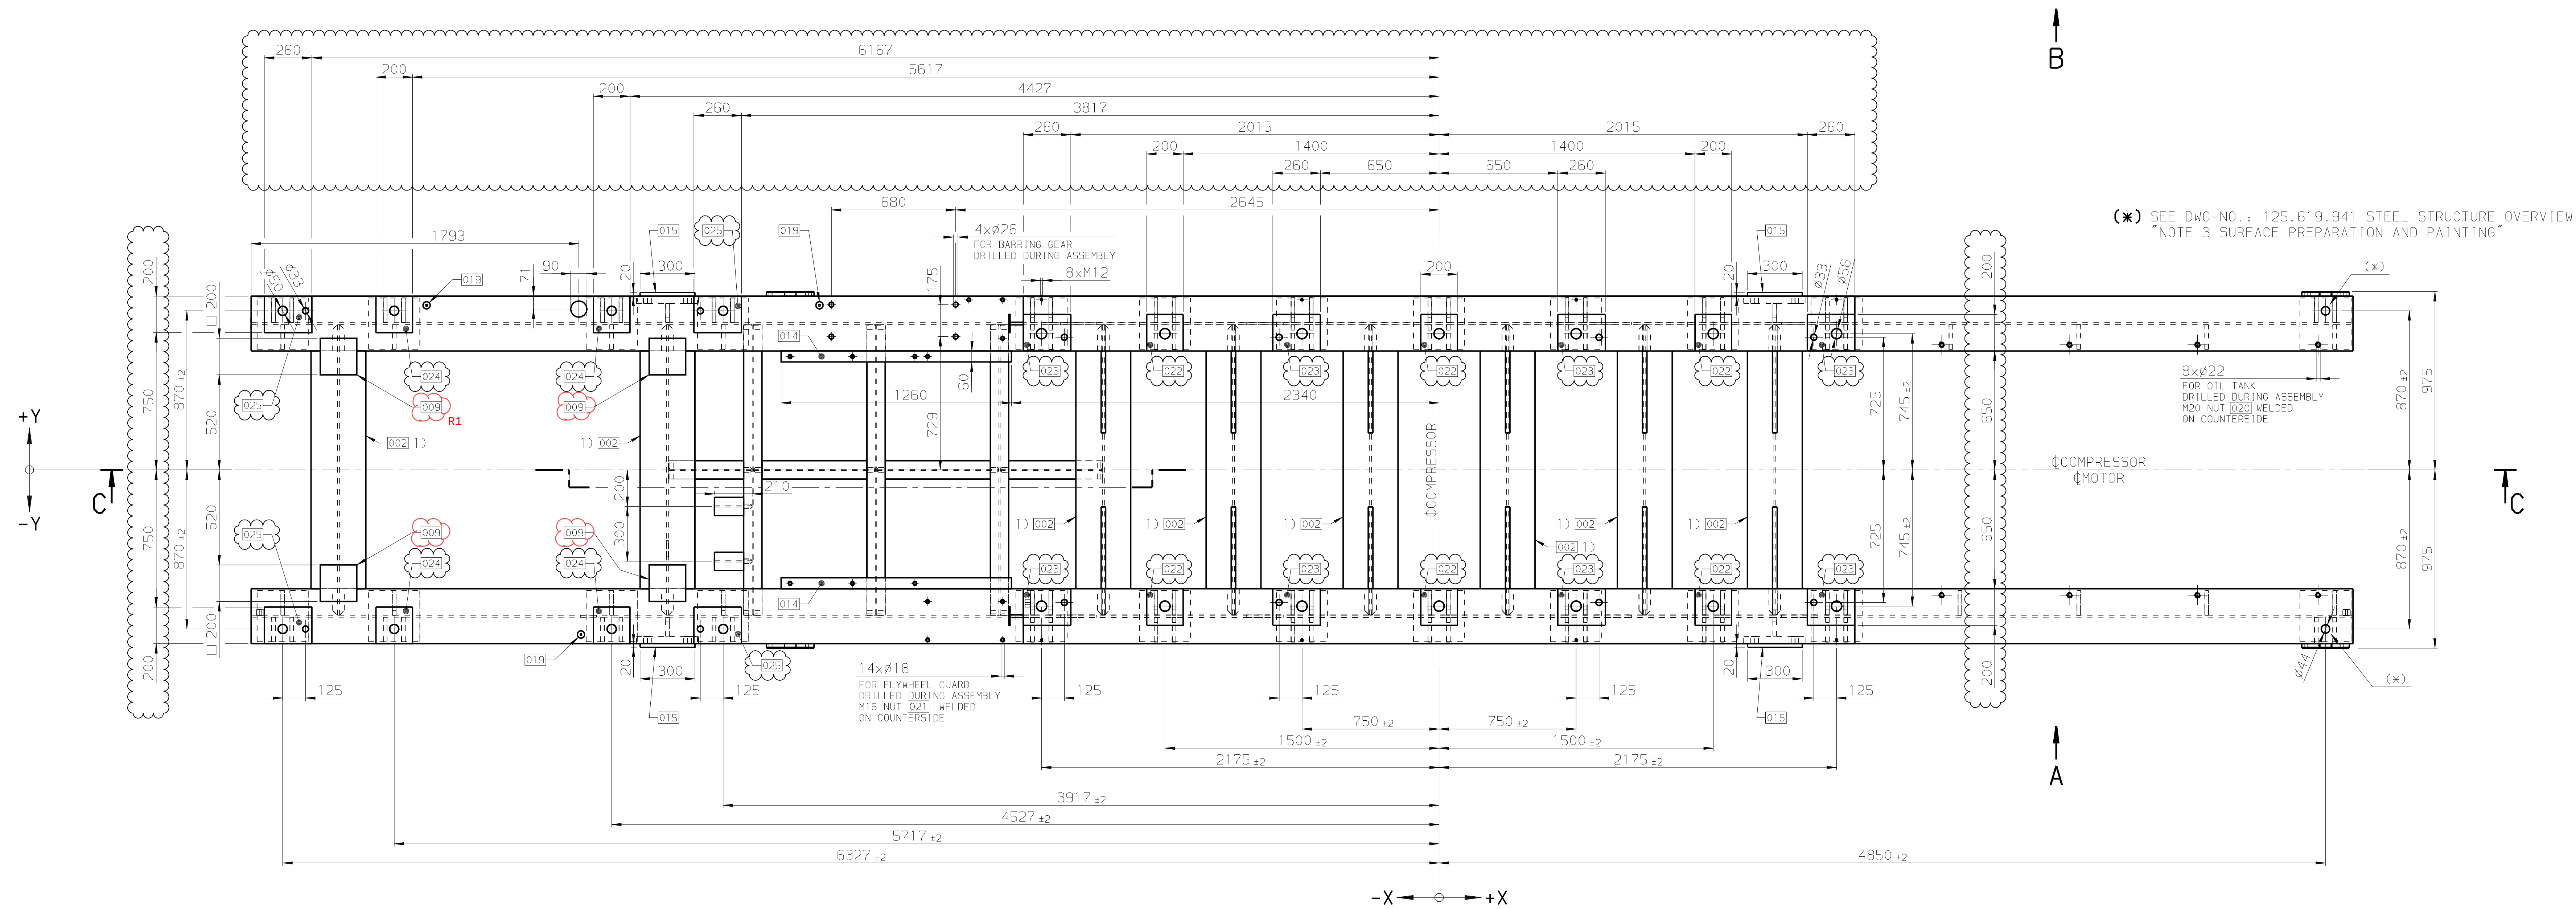


ALL NON MARKED H-BEAMS H100x100 003
1) FULL PENETRATION WELDED

VIEW A

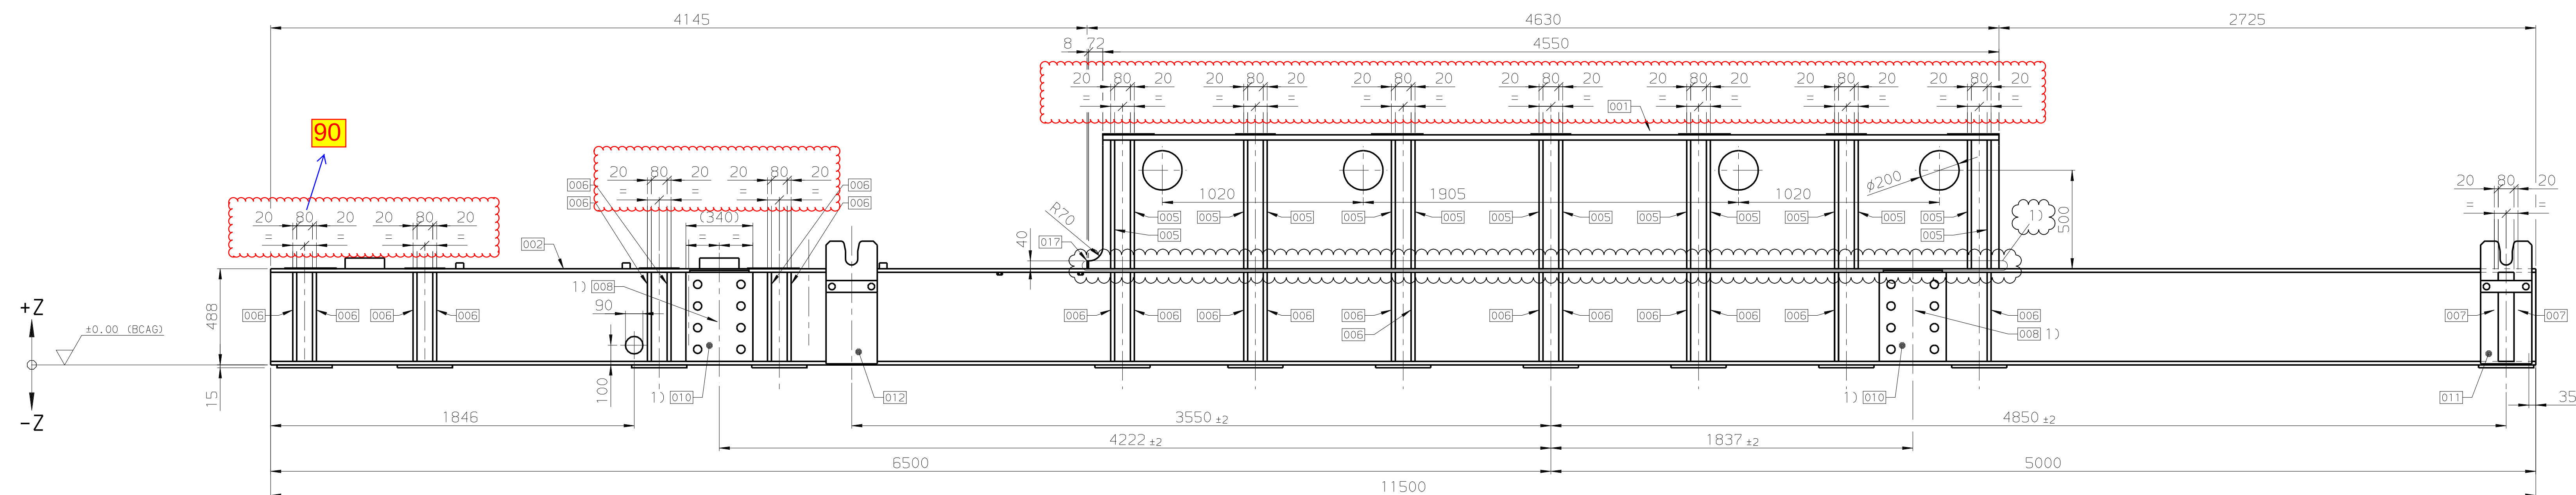

VIEW B

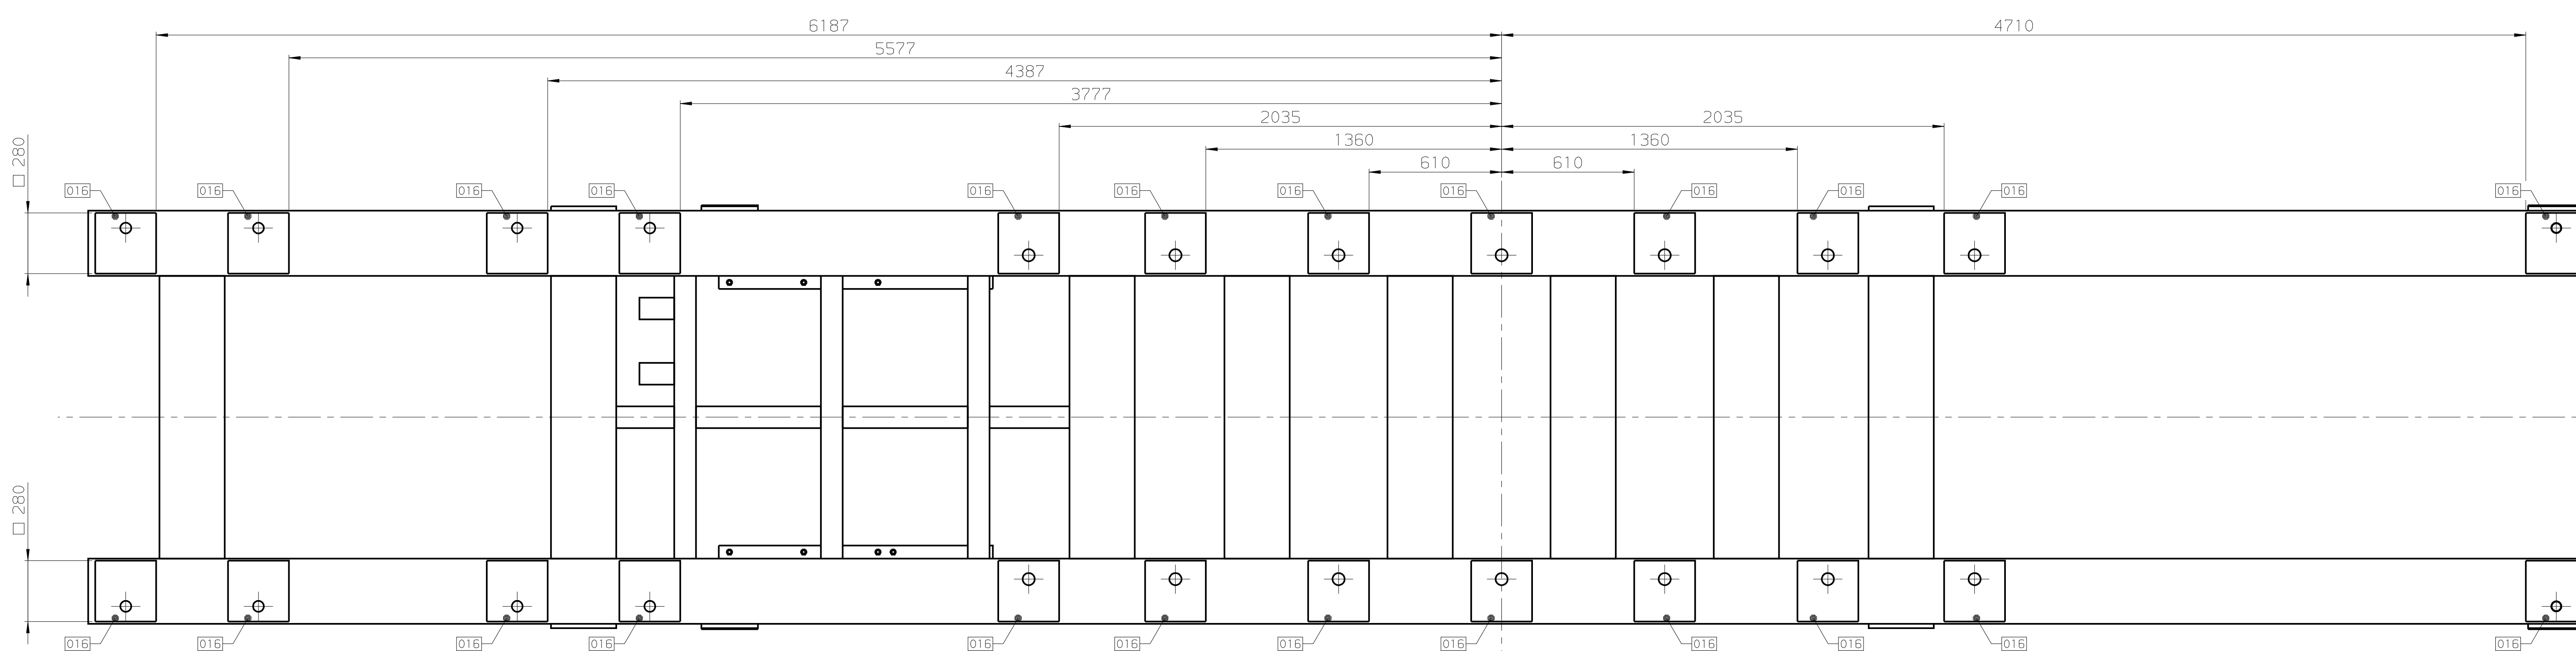

Date of release				
				
	TONELLI, M	24-07-2020	TONELLI, M	11-01-2021
	None	Date	None	Date
	TONELLI, M	24-07-2020	TONELLI, M	11-01-2021
	None	Date	None	Date
Suppliers List		Design group		 
Replaced by		Subst. For		Orig. scale 1:15
SLP250V-SA		STEEL STRUCTURE M1 BASE FRAME LBY-610 - NON-LUBE. CP. ITEM NO.: C-001		Drawn: 19-04-2020 TONELLI, M
				Verified: 22-02-2020 SABOGAL, L
				Standards conform:
L-0184 ASME		Part-No.	Ser. Code	
CAD-Drawing				
 Borchardt Compression		E	0-125.619.945	2 - 3