
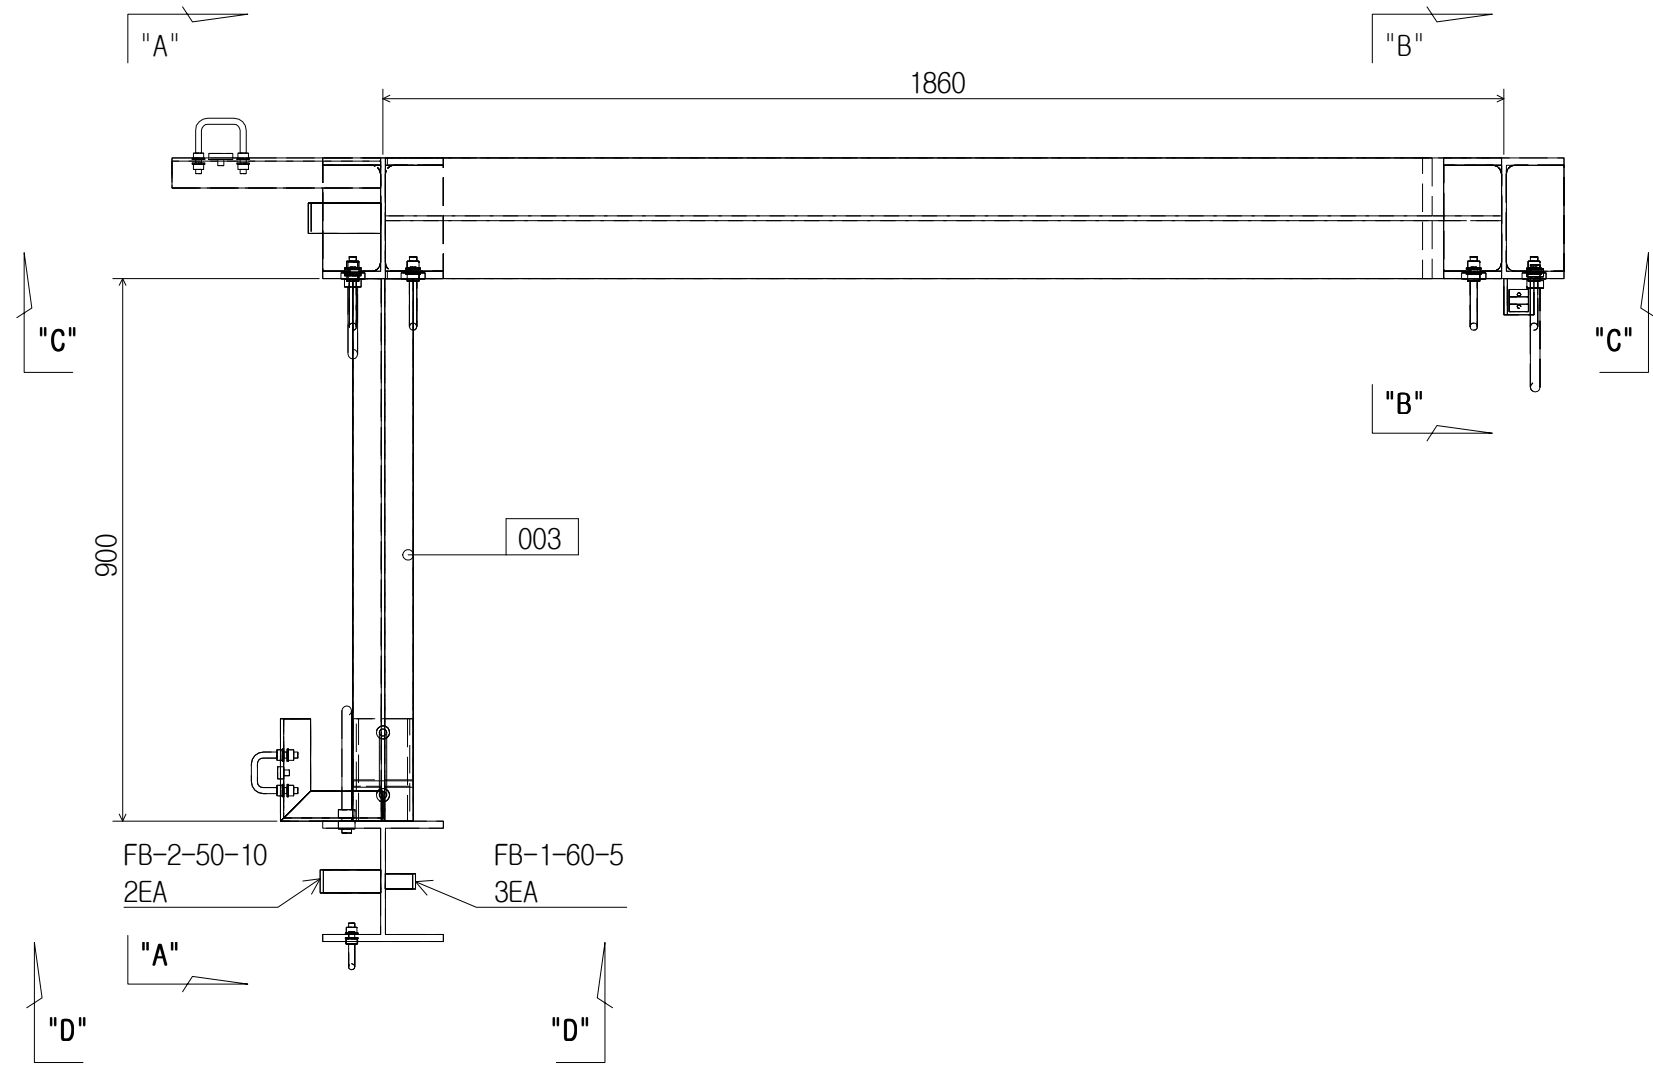


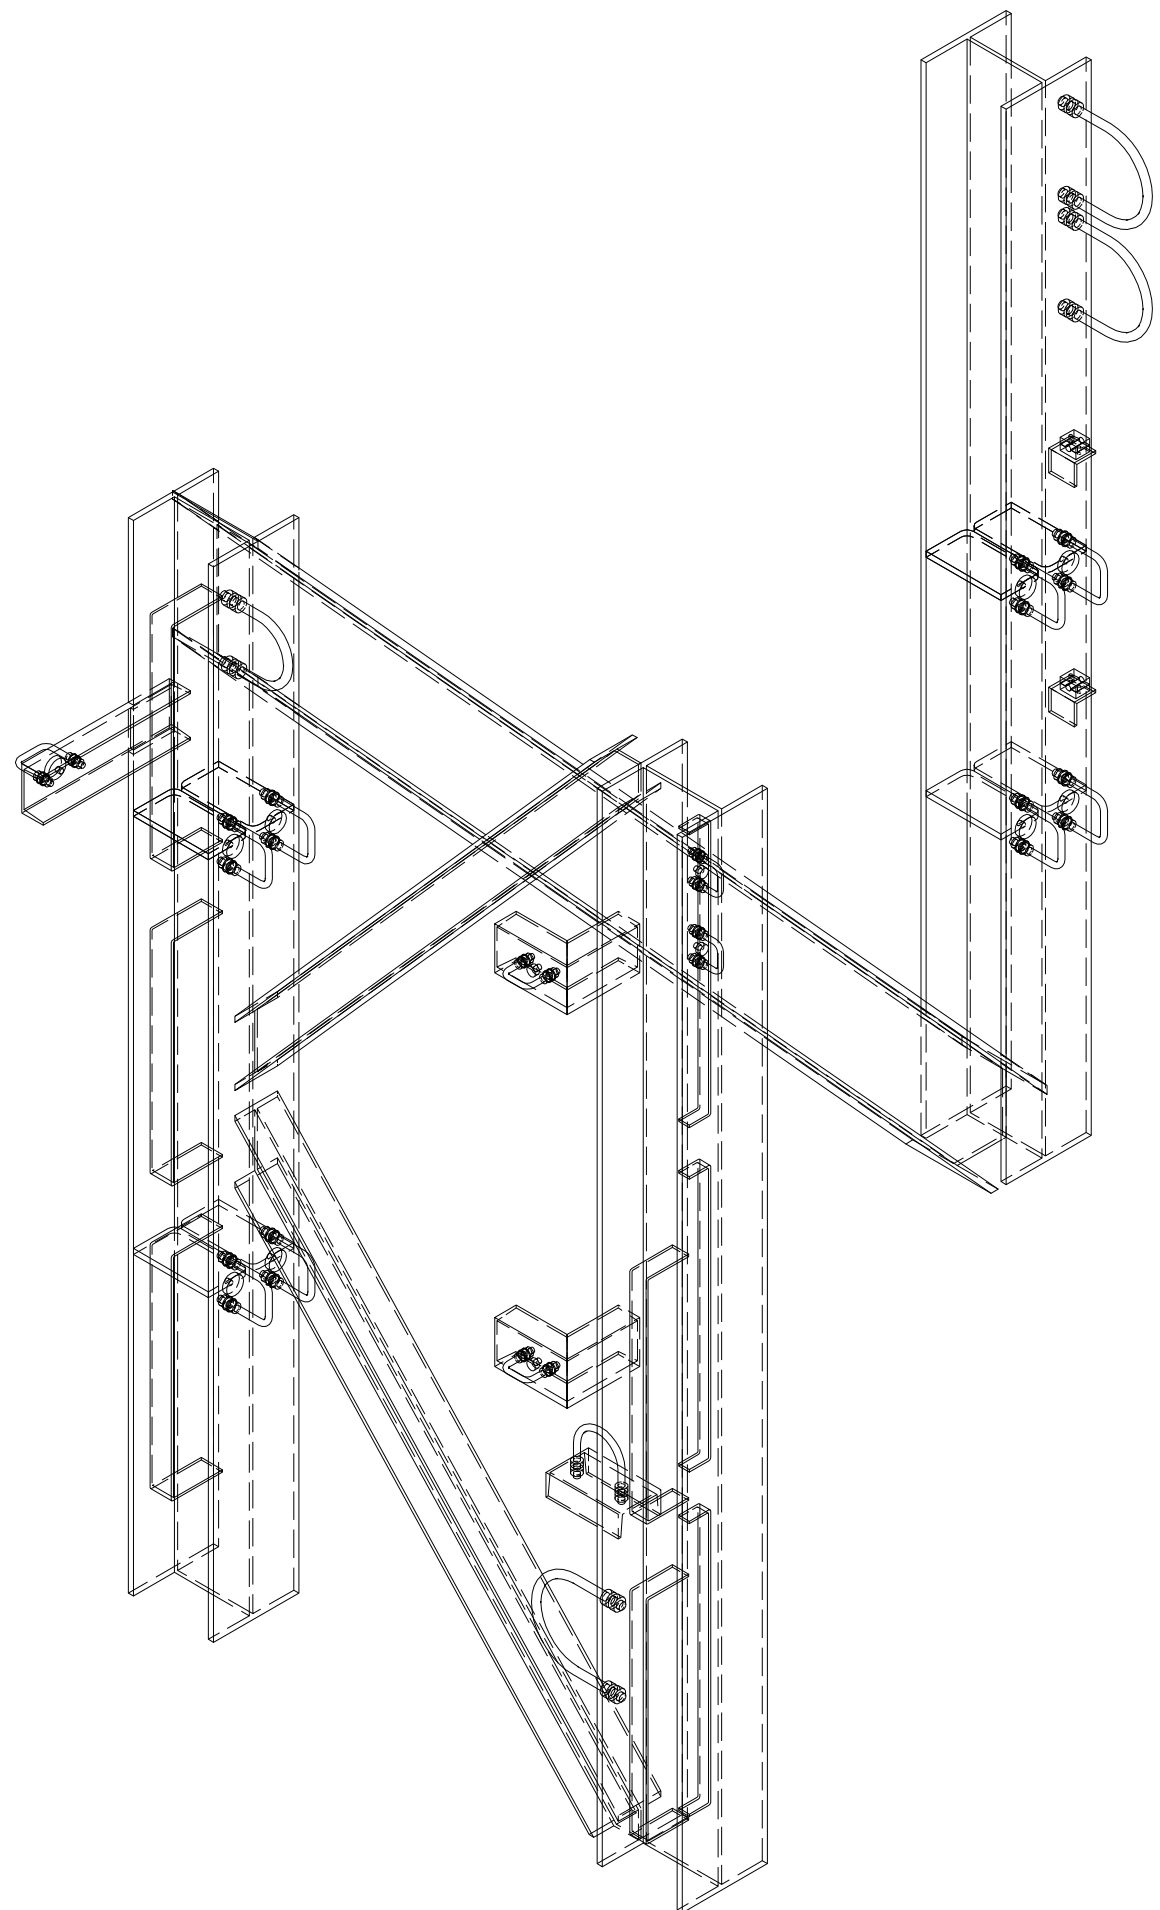

- ALL NON MARKED SLOT HOLE Ø8X20L 001
- ALL NON MARKED H-BEAMS H200x200 006
- ALL NON MARKED U-BEAMS CH100x50 008
- ALL NON MARKED L-BEAMS L50x50 009
- ALL NON MARKED STIFFENER FOR H200x200

APPROVED 김갑진	PROJECT NO. D2585 3LP165		
CHECKED 김영광	NAME OF DRAWING		
DRAWN 강지혜	STEEL STRUCTURE		
TEL. NO. +82-51-260-5640	SUPPORTS & PILARS		
DRAWING NO. SB-	CLASS DNV	SCALE -	☉
SUNBO UNITECH CO., LTD.			