

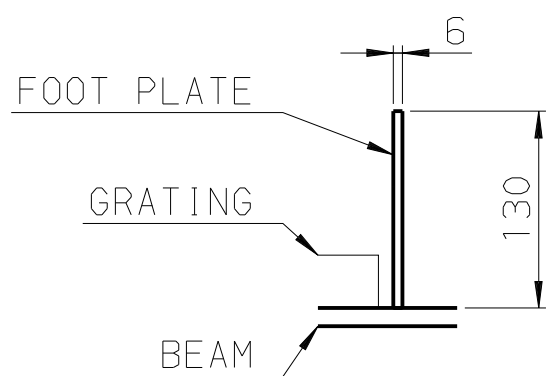


TYPICAL FOR
POS 001 FOOT PLATE
(SCALE 1:5)

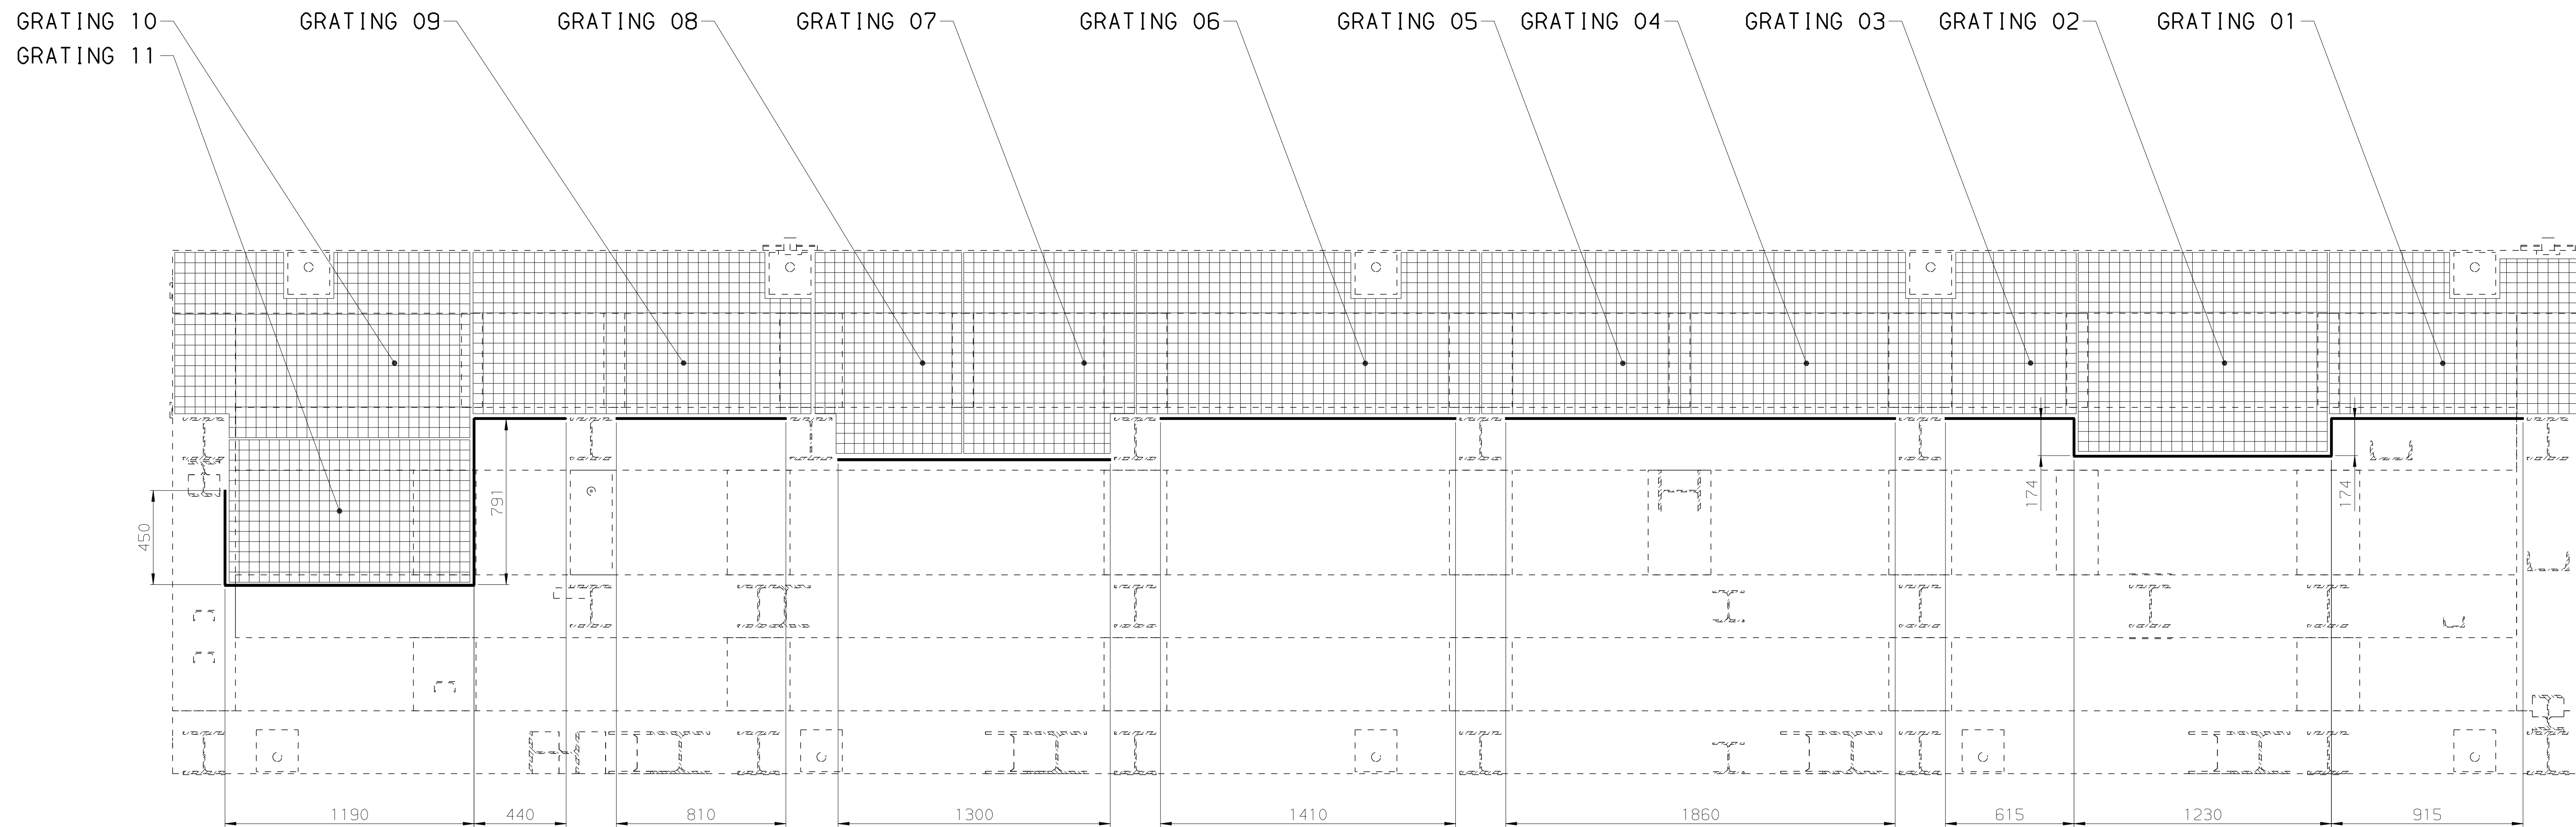

TYPICAL FOR
POS 002 FOOT PLATE
(SCALE 1:5)

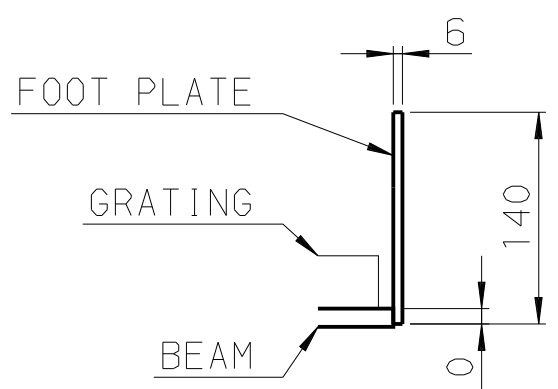

No.	Revision	(a)	(b)	(c)	(d)	Date
		TONELLI_M	TONELLI_M	TONELLI_M	TONELLI_M	
		11-17-2021	20-08-2021	21-12-2021	21-12-2021	
		Name	Name	Name	Name	Name
Supp. parts list		Design group		 		
Replaced by		Subst. for		Orig. scale 1:15		
SLP250V-SA		STEEL STRUCTURE M3 RAILING AND GRATING LABY-610 - NON-LUBE COMP. ITEM NO. : C-001			Drawn: 19-04-2022	
					TONELLI_M	
					Verified: 08-03-2022	
L-0184 ASME					SABOGAL_A	
					Standards conform:	
CAD-Drawing		Part-No.	Bar - Code			
 Burckhardt Compression		E	0-125.619.977		2 - d	
					4	

This drawing is entrusted to the recipient personally, but the copyright remains with us. It must not be copied, reproduced or in any way communicated or made accessible to third parties without our written consent.

Similar Drug.

Machining regulations see Drawing Standards,