



SUPPORT 취부도 (5 / 14)

PLAN VIEW "D"

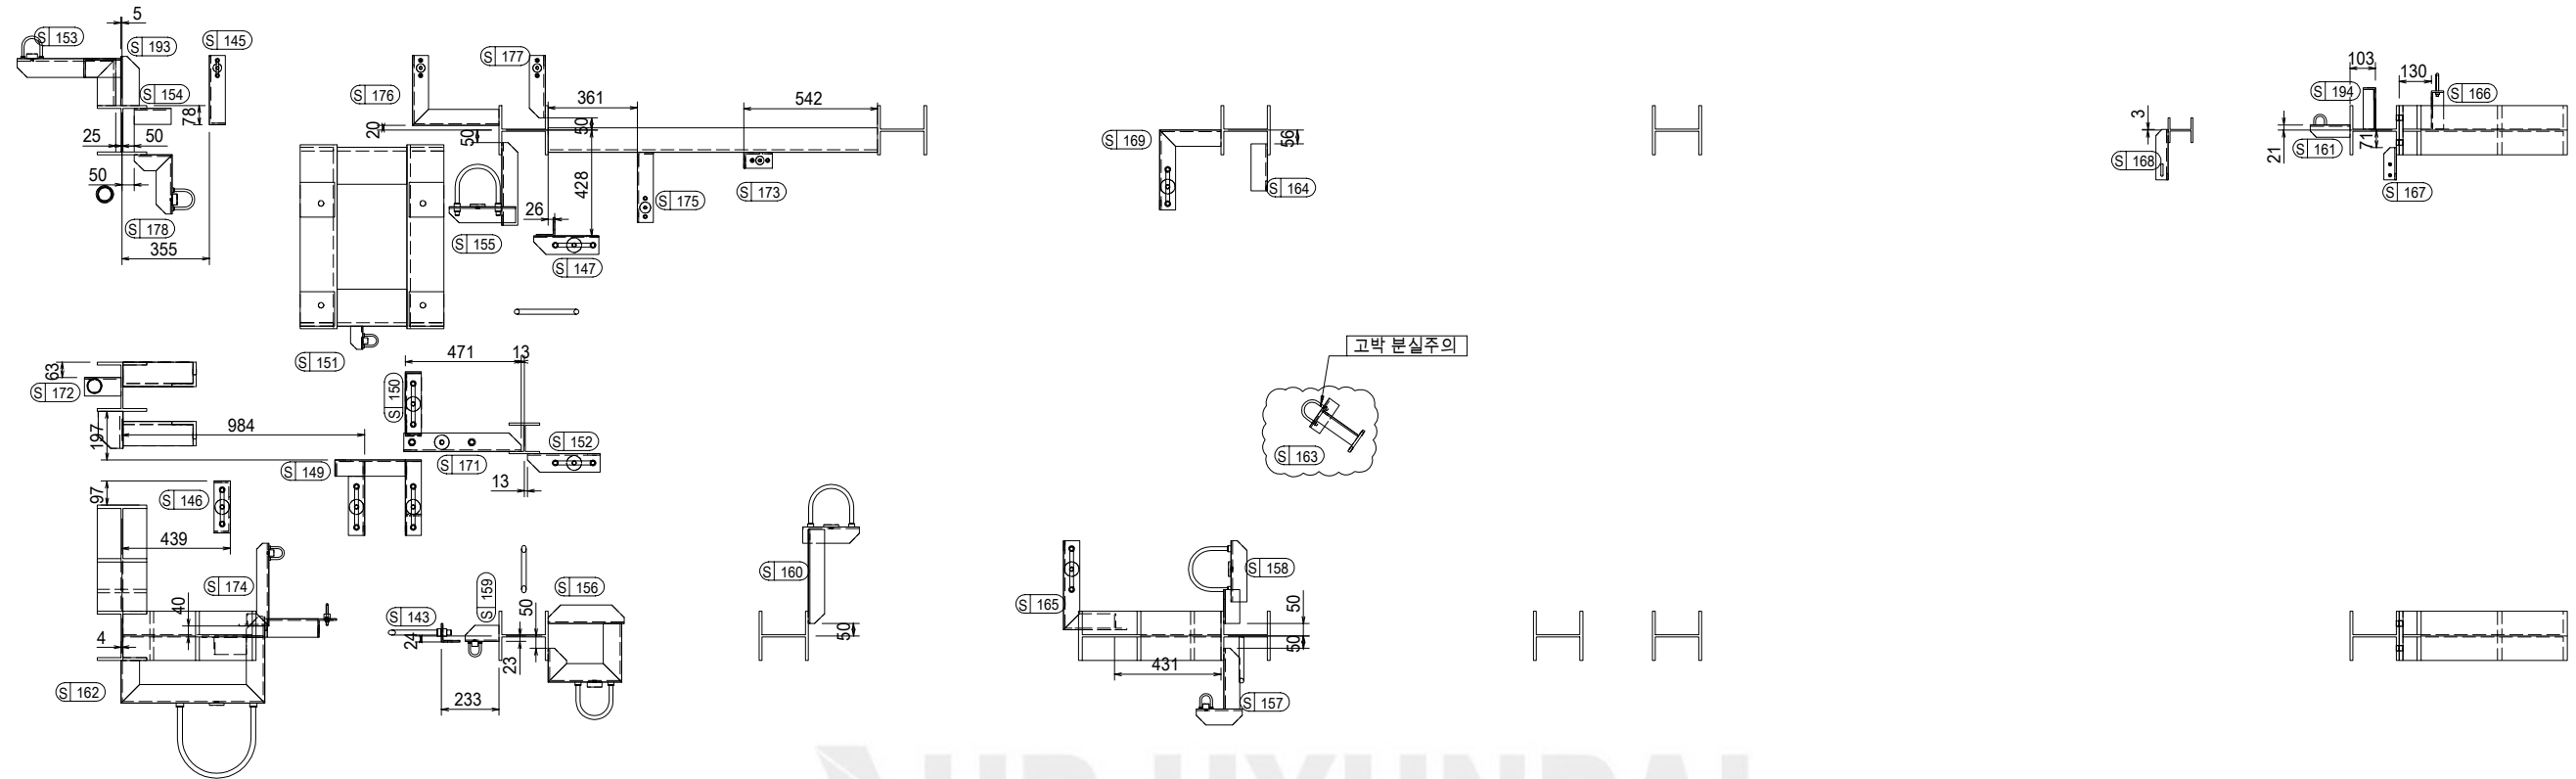

PLAN VIEW "E"

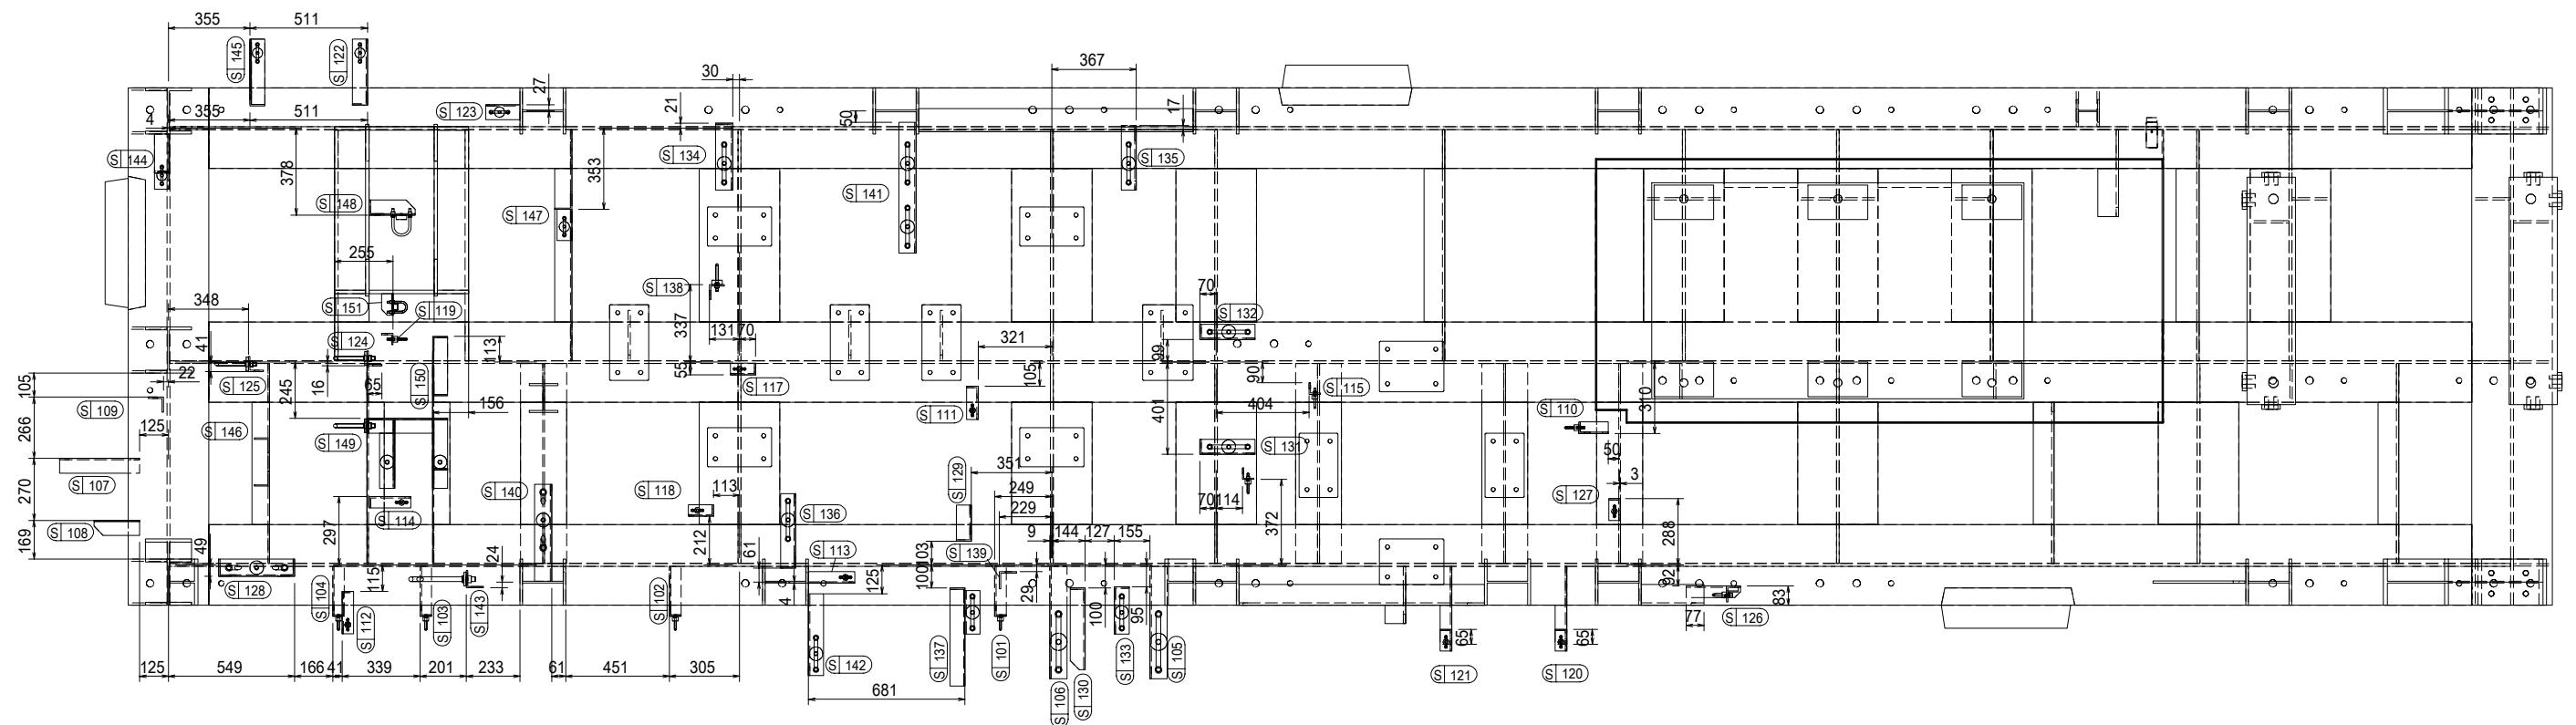

해당표기 SUPP는
정위치 T/W할 것.