



POS 009

THICKNESS 12mm
(SCALE 1:5)

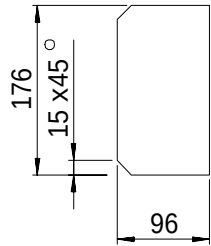


POS 010

THICKNESS 10mm
(SCALE 1:5)

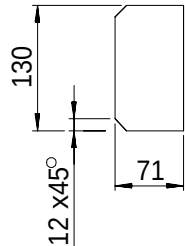


POS 011

THICKNESS 15mm
(SCALE 1:5)

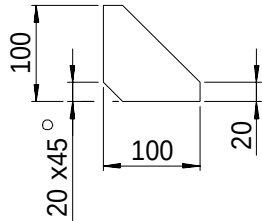


POS 012

THICKNESS 15mm
(SCALE 1:5)

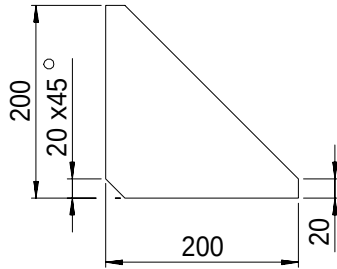


POS 013

THICKNESS 8mm
(SCALE 1:5)

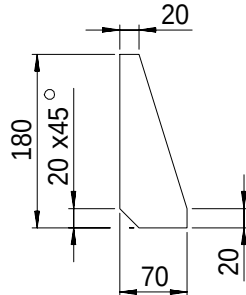


POS 014

THICKNESS 5mm
(SCALE 1:10)

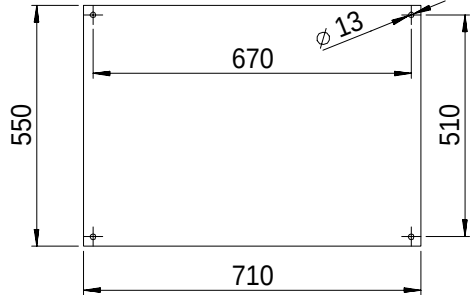


POS 015

THICKNESS 20mm
(SCALE 1:5)

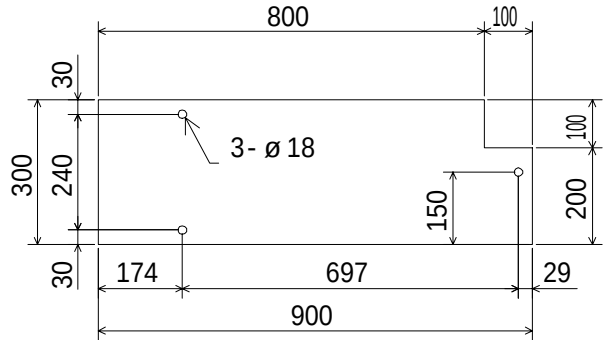


POS 016

THICKNESS 10mm
(SCALE 1:5)

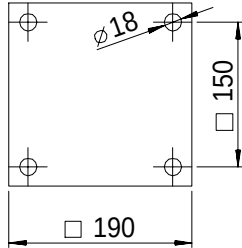


POS 017

THICKNESS 10mm
(SCALE 1:5)

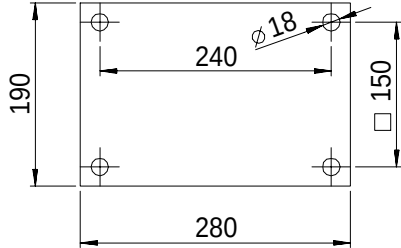


POS 018

THICKNESS 8mm
(SCALE 1:5)

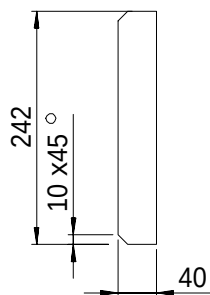


POS 019

THICKNESS 8mm
(SCALE 1:5)

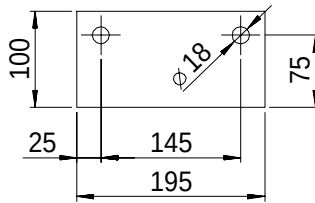


POS 025

EARTHING CONNECTION
(SCALE 1:2)

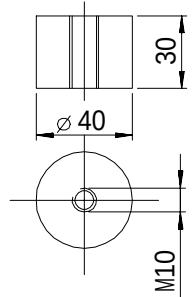


POS 030

THICKNESS 3mm
(SCALE 1:5)

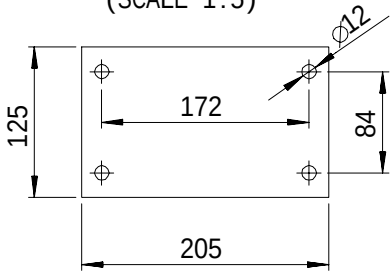

POS 031

THICKNESS 15mm
(SCALE 1:10)

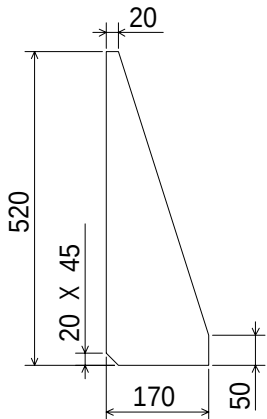

APPROVED 감 진		PROJECT NO. D2585 3LP165		
CHECKED 김 영 광		NAME OF DRAWING STEEL STRUCTURE SUPPORTS & PILARS		
DRAWN 강 지 해				
TEL. NO. +82-51-260-5640		CLASS DNV	SCALE -	
DRAWING NO. SB-		SUNBO UNITECH CO., LTD.		