
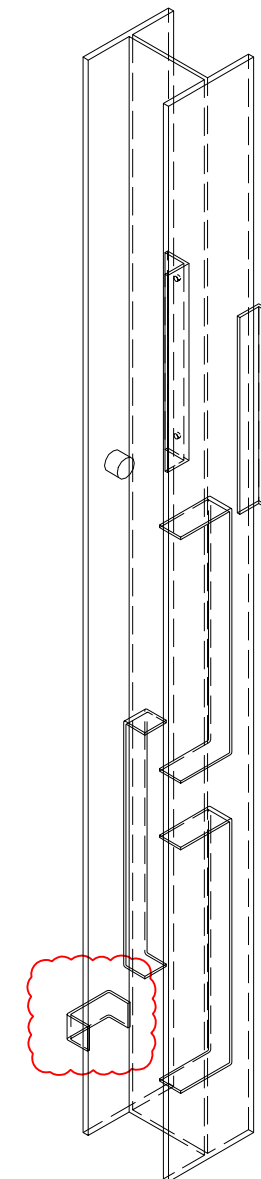
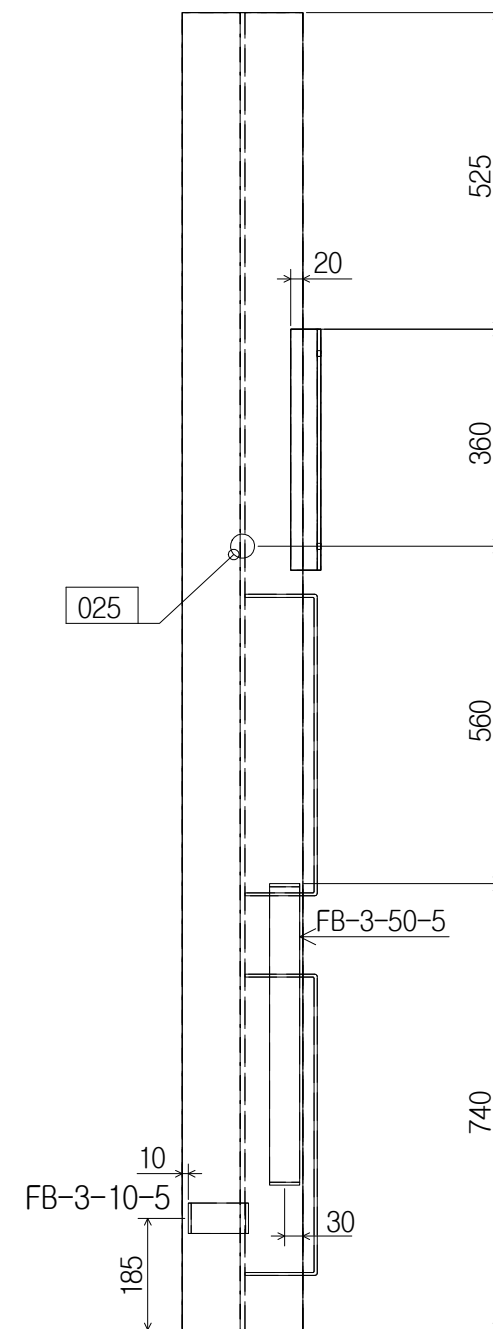
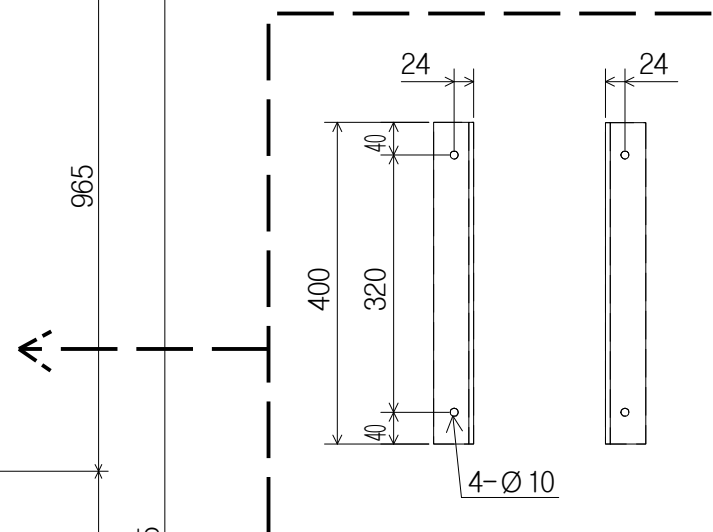
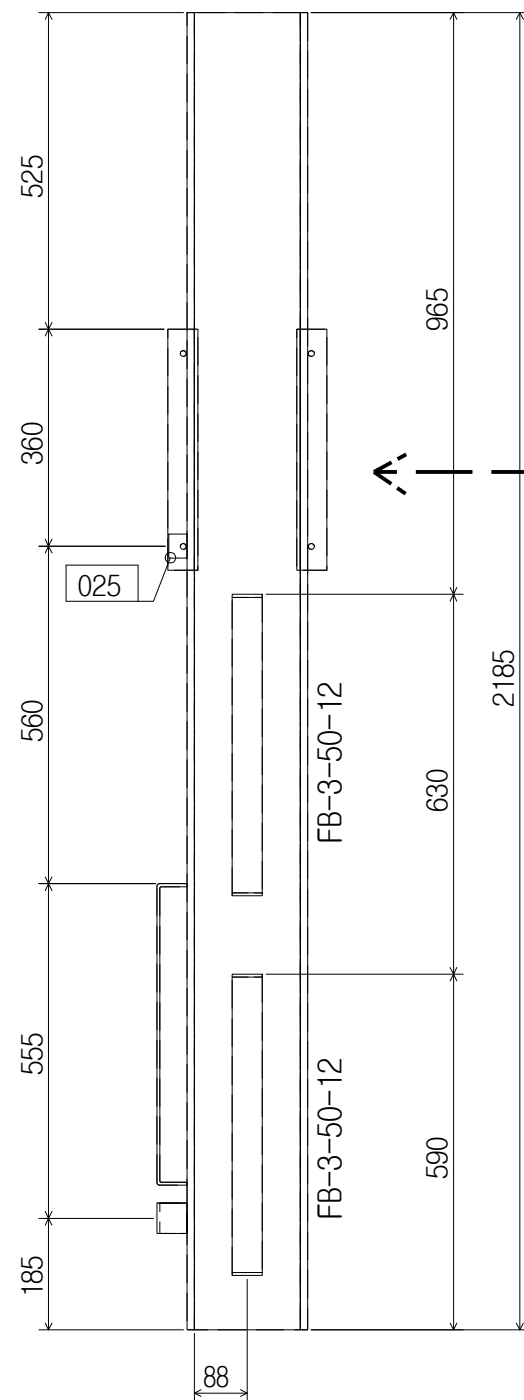


PIL-06

R6_FB 삭제/추가

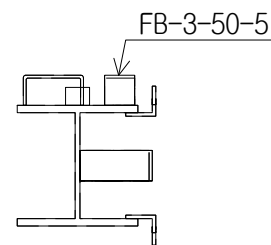

ALL NON MARKED SLOT HOLE Ø8X20L
 ALL NON MARKED H-BEAMS H200x200
 ALL NON MARKED U-BEAMS CH100x50
 ALL NON MARKED L-BEAMS L50x50
 ALL NON MARKED STIFFENER FOR H200x200

001
 006
 008
 009

APPROVED 김갑진	PROJECT NO. D2585 3LP165		
CHECKED 김영광	NAME OF DRAWING		
DRAWN 강지혜	STEEL STRUCTURE SUPPORTS & PILARS		
TEL. NO. +82-51-260-5640			
DRAWING NO. SB-	CLASS DNV	SCALE -	☉
SUNBO UNITECH CO., LTD.			