


제작 참고용 도면

NOTES:
1 MASKING AREA IS FOR REFERENCE. DETAIL DIMENSIONS FOR MASKING TO BE DETERMINED BY YARD.

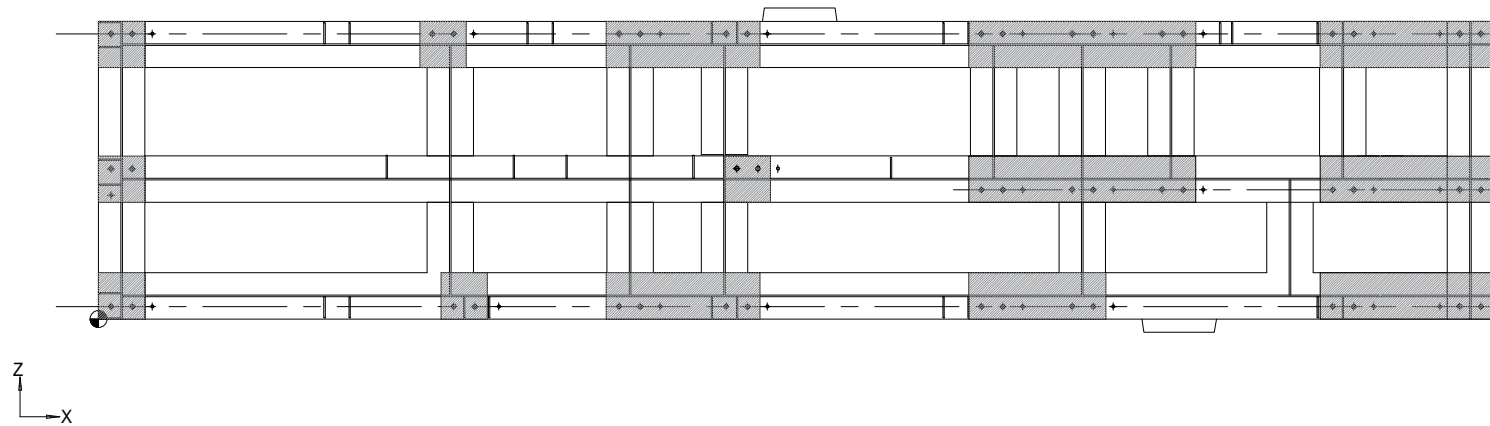

 : CHOCKFAST SURFACE AREA
(PAINTING NOT TO BE APPLIED ON FABRICATION STAGE)



00	2026-01-21	SUBMITTED FOR INFORMATION		SJH			
REV	DATE	DESCRIPTION		DRWN	CHKD	APPD	APPD



TITLE
FABRICATION & ASSEMBLY DETAIL DRAWING
FOR LPG RELIQUEFACTION SKID
BASE FRAME HOLE & MASKING PLAN

3531 / 3532

PROJECT NUMBER