

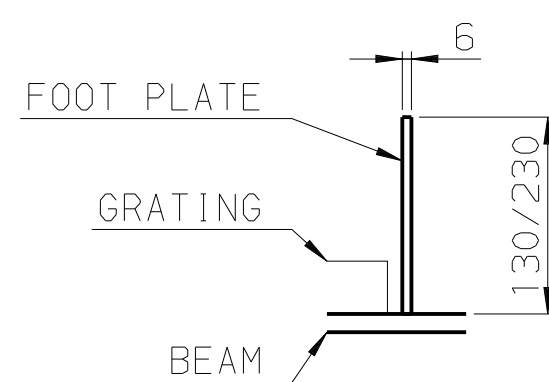
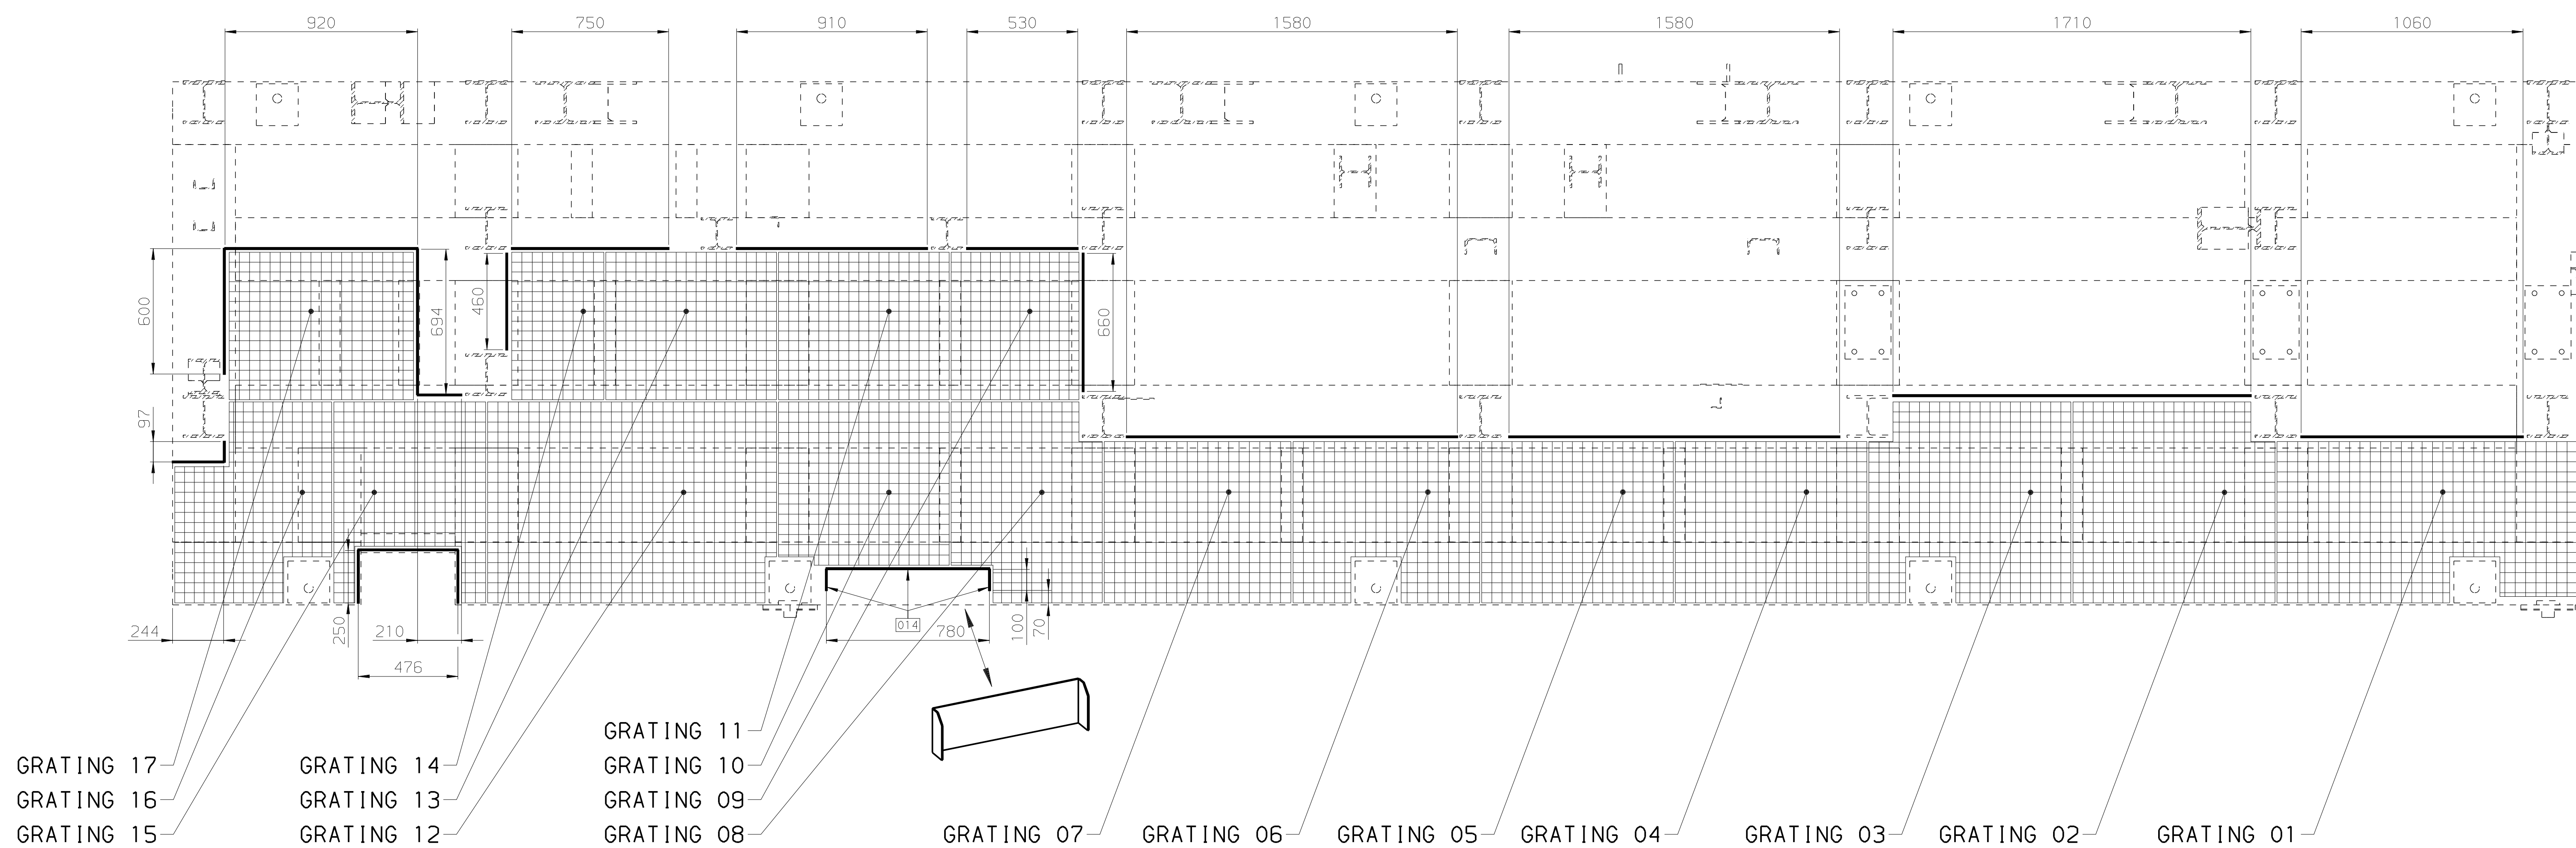


TYPICAL FOR
POS 001 AND 014 FOOT PLATE
(SCALE 1:5)

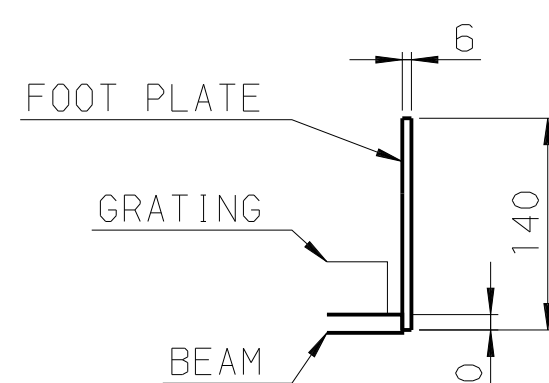

TYPICAL FOR
POS 002 FOOT PLATE
(SCALE 1:5)

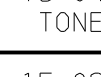

No. of revision	(a)	TONELLI, M	19-07-2022	(b)	TONELLI, M	20-12-2022	(c)	TONELLI, M	21-04-2023	(d)	TONELLI, M	19-09-2023
	Name	Date	Name	Date	Name	Date	Name	Date	Name	Date		
Sup. points list		Design group										
Replaced by		Subst. for				Orig. scale		1:15				
SLP250V-5A		STEEL STRUCTURE L2 RAILING AND GRATING M4Y-G10 - NON-LUBE COMP. ITEM NO.: C-001						Drawn:		19-04-2022		
L-0184								Verified:		15-09-2023		
								Standards conform:		SABOGAL		
CAD-Drawing		Part-No.		Bar - Code								
 Burckhardt Compression		E		0-125.619.962						2 nd d		

This drawing is entrusted to the recipient personally, but the copyright remains with us. It must not be copied, reproduced or in any way communicated or made accessible to third parties without our written consent.

Similar Dwg.

Machining regulations see Drawing Standards.