
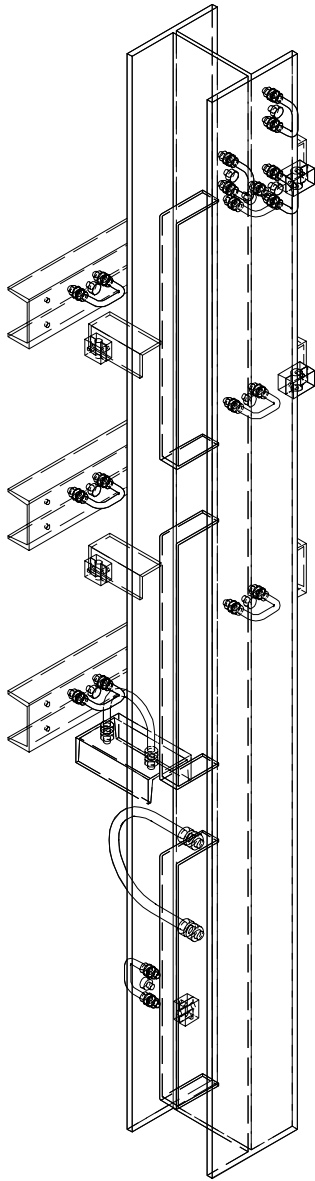
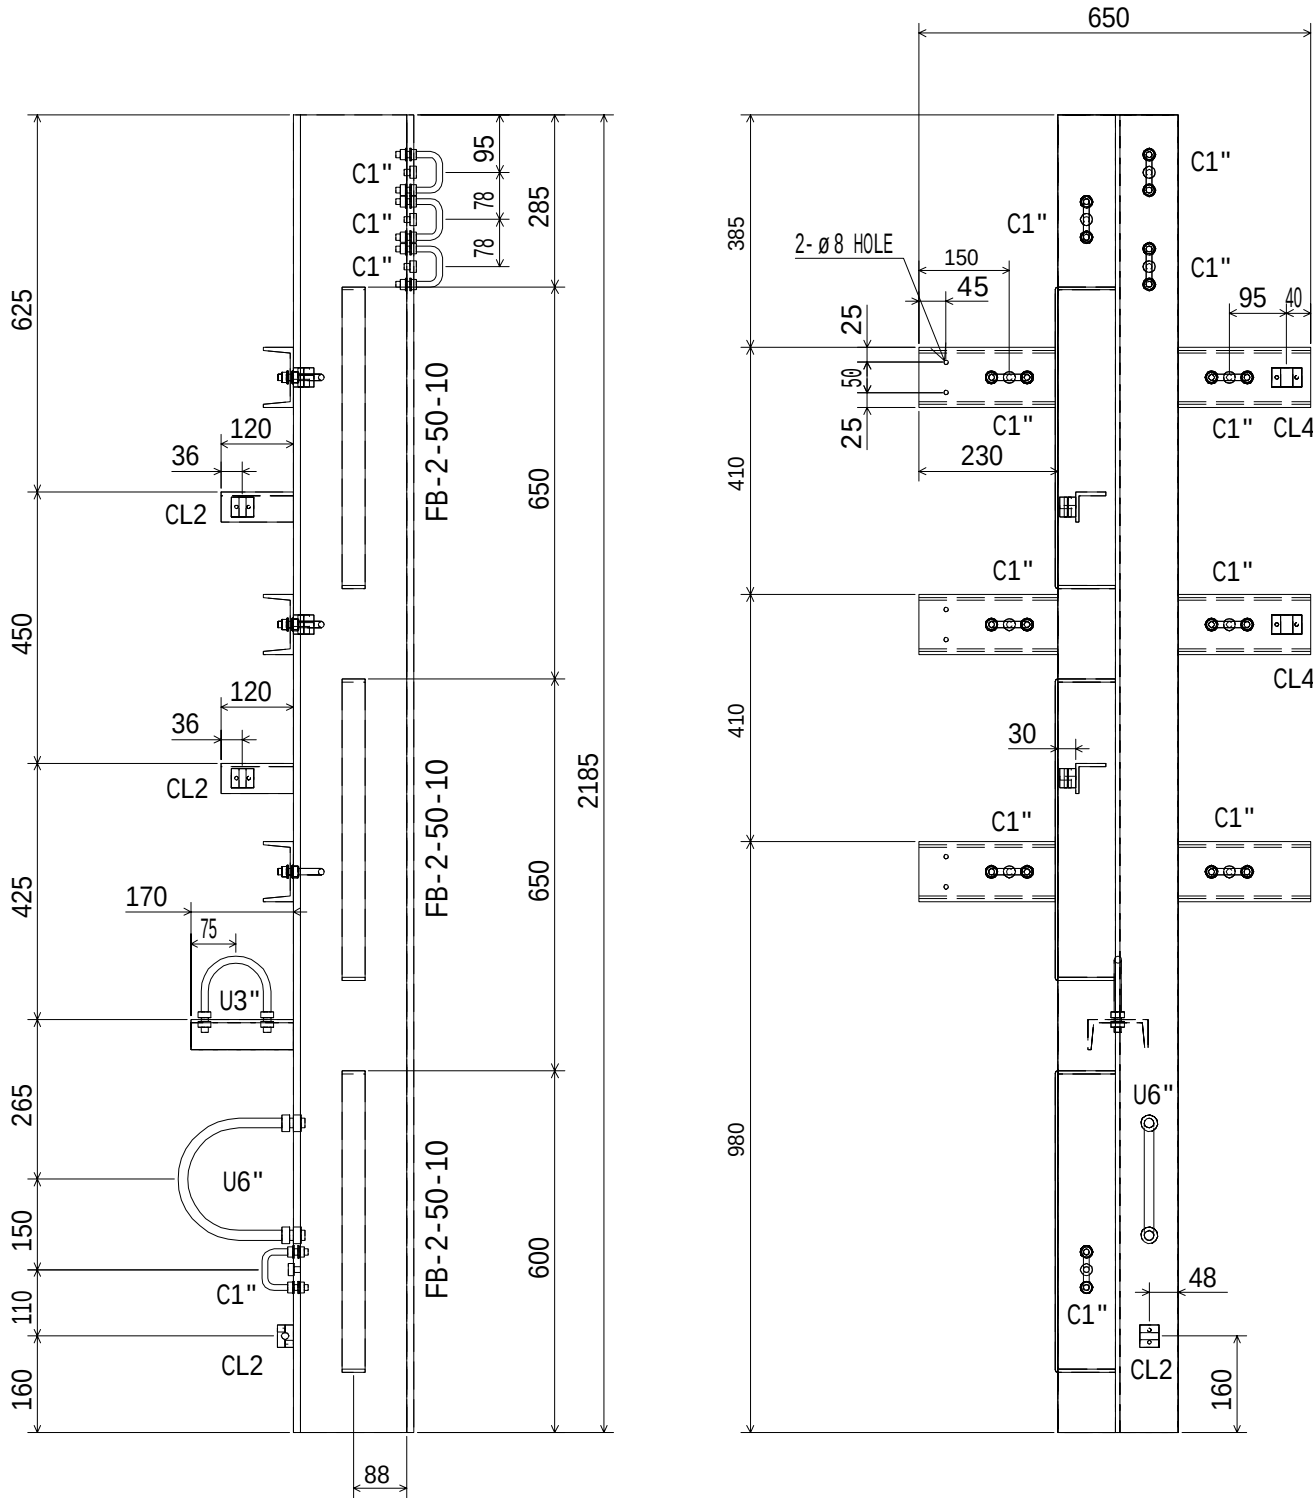


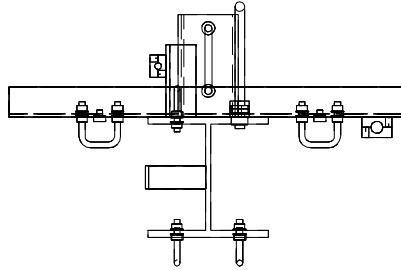

ALL NON MARKED SLOT HOLE Ø8X20L
ALL NON MARKED H-BEAMS H200x200
ALL NON MARKED U-BEAMS CH100x50
ALL NON MARKED L-BEAMS L50x50
ALL NON MARKED STIFFENER FOR H200x200

APPROVED 김 감 진	PROJECT NO. D2585 3LP165		
CHECKED 김 영 광	NAME OF DRAWING STEEL STRUCTURE SUPPORTS & PILARS		
DRAWN 강 지 해			
TEL. NO. +82-51-260-5640			
DRAWING NO. SB-	CLASS DNV	SCALE .	☉
SUNBO UNITECH CO., LTD.			