
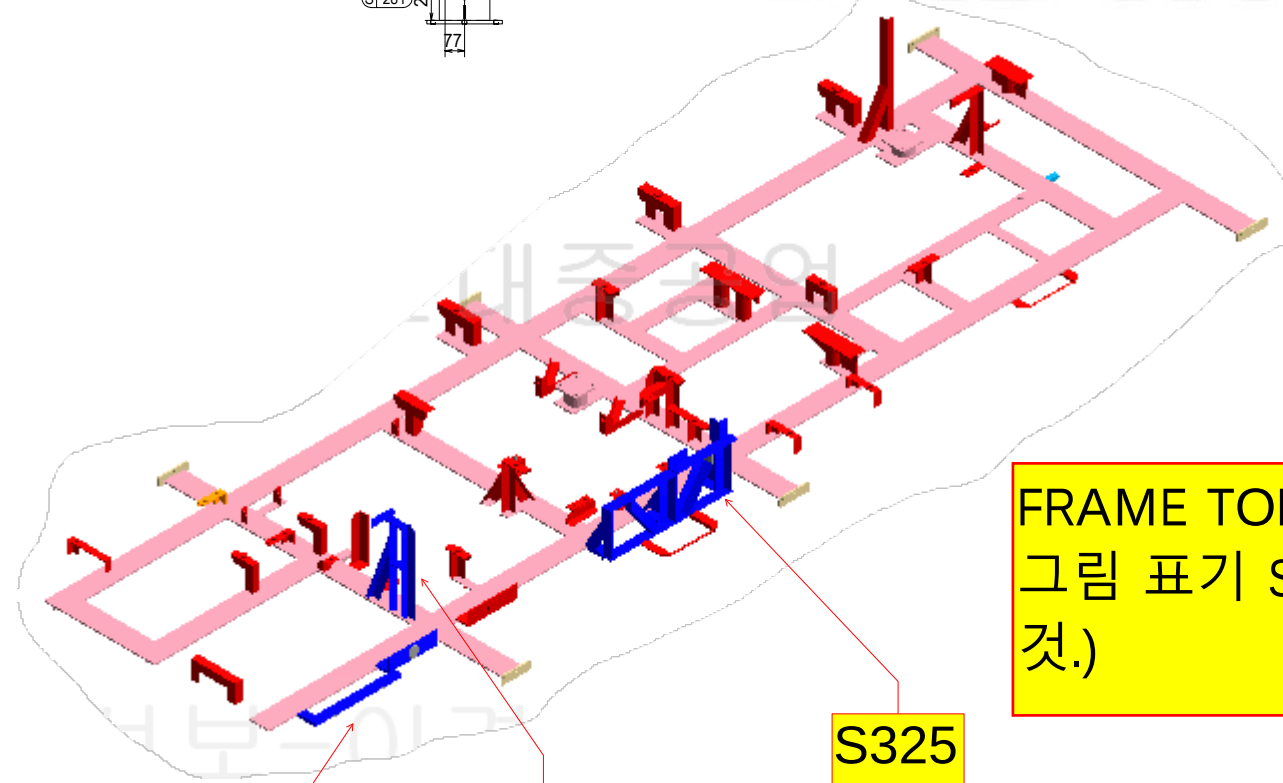


SUPPORT 취부도 (3 / 14)

PLAN VIEW "A"

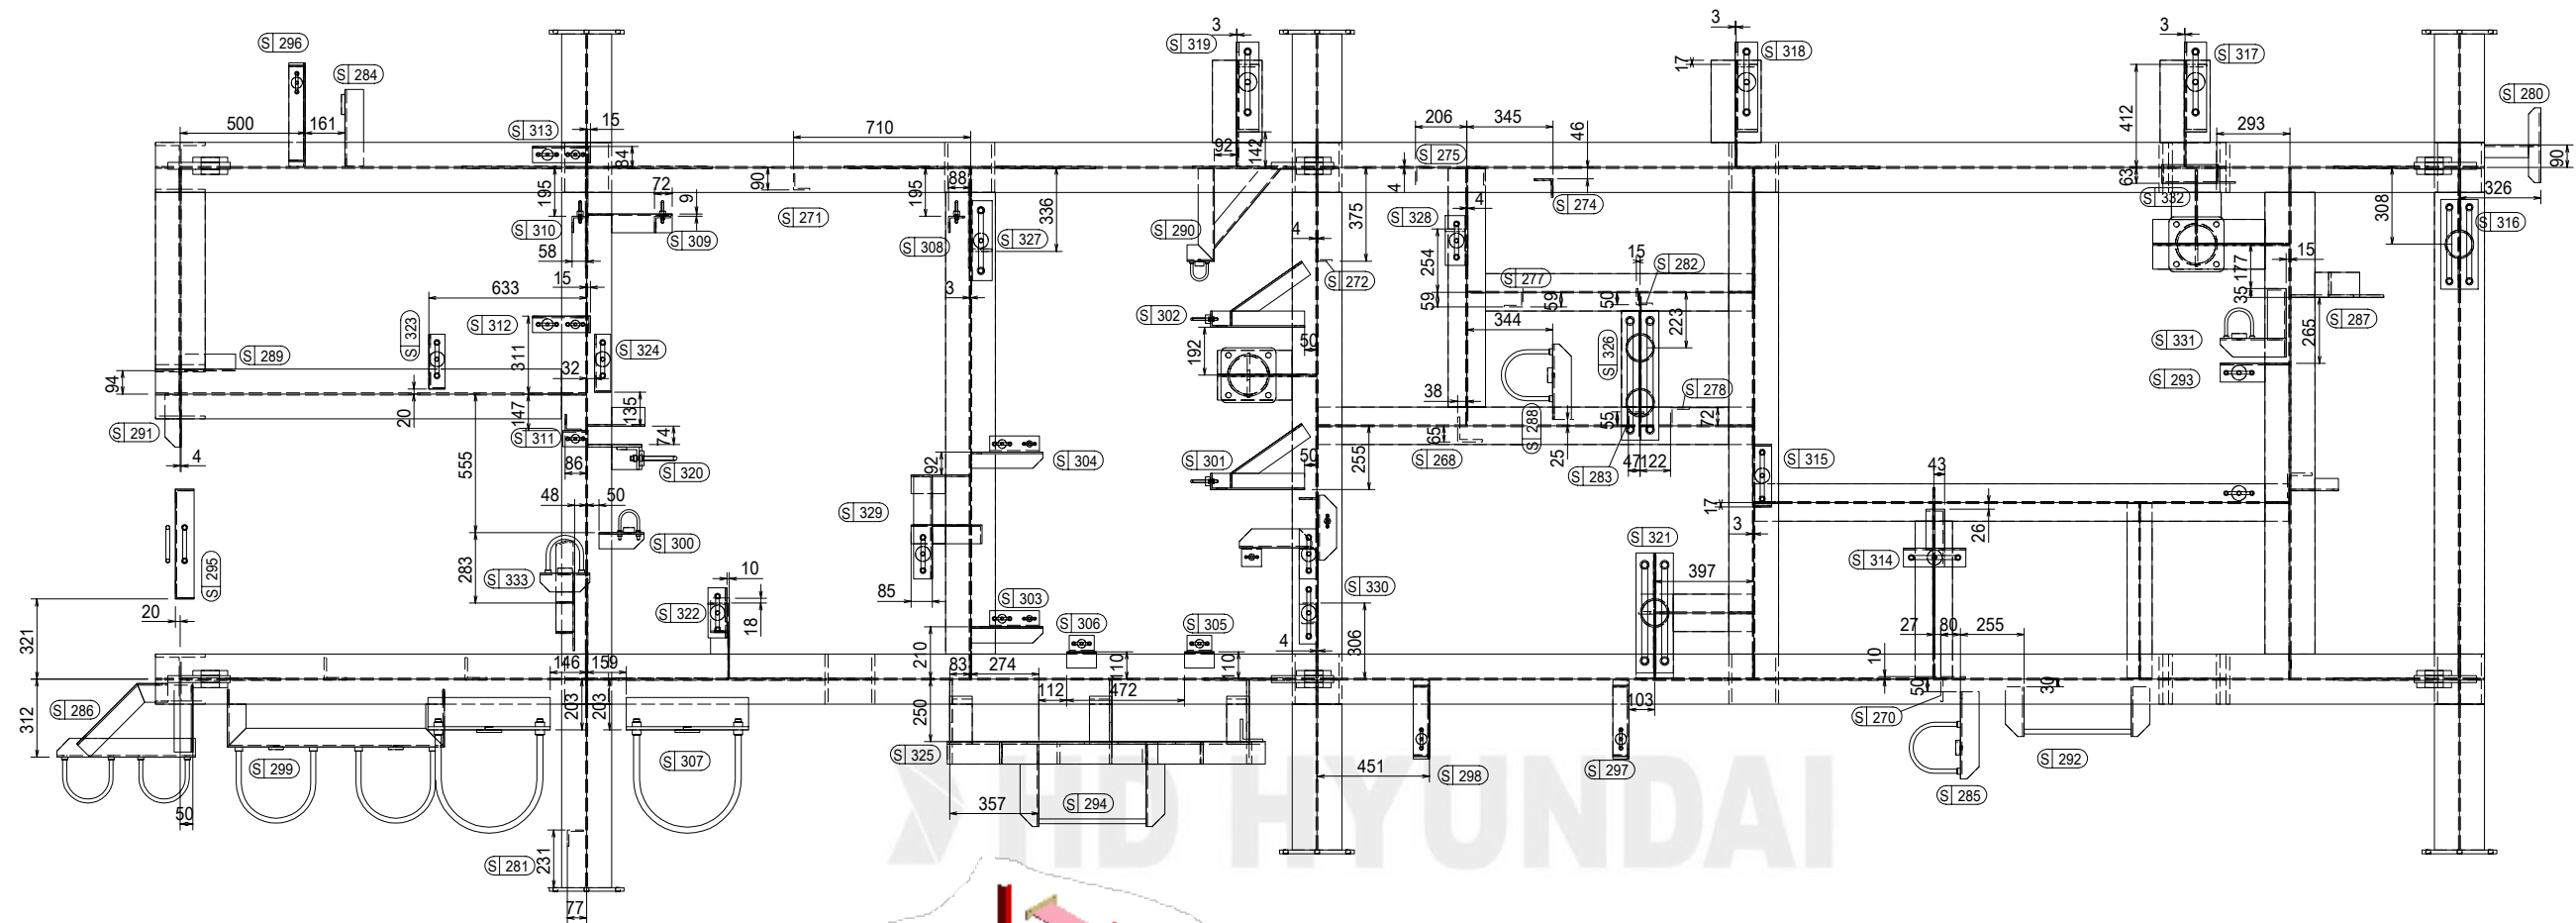

FRAME TOP FRAME TOP면에 설치되는 SUPP중
그림 표기 SUPP제외 전량 T/W(반드시 정위치할
것.)

S325
제외

S333
제외

S299
제외