

# PLAN HISTORY

| DATE       | REV. NO | PROJ. NO. | DESCRIPTION                     | WEIGHT(Kg) |     |     |     | TOTAL PAGES | DWN | CHK | APP |
|------------|---------|-----------|---------------------------------|------------|-----|-----|-----|-------------|-----|-----|-----|
|            |         |           |                                 | REV        | ADD | CAN | SUM |             |     |     |     |
| 2025.06.18 | 0       | D2581/2   | D2581/2 5LP250V 호선용으로 출도함(2SET) |            |     |     |     |             | 김갑진 | -   | 임우택 |
| 2025.09.26 |         | D2602     | D2602 5LP250V 호선용으로 출도함         |            |     |     |     |             | 진호련 | 김갑진 | 인진태 |
| 2026.01.09 |         | D2603     | D2603 5LP250V 호선용으로 출도함         |            |     |     |     |             | 진호련 | 김갑진 | 인진태 |
|            |         |           |                                 |            |     |     |     |             |     |     |     |
|            |         |           |                                 |            |     |     |     |             |     |     |     |
|            |         |           |                                 |            |     |     |     |             |     |     |     |
|            |         |           |                                 |            |     |     |     |             |     |     |     |

\* 총중량(KG/SHIP) : A : 485kg, B:453kg

## NOTE

- 의문사항은 임의 제작치 마시고 설계부로 문의 후 작업 바랍니다.
- 한 호선당 본 도면으로 2SET 제작 바랍니다.
- 본 도면의 H/RAIL만 제작 바랍니다.
- 제작 수량에 주의바라며, 호선당 A/B SET 구분하여 용접타입은 설치 입고(BOLT'G TYPE LOOSE 입고)
- PAINT SPEC. : BCX\_1 (FINAL COLOR : RAL1018)

# HAND RAIL

## CAUTION

THIS DRAWING OR DOCUMENT IS THE PROPERTY OF SUNBO INDUSTRIES CO., LTD.  
AND IT MUST NOT BE PARTIALLY OR WHOLLY COPIED OR USED FOR ANY OTHER PURPOSE  
WITHOUT PRIOR WRITTEN PERMISSION OF SUNBO INDUSTRIES CO., LTD.

|         |  |   |  |                                                |  |                                                                                     |          |              |       |
|---------|--|---|--|------------------------------------------------|--|-------------------------------------------------------------------------------------|----------|--------------|-------|
| 도면배포처   |  | SEC NO.   |  | MACH. OUTFITTING DESIGN DEP'T<br>DESIGN 5 TEAM |  | SHIP<br>TYPE                                                                        | 174K LNG |              |       |
| 구매부 ▼   |  | TEL. NO.   |  | SHIP NO.                                       |  | SHIP<br>NAME                                                                        |          |              |       |
| 생산부 ▼   |  | 051-260-5638   |  | D2581/2/2602/2603 5LP250V                      |  |                                                                                     |          |              |       |
| QC ▼    |  | DATE<br>2025.09.26                                                                                                   |  | APPROVED<br>인진태                                |  | NAME OF DRAWING<br><b>HAND RAIL DWG FOR<br/>HP COMPRESSOR<br/>PACKAGE (5LP250V)</b> |          |              |       |
|         |  |   |  |                                                |  |                                                                                     |          |              |       |
|         |  |   |  | CHECKED<br>김갑진                                 |  | DRAWING NO.                                                                         |          |              | SCALE |
|         |  |   |  | DRAWN<br>진호련                                   |  | SB - 0                                                                              |          |              | NONE  |
|         |  |  <b>SUNBO INDUSTRIES CO., LTD</b> |  |                                                |  | CLASS                                                                               | UNIT     | CONSOLIDATED |       |
|         |  |   |  |                                                |  | 0                                                                                   | mm       |              |       |
|         |  |   |  |                                                |  |                                                                                     |          |              |       |
| TOTAL 3 |  |   |  |                                                |  |                                                                                     |          |              |       |



**SUNBO INDUSTRIES CO., LTD**

도면 및 중량 LIST

| DWG NO                                    | PART NO                    | SET당<br>제작수량   | 호선당<br>제작수량    | 중량(kg)        | 비고         |
|-------------------------------------------|----------------------------|----------------|----------------|---------------|------------|
| 125.619.962<br>(M2T)                      | RAILING 1(M2T-1)           | 2EA            | 4EA            | 148           |            |
|                                           | RAILING 2(M2T-2)           | 1EA            | 2EA            |               |            |
|                                           | RAILING 3(M2T-3)           | 1EA            | 2EA            |               |            |
|                                           | RAILING 4(M2T-4)           | 1EA            | 2EA            |               |            |
|                                           | RAILING 5(M2T-5)           | 1EA            | 2EA            |               |            |
|                                           | RAILING 6(M2T-6)           | 1EA            | 2EA            |               |            |
|                                           | RAILING 7(M2T-7)           | 1EA            | 2EA            |               |            |
| 125.619.977<br>(M3T)                      | RAILING 1(M3T-1)           | 1EA            | 2EA            | 176           |            |
|                                           | RAILING 2(M3T-2)           | 1EA            | 2EA            |               |            |
|                                           | RAILING 3(M3T-3)           | 1EA            | 2EA            |               |            |
|                                           | RAILING 4(M3T-4)           | 1EA            | 2EA            |               |            |
|                                           | RAILING 5(M3T-5)           | 1EA            | 2EA            |               |            |
|                                           | RAILING 6(M3T-6)           | 1EA            | 2EA            |               |            |
|                                           | RAILING 7(M3T-7)           | 1EA            | 2EA            |               |            |
|                                           | RAILING 8(M3T-8)           | 1EA            | 2EA            |               |            |
| <del>125.619.980<br/>(BRIDGE MOTOR)</del> | <del>RAILING(MOT-1)</del>  | <del>1EA</del> | <del>2EA</del> | <del>29</del> | 삭제(D2537~) |
| <del>125.619.981<br/>(BRIDGE PUMP)</del>  | <del>RAILING(PUMP-1)</del> | <del>1EA</del> | <del>2EA</del> | <del>29</del> | 삭제(D2537~) |
| <del>125.619.982<br/>(BRIDGE COMP)</del>  | <del>RAILING(COMP-1)</del> | <del>2EA</del> | <del>4EA</del> | <del>62</del> | 삭제(D2537~) |
| 125.619.985                               | LOOSE-1                    | 1EA            | 2EA            | 9             |            |
|                                           | LOOSE-2                    | 2EA            | 4EA            |               |            |
| 125.622.142                               | LOOSE-3                    |                | 1EA            | 32            | 호선당 1EA 제작 |
| A SET 중량                                  |                            |                |                | 365           |            |
| B SET 중량                                  |                            |                |                | 333           | LOOSE-3 제외 |

|   |   |                                              |          |
|---|---|----------------------------------------------|----------|
|  <b>Burckhardt<br/>Compression</b> | <b>Painting Spezifikation</b><br><b>Für C-Stahl, Grau-, Sphäroguss <math>\leq +120^{\circ}\text{C}</math></b><br><i>Painting specification for carbon steel, grey-, nodular cast</i><br><b>C5-M (ISO 12944-5)</b> | (TSP)<br><b>BCX_PAINT_</b><br><b>SYST_01</b> | Revision |
|---|---|----------------------------------------------|----------|

## 6. Farbaufbau / Coating system

Burckhardt Compression Farbaufbau  
auf Kohlenstoffstahl, Grau- und Sphäroguss  
für Betriebstemperaturen  $\leq +120^{\circ}\text{C}$

*Burckhardt Compression painting system  
for carbon steel, cast-iron and nodular cast  
for service temperatures  $\leq +120^{\circ}\text{C}$*

### Grundierung / Primer

2-K Epoxy – Zinkstaubgrundierung

*2-Pack Epoxy – zinc rich primer*

**INTERZINC 52**

TDO 2039235

### Zwischenbeschichtung / Interlayer

2-K Epoxy / Polyamid Glimmerfarbe

*2-Pack Epoxy / Polyamide Mio paint*

**INTERGARD 475 HS**

TDO 2039236

### Decklack / Top coat


2-K Polyurethan - Acrylat

*2-Pack Acrylic - Polyurethane*

**INTERTHANE 990**

TDO 2039237



FINAL COLOR : RAL1018(YELLOW)

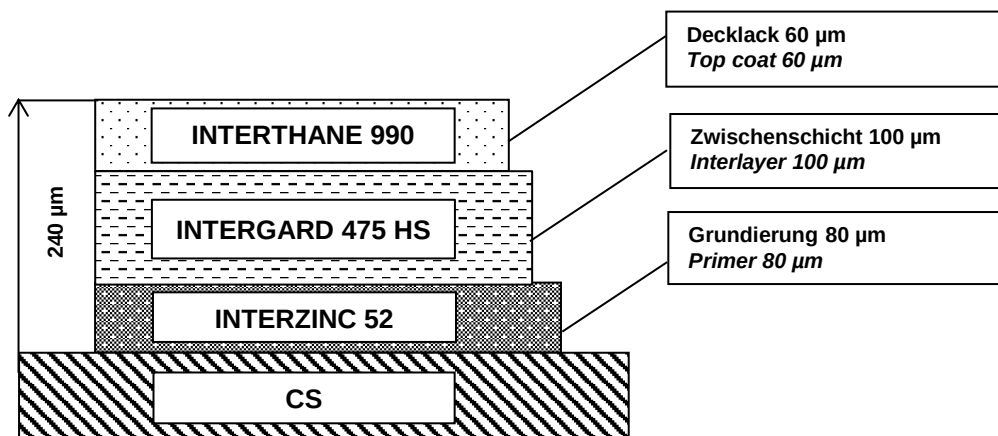

Produktspezifische Details entnehmen Sie  
bitte den technischen Merkblättern (TDO)

*For product details please refer to  
manufacturer data sheets (TDO)*

|                         | Rev. | Dat.       | Sig.       | Ersatz für<br>Replacement for | Seite 3 von 5<br>Page 3 of 5 |  |
|-------------------------|------|------------|------------|-------------------------------|------------------------------|--|
| Erstellt / Prepared     |      | 28.12.2021 | RIEDENER_T | Revision                      |                              |  |
| Überprüft / Reviewed    |      | 03.01.2022 | BERNHARD_M | vom / date                    |                              |  |
| Freigabe / Approval DVS |      | 03.01.2022 | RIEDENER_T |                               |                              |  |

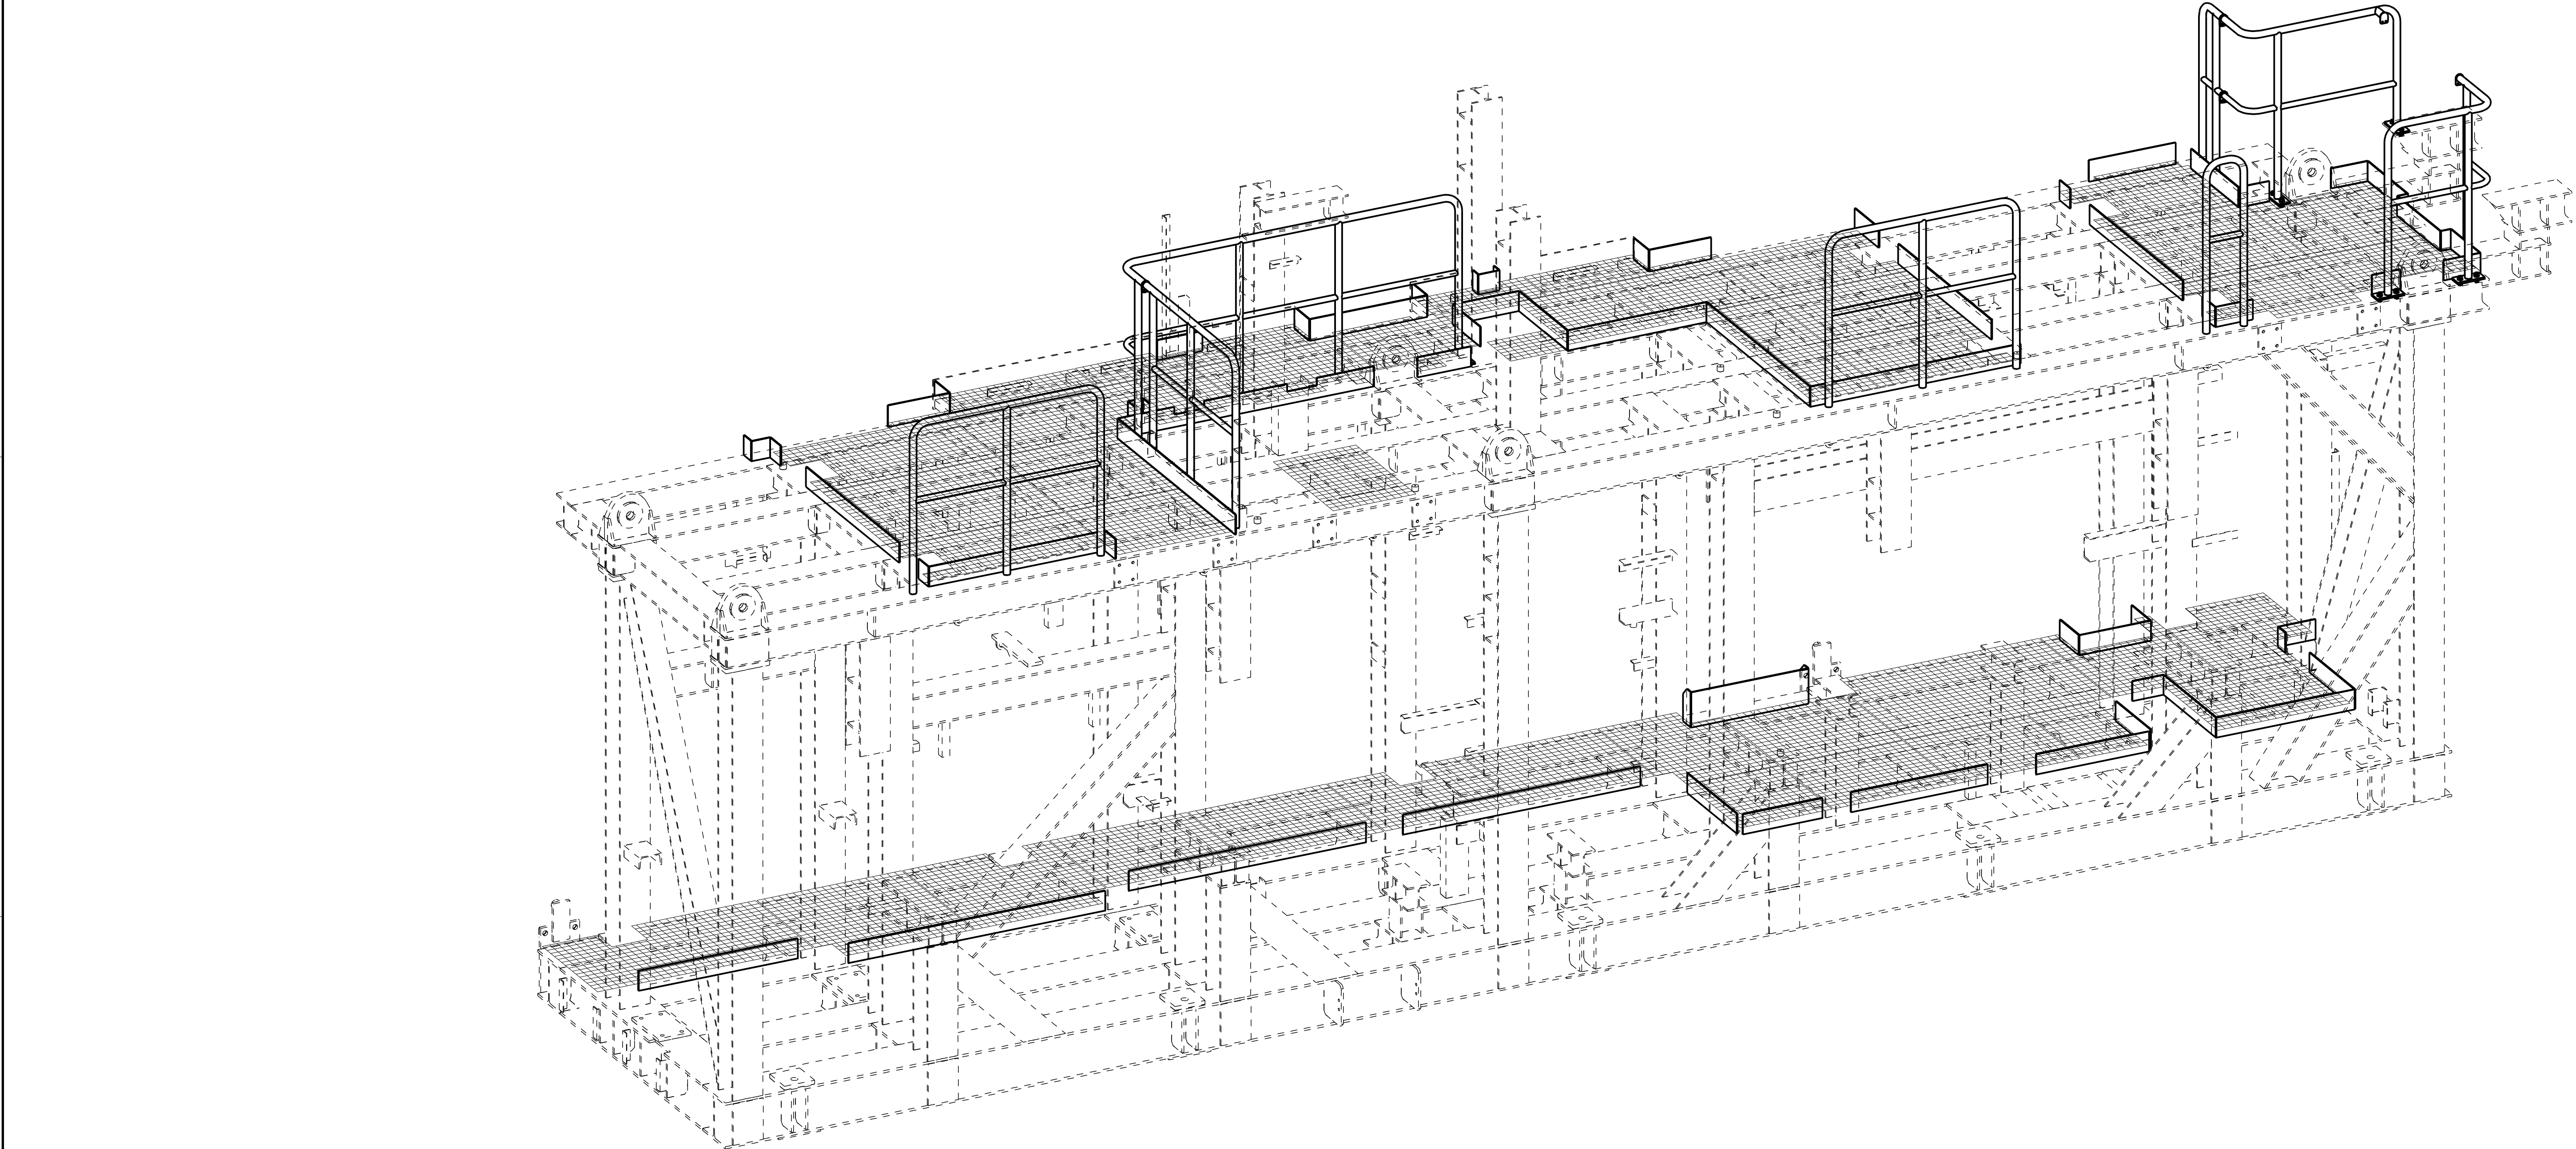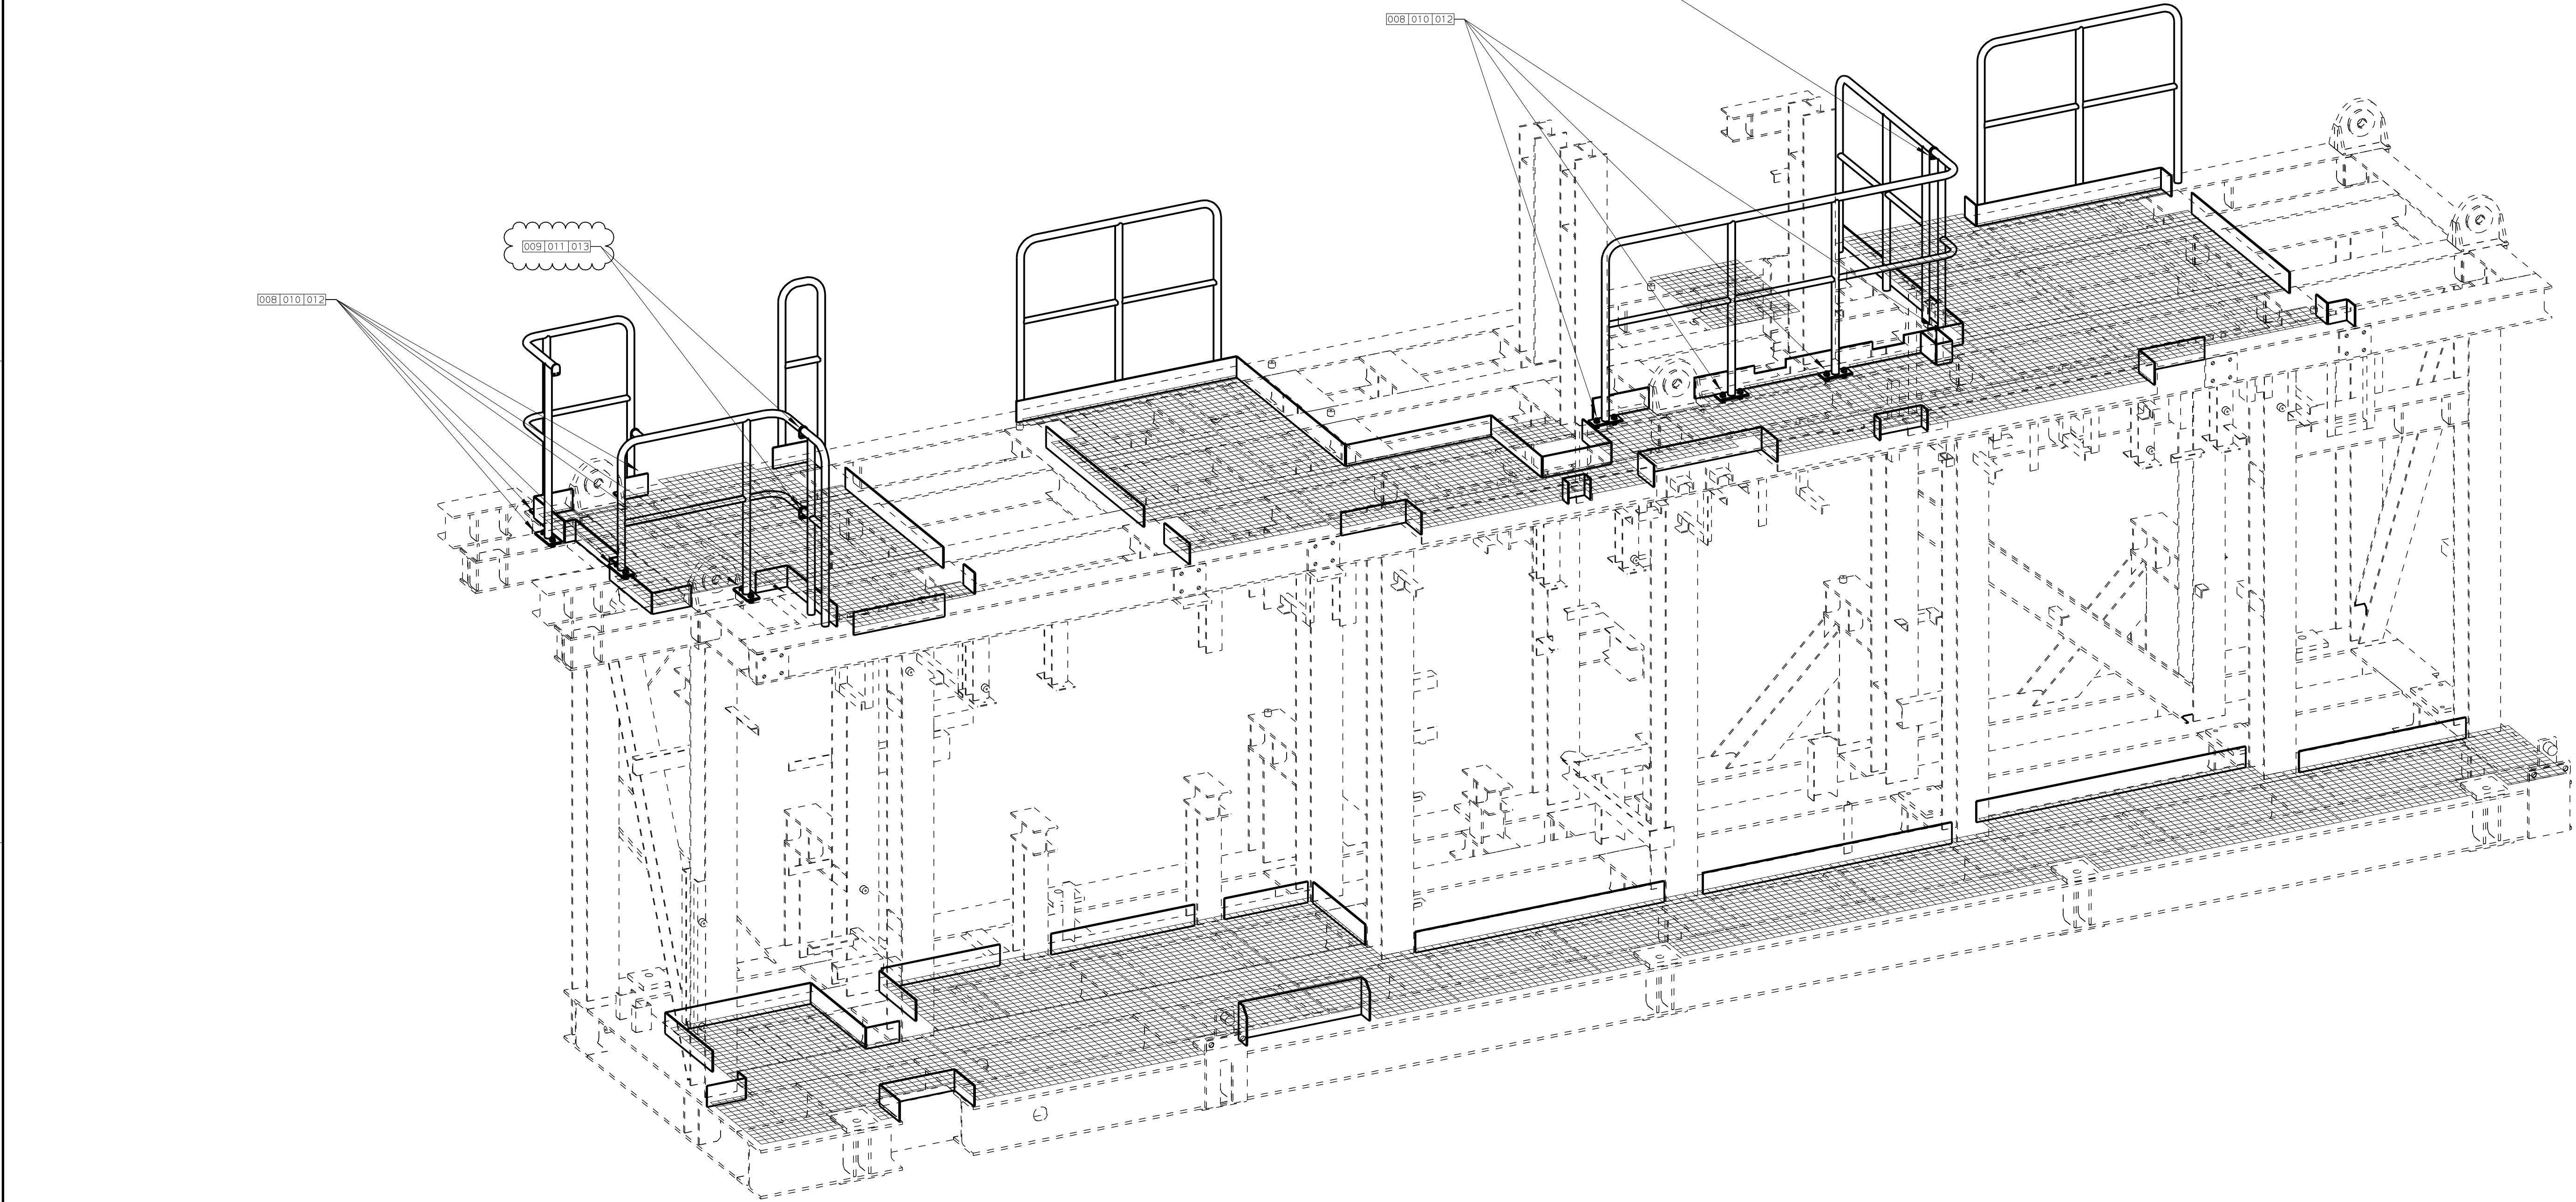

This drawing is attributed to the recipient personally, but the copyright remains with us. It must not be copied, reproduced or in any way communicated or made accessible to third parties without our written consent.

3 in 1 or 2 in 1  
According to regulations see Drawing Standards.



| Execution Code Number |     | Pos. No.                | Designation          | Source of Supply |     | Letter |
|-----------------------|-----|-------------------------|----------------------|------------------|-----|--------|
|                       |     |                         | Material and Remarks | Approximate kg   |     |        |
| Number: OFF           |     |                         |                      |                  |     |        |
| 32.5m                 | 001 | FOOT PLATE 6x130        |                      | /                | /   | /      |
|                       |     | 55400                   |                      | /                | 193 | /      |
| 3.5m                  | 002 | FOOT PLATE 6x140        |                      | /                | /   | /      |
|                       |     | 55400                   |                      | /                | 19  | /      |
| 3.5m                  | 003 | PIPE 1 1/4" (SCHED. 10) | ASME B36.10M         | /                | /   | /      |
|                       |     | A106 GR B               |                      | /                | 117 | /      |
| 9.5m                  | 004 | PIPE 1" (SCHED. 10)     | ASME B36.10M         | /                | /   | /      |
|                       |     | A106 GR B               |                      | /                | 30  | /      |
| 5m                    | 005 | GRATING (THK 25)        |                      | /                | /   | /      |
|                       |     | /                       |                      | /                | /   | /      |
| 10                    | 006 | PLATE 180x80x10         |                      | /                | /   | /      |
|                       |     | 55400                   |                      | /                | 1   | /      |
| 8                     | 007 | PLATE 70x50x5           |                      | /                | /   | /      |
|                       |     | 55400                   |                      | /                | /   | /      |
| 20                    | 008 | HEX. HEAD BOLT M16x45   |                      | /                | /   | /      |
|                       |     | 8.8                     | DIN EN ISO 4017      | /                | /   | /      |
| 6                     | 009 | HEX. HEAD BOLT M8x25    |                      | /                | /   | /      |
|                       |     | 8.8                     | DIN EN ISO 4017      | /                | /   | /      |
| 20                    | 010 | HEX. NUT M16            |                      | /                | /   | /      |
|                       |     | 8                       | DIN EN ISO 4032      | /                | /   | /      |
| 6                     | 011 | HEX. NUT M8             |                      | /                | /   | /      |
|                       |     | 8                       | DIN EN ISO 4032      | /                | /   | /      |
|                       | 012 | WASHER (M16)            |                      | /                | /   | /      |
|                       |     | /                       | ISO 7089-16-200 HV   | /                | /   | /      |
| 12                    | 013 | WASHER (M8)             |                      | /                | /   | /      |
|                       |     | /                       | ISO 7089-8-200 HV    | /                | /   | /      |
| 14                    | 014 | FOOT PLATE 6x230        |                      | /                | /   | /      |
|                       |     | 55400                   |                      | /                | 10  | /      |
| APPROX WEIGHT         |     |                         |                      | ≈                | 370 | Kg     |

NOTE:  
1) ALL LISTE MATERIAL ARE WITHOUT ALLOWANCE.



|                 |                |                          |                |                                |
|-----------------|----------------|--------------------------|----------------|--------------------------------|
| Rev. / Date     | 1 / 14-04-2022 | 2 / 15-09-2023           | 3 / 15-09-2023 | 4 / 15-09-2023                 |
| TONELLI_M       | TONELLI_M      | TONELLI_M                | TONELLI_M      | TONELLI_M                      |
| Name            | Name           | Name                     | Name           | Name                           |
| Date            | Date           | Date                     | Date           | Date                           |
| Replaced by     |                | Subst. for               |                | Orig. scale 1:20               |
| SLP250V-SA      |                | STEEL STRUCTURE          |                | Drawn: 14-04-2022 TONELLI_M    |
| L-0184          |                | M2 RAILING AND GRATING   |                | Verified: 15-09-2023 SABOGAL_M |
| ASME            |                | LABY-G1 - NON-LUBE COMP. |                | Standards comply               |
| ITEM NO.: C-001 |                |                          |                |                                |
| CAD-Drawing     |                | Part-No.                 | Bar - Code     |                                |
|                 |                | E                        | 0-125.619.962  |                                |
|                 |                |                          | 1 - 4          |                                |

TYPICAL FOR  
POS 001 AND 014 FOOT PLATE  
(SCALE 1:5)

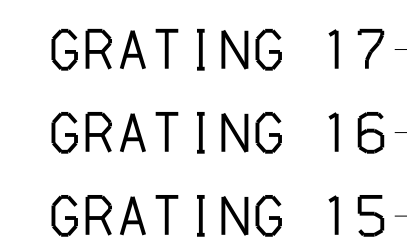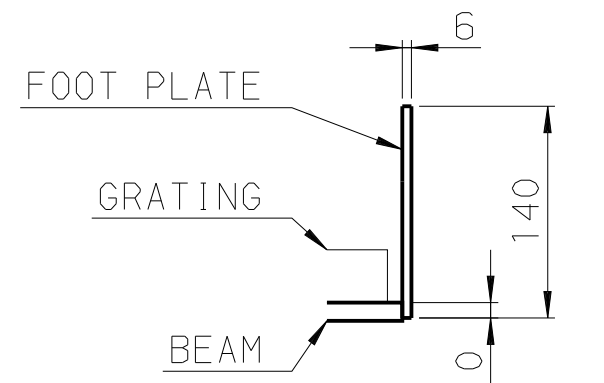

GRATING 14-  
GRATING 13-  
GRATING 12-

GRATING 11-  
GRATING 10-  
GRATING 09-  
GRATING 08-

GRATING 07-

GRATING 06-

GRATING 05-

GRATING 04-







GRATING 03—



GRATING 02—

GRATING 01-

|   |                                                                                       |             |                                                                                                   |            |                                                                                       |             |      |            |                                                                                       |             |      |   |                                                                                       |             |      |            |
|---|---------------------------------------------------------------------------------------|-------------|---------------------------------------------------------------------------------------------------|------------|---------------------------------------------------------------------------------------|-------------|------|------------|---------------------------------------------------------------------------------------|-------------|------|---|---------------------------------------------------------------------------------------|-------------|------|------------|
| Material Code   |  | TONEILLI, M |                                                                                                   | 14-07-2024 |  | TONEILLI, M |      | 20-12-2024 |  | TONEILLI, M |      | 20-09-2024   |  | TONEILLI, M |      | 19-09-2024 |
|   | Name                                                                                  |             | Date                                                                                              |            | Name                                                                                  |             | Date |            | Name                                                                                  |             | Date |   | Name                                                                                  |             | Date |            |
| Sub-parts List   |                                                                                       |             | Design group                                                                                      |            |                                                                                       |             |      |            |                                                                                       |             |      |   |                                                                                       |             |      |            |
| Replaced by   |                                                                                       |             | Subst. for                                                                                        |            |                                                                                       | Orig. scale |      |            | 1:15                                                                                  |             |      |   |                                                                                       |             |      |            |
| 5LP250V-SA<br><br>L-0184<br>ASME                                                                                       |                                                                                       |             | STEEL STRUCTURE<br><br>M2 RAILING AND GRATING<br><br>LABY-G10 - NON-LUBE COMP.<br>ITEM NO.: C-001 |            |                                                                                       |             |      |            |                                                                                       |             |      | Drawn: 19-04-2024<br>TONEILLI, M   |                                                                                       |             |      |            |
|   |                                                                                       |             |                                                                                                   |            |                                                                                       |             |      |            |                                                                                       |             |      | Verified: 15-09-2024<br>SABOGAL, A   |                                                                                       |             |      |            |
|   |                                                                                       |             |                                                                                                   |            |                                                                                       |             |      |            |                                                                                       |             |      | Standards conform:   |                                                                                       |             |      |            |
|   |                                                                                       |             |                                                                                                   |            |                                                                                       |             |      |            |                                                                                       |             |      |   |                                                                                       |             |      |            |
| CAD-Drawing   |                                                                                       |             | Part-No.                                                                                          |            | Bar - Code                                                                            |             |      |            |                                                                                       |             |      |   |                                                                                       |             |      |            |
|  <b>Buckhardt<br/>Compression</b> |                                                                                       |             | E                                                                                                 |            | 0-125.619.962                                                                         |             |      |            | 2 <sup>d</sup> - 4                                                                    |             |      |   |                                                                                       |             |      |            |
|   |                                                                                       |             |                                                                                                   |            |                                                                                       |             |      |            |                                                                                       |             |      |   |                                                                                       |             |      |            |

### RAILING 4

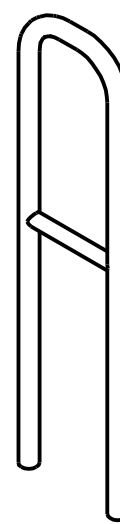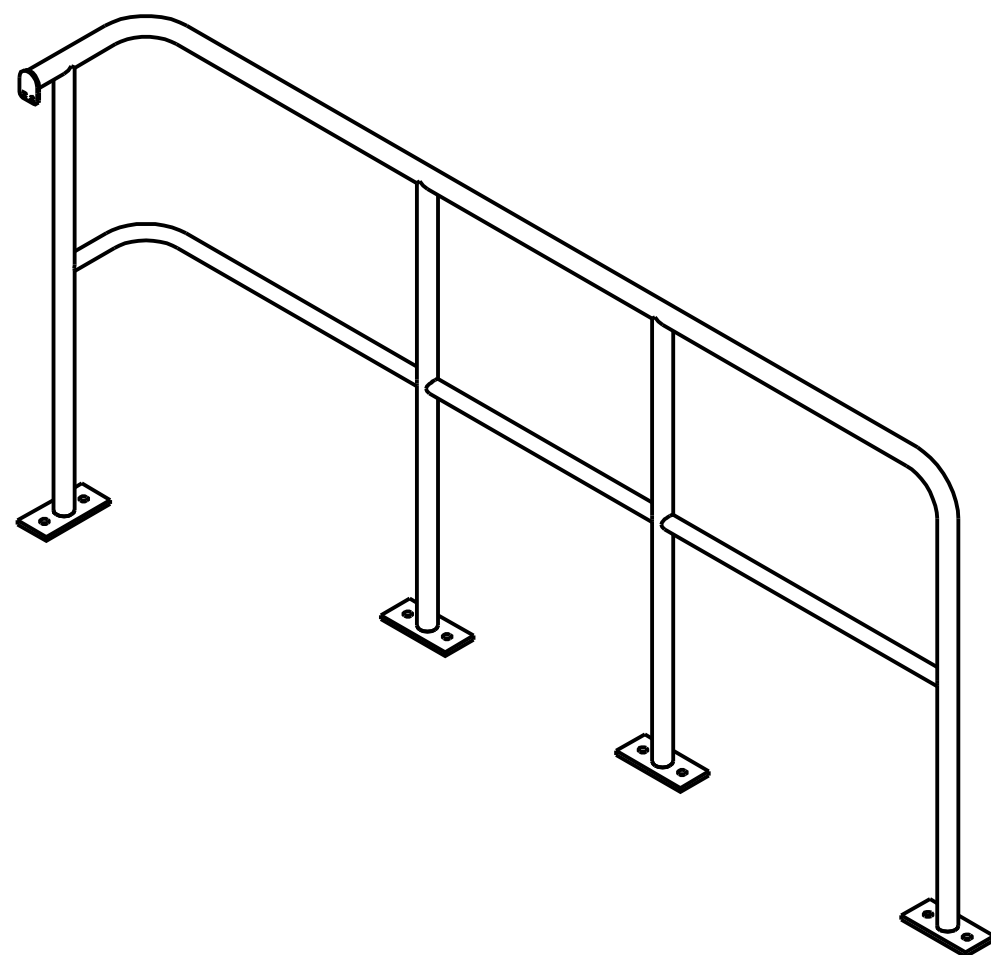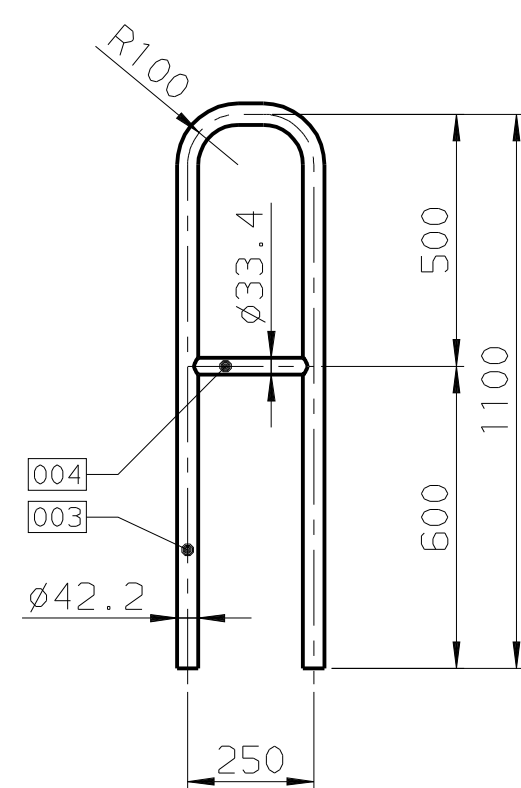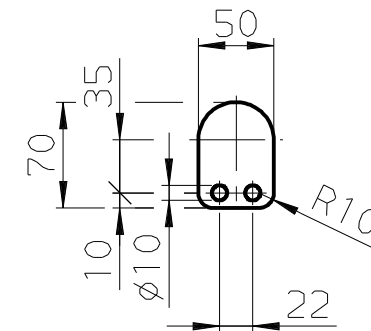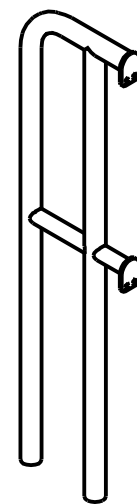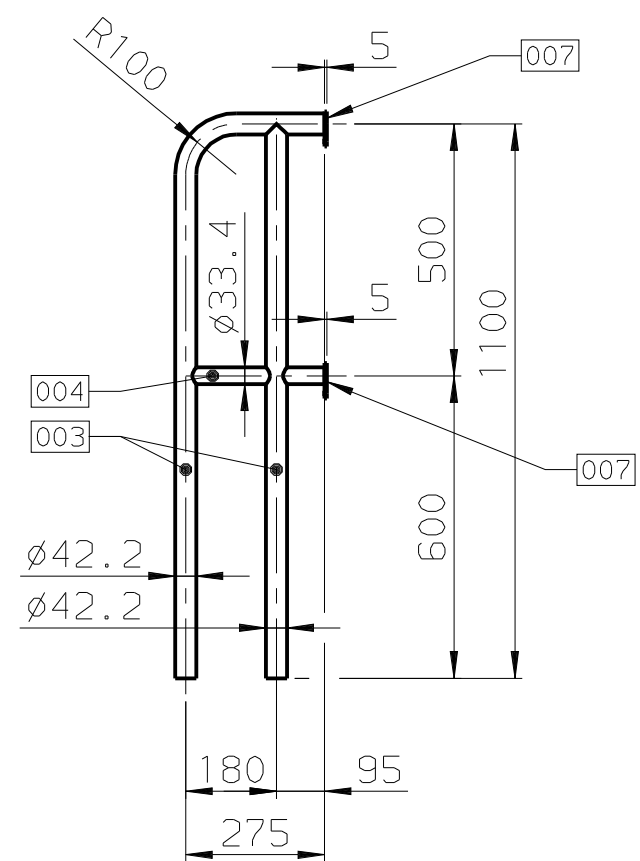RAILING 7
**Burckhardt  
Compression**

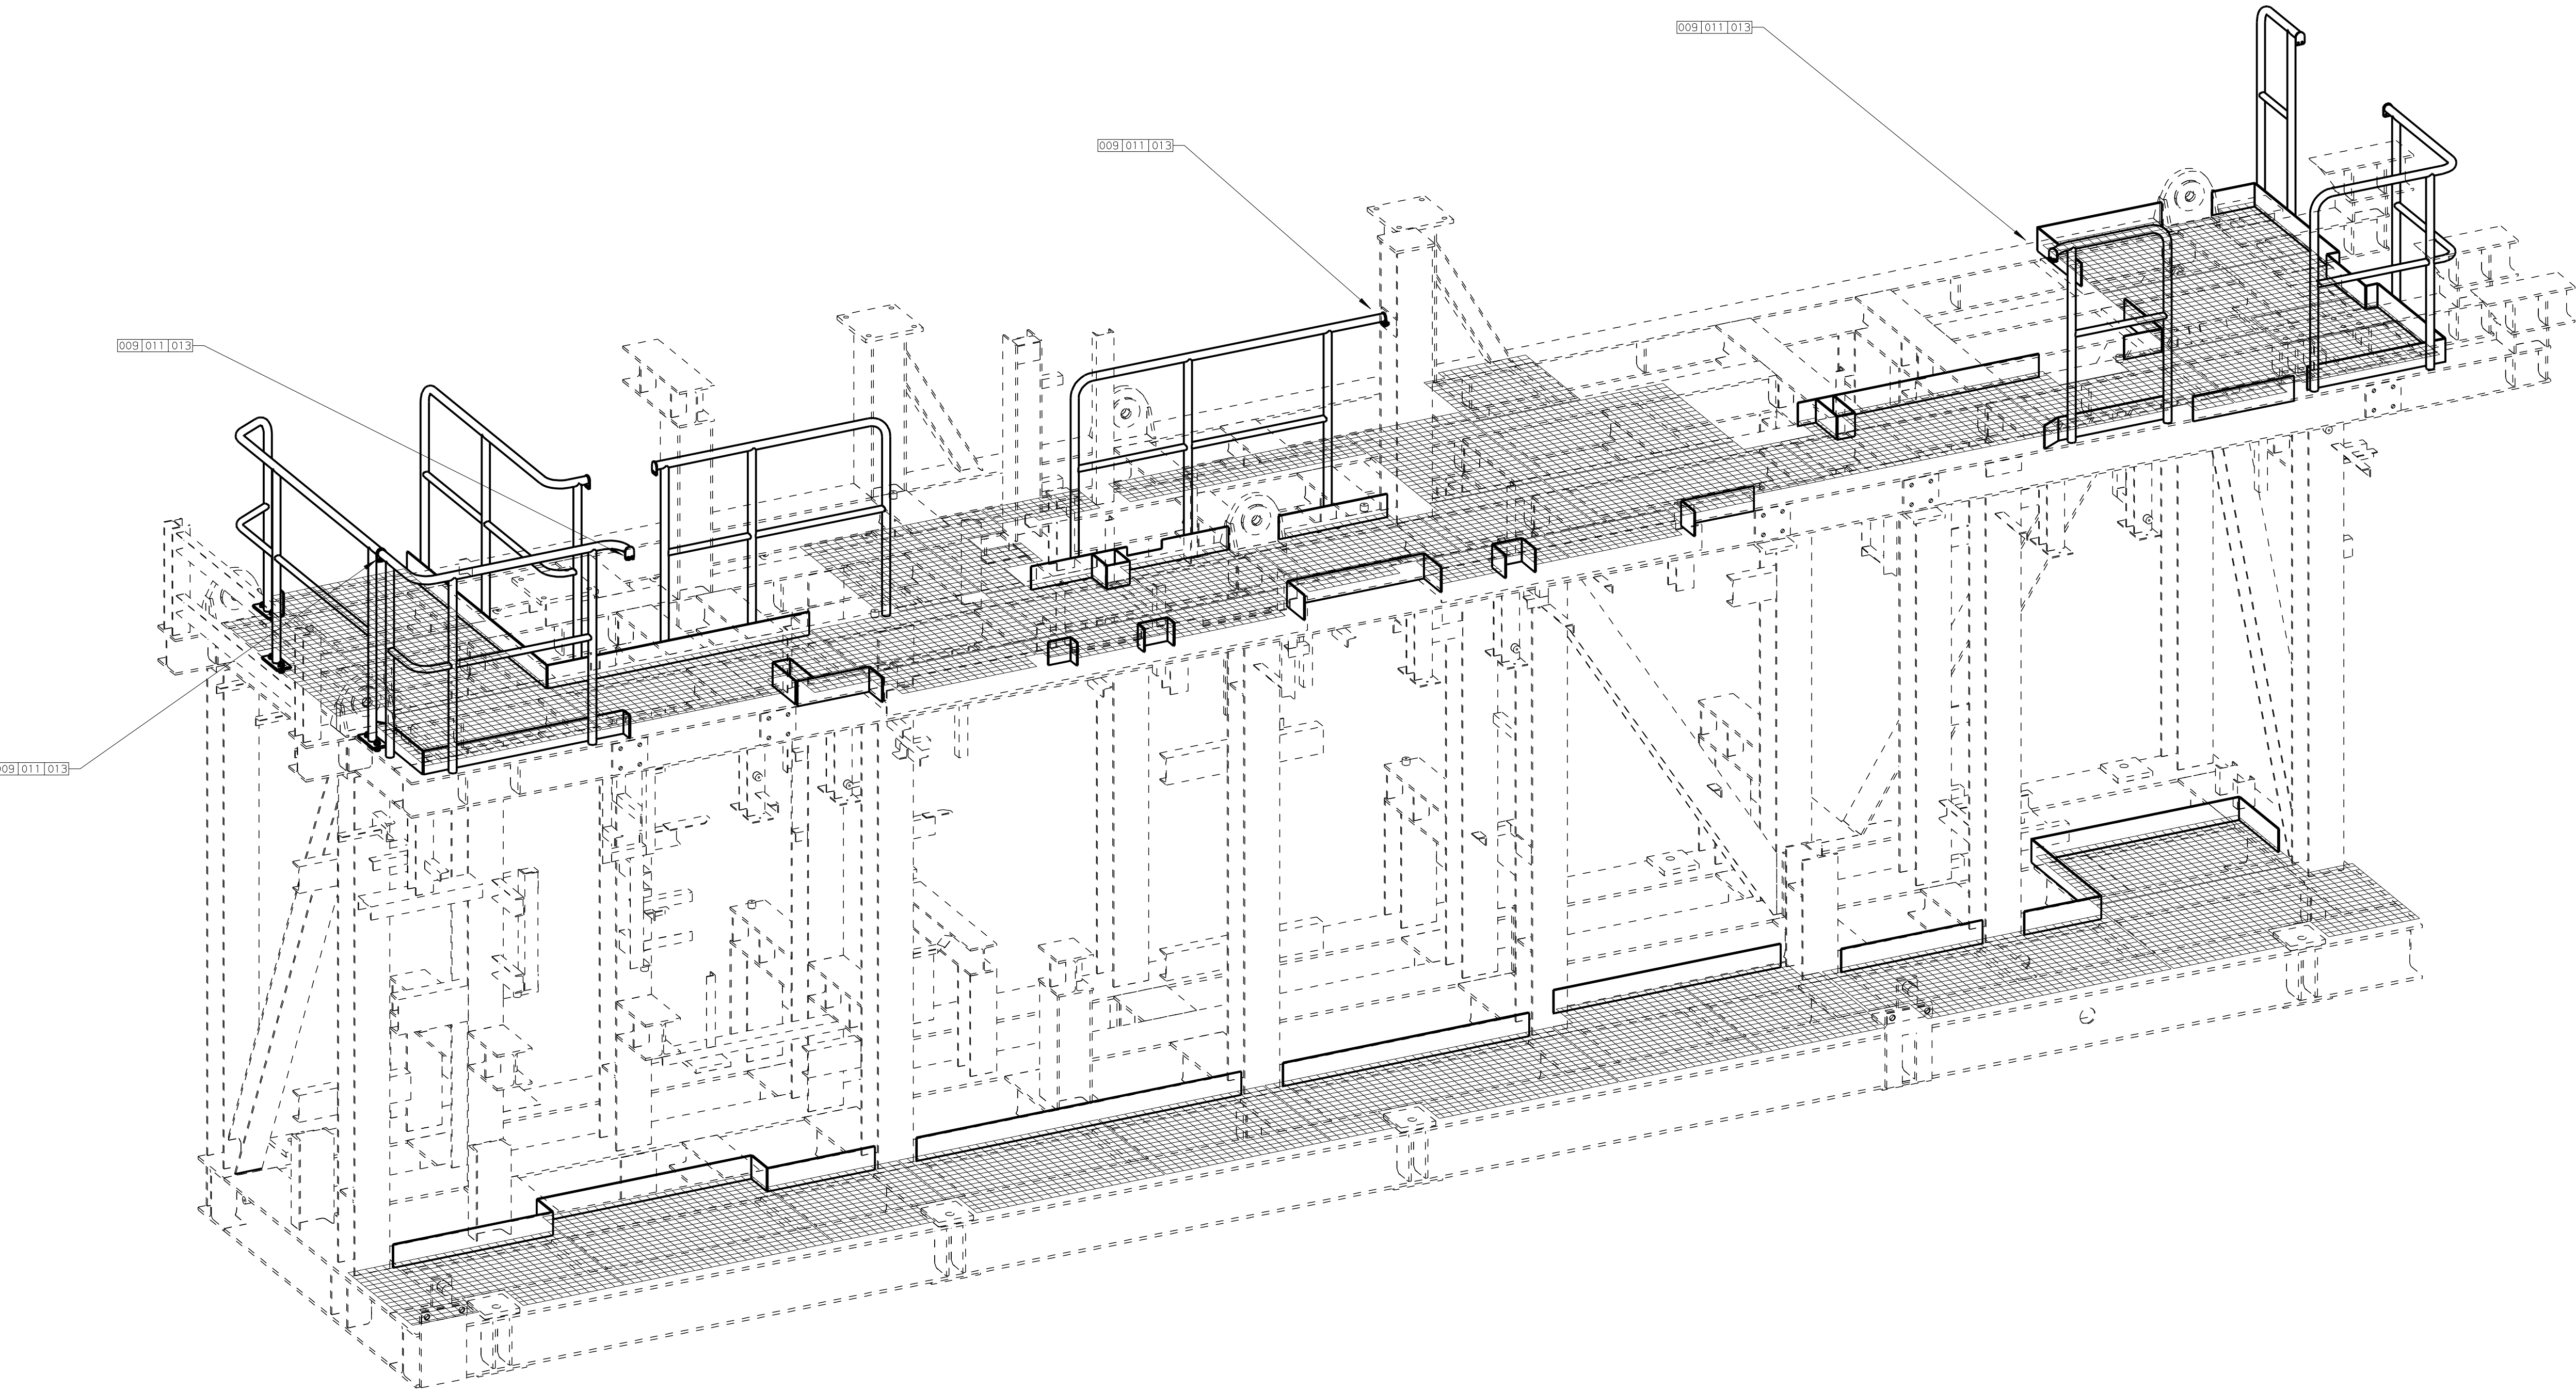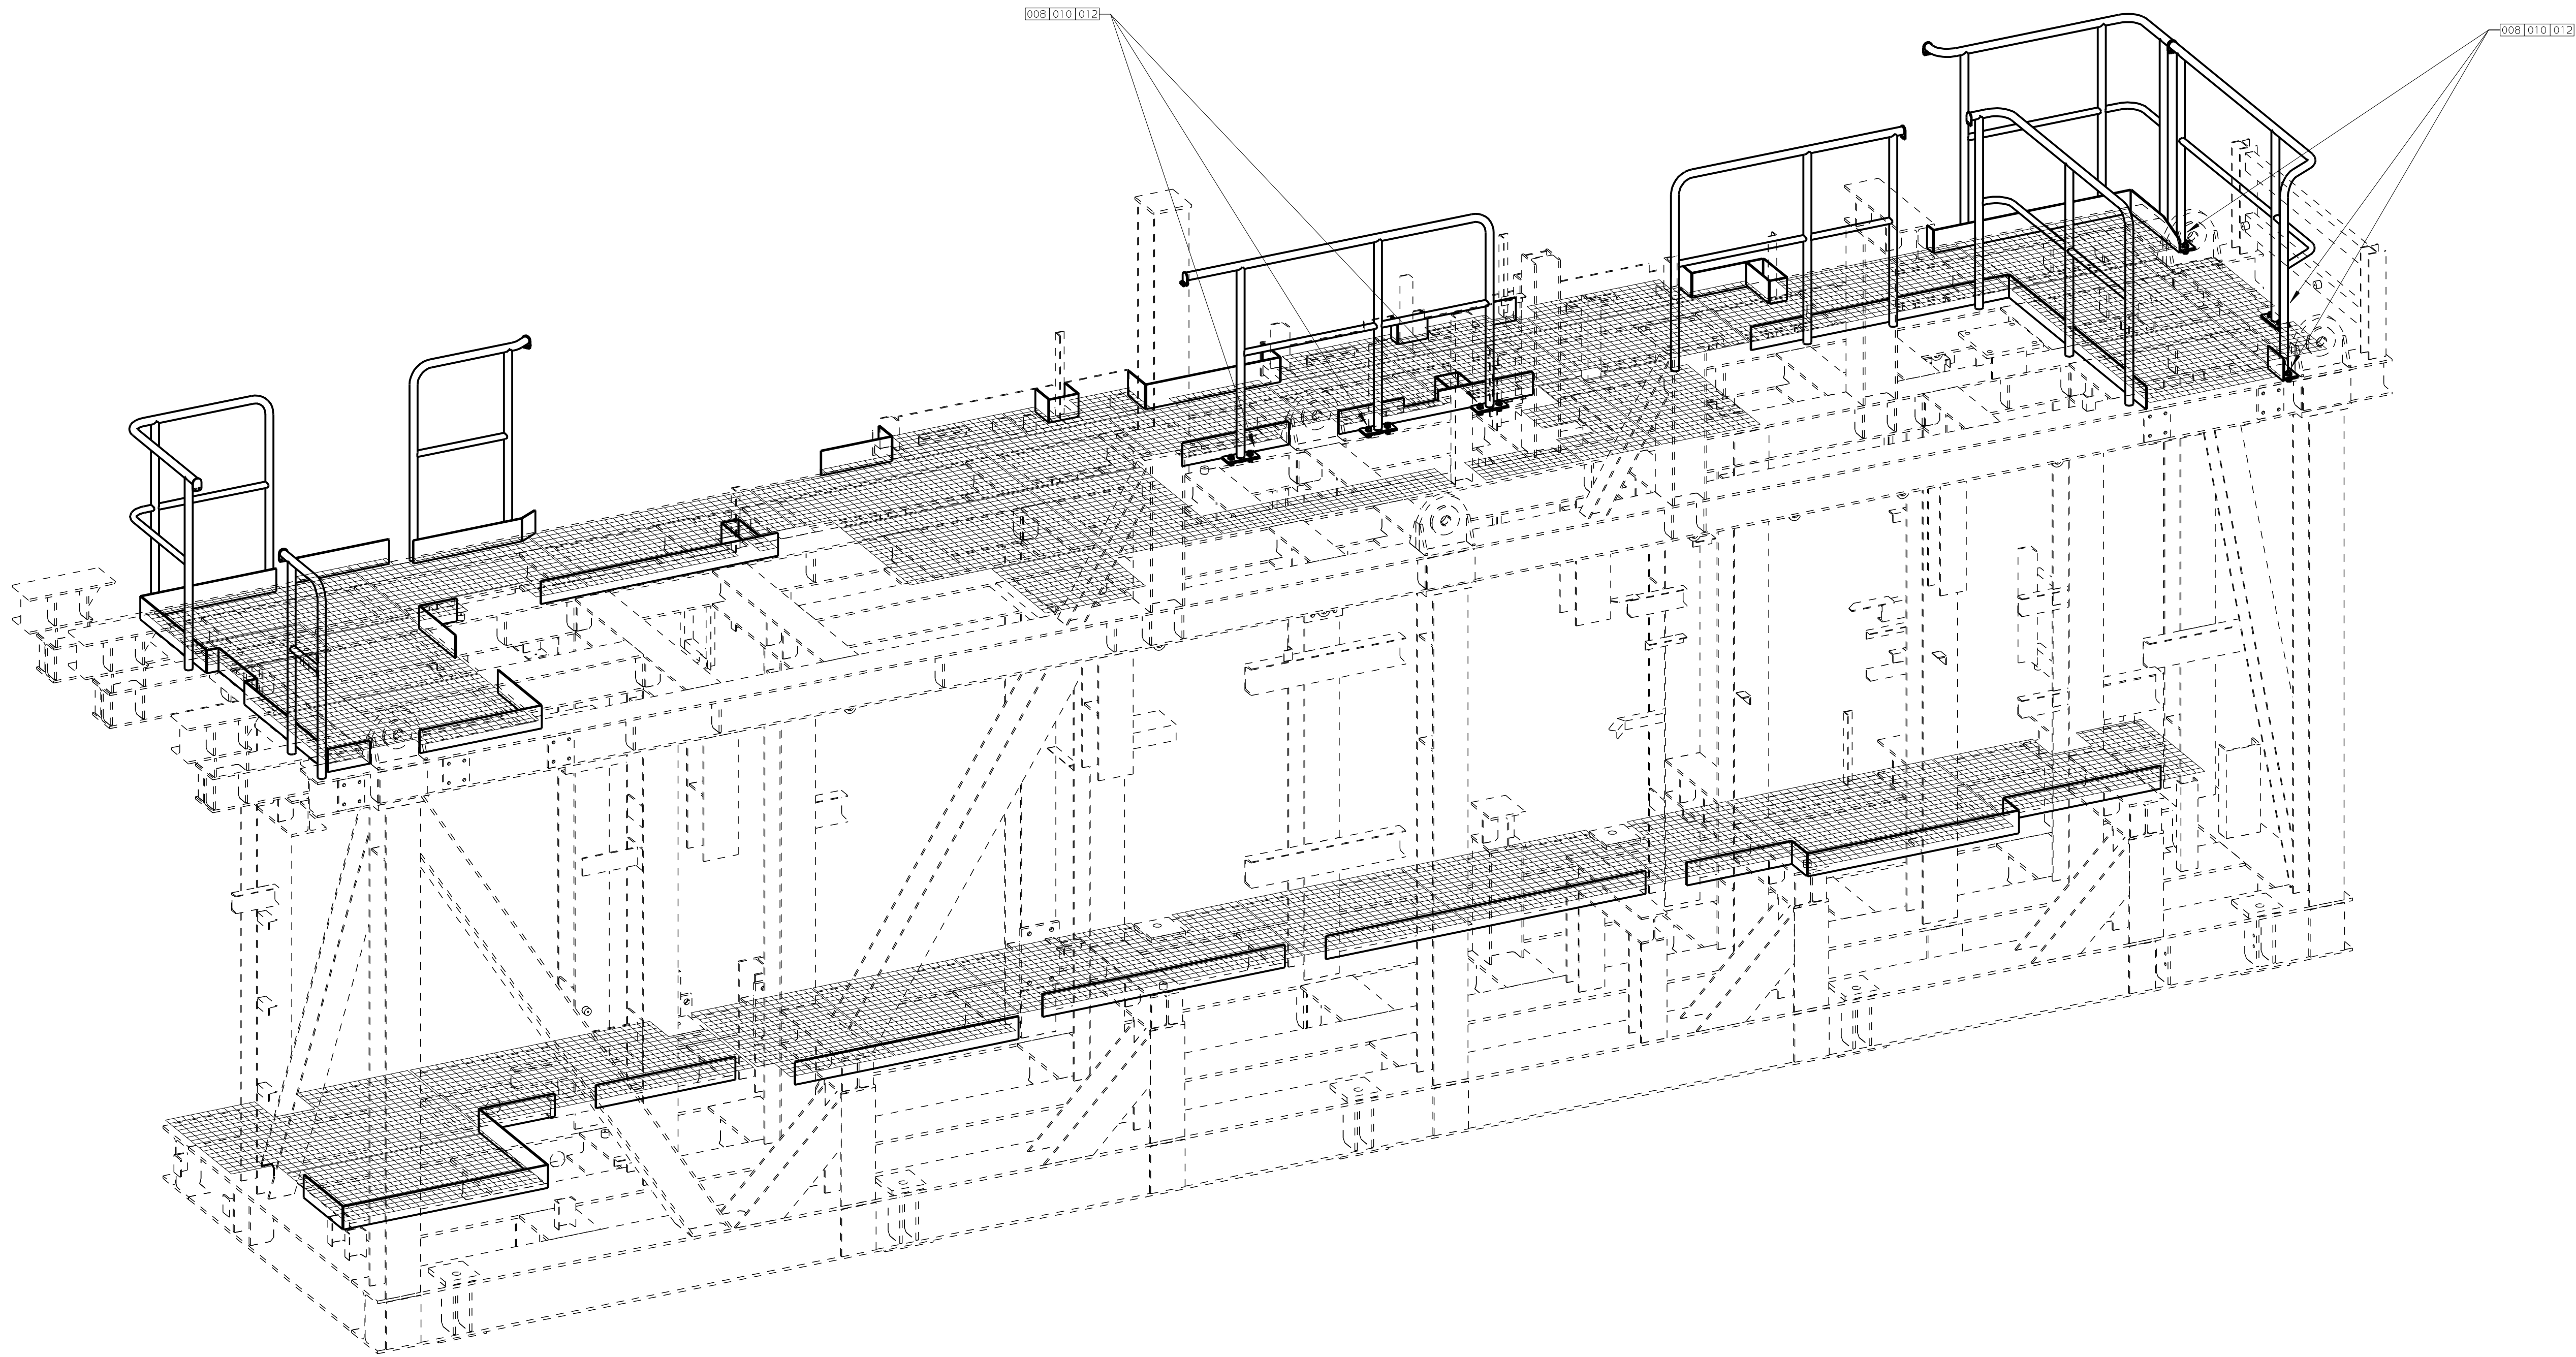


| Execution Code | Number | Pos.No.<br>Code | Designation             | Source of Supply |     | Letter |
|----------------|--------|-----------------|-------------------------|------------------|-----|--------|
| Number:        |        |                 | Material and Remarks    | Approx. mass kg  |     |        |
| 28m            | 001    |                 | FOOT PLATE 6x130        | /                | /   | /      |
|                |        |                 | 55400                   | /                | 170 | /      |
| 2.9m           | 002    |                 | FOOT PLATE 6x140        | /                | /   | /      |
|                |        |                 | 55400                   | /                | 19  | /      |
| 37m            | 003    |                 | PIPE 1 1/4" (SCHED. 10) | /                | /   | /      |
|                |        |                 | A106 GR B ASME B36.10M  | 135              | /   | /      |
| 11m            | 004    |                 | PIPE 1" (SCHED. 10)     | /                | /   | /      |
|                |        |                 | A106 GR B ASME B36.10M  | 40               | /   | /      |
| 26m²           | 005    |                 | GRATING (THK 25)        | /                | /   | /      |
|                |        |                 | /                       | /                | /   | /      |
| 6              | 006    |                 | PLATE 180x80x10         | /                | /   | /      |
|                |        |                 | 55400                   | /                | 1   | /      |
| 8              | 007    |                 | PLATE 70x50x5           | /                | /   | /      |
|                |        |                 | 55400                   | /                | /   | /      |
| 12             | 008    |                 | HEX. HEAD BOLT M16x45   | /                | /   | /      |
|                |        |                 | 8.8 DIN EN ISO 4017     | /                | /   | /      |
| 8              | 009    |                 | HEX. HEAD BOLT M8x25    | /                | /   | /      |
|                |        |                 | 8.8 DIN EN ISO 4017     | /                | /   | /      |
| 12             | 010    |                 | HEX. NUT M16            | /                | /   | /      |
|                |        |                 | 8 DIN EN ISO 4032       | /                | /   | /      |
| 8              | 011    |                 | HEX. NUT M8             | /                | /   | /      |
|                |        |                 | 8 DIN EN ISO 4032       | /                | /   | /      |
| 24             | 012    |                 | WASHER (M16)            | /                | /   | /      |
|                |        |                 | / ISO 7089-16-200 HV    | /                | /   | /      |
| 16             | 013    |                 | WASHER (M8)             | /                | /   | /      |
|                |        |                 | / ISO 7089-8-200 HV     | /                | /   | /      |
| APPROX. WEIGHT |        |                 |                         | ≈                | 375 | Kg     |

NOTE:  
1) ALL LISTE MATERIAL ARE WITHOUT ALLOWANCE.





|                  |           |                           |           |                      |           |            |           |            |
|------------------|-----------|---------------------------|-----------|----------------------|-----------|------------|-----------|------------|
| Rev. / Changes   | A         |                           | B         |                      | C         |            | D         |            |
|                  | TONELLI_M | 14-01-2022                | TONELLI_M | 20-01-2022           | TONELLI_M | 21-12-2024 | TONELLI_M | 20-02-2024 |
| Name             |           | Date                      | Name      |                      | Date      | Name       |           | Date       |
| Supp. parts list |           | Design group              |           |                      |           |            |           |            |
| Replaced by      |           | Subst. for                |           | Orig. scale          |           | 1:20       |           |            |
| SLP250V-SA       |           | STEEL STRUCTURE           |           | Drawn: 14-04-2022    |           | TONELLI_M  |           |            |
| L-0184           |           | M3 RAILING AND GRATING    |           | Verified: 08-03-2024 |           | SABOGAL_M  |           |            |
| ASME             |           | LABY-G10 - NON-LUBE COMP. |           | Standards comply:    |           |            |           |            |
| CAD-Drawing      |           | Part-No.                  |           | Bar - Code           |           |            |           |            |
|                  |           | E                         |           | 0-125.619.977        |           | 1 - 4      |           |            |

TYPICAL FOR  
POS 001 FOOT PLATE  
(SCALE 1:5)

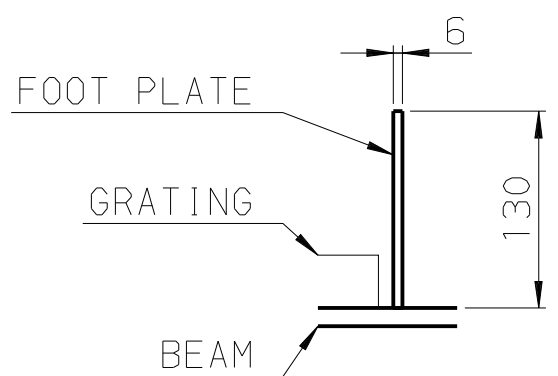

TYPICAL FOR  
POS 002 FOOT PLATE  
(SCALE 1:5)

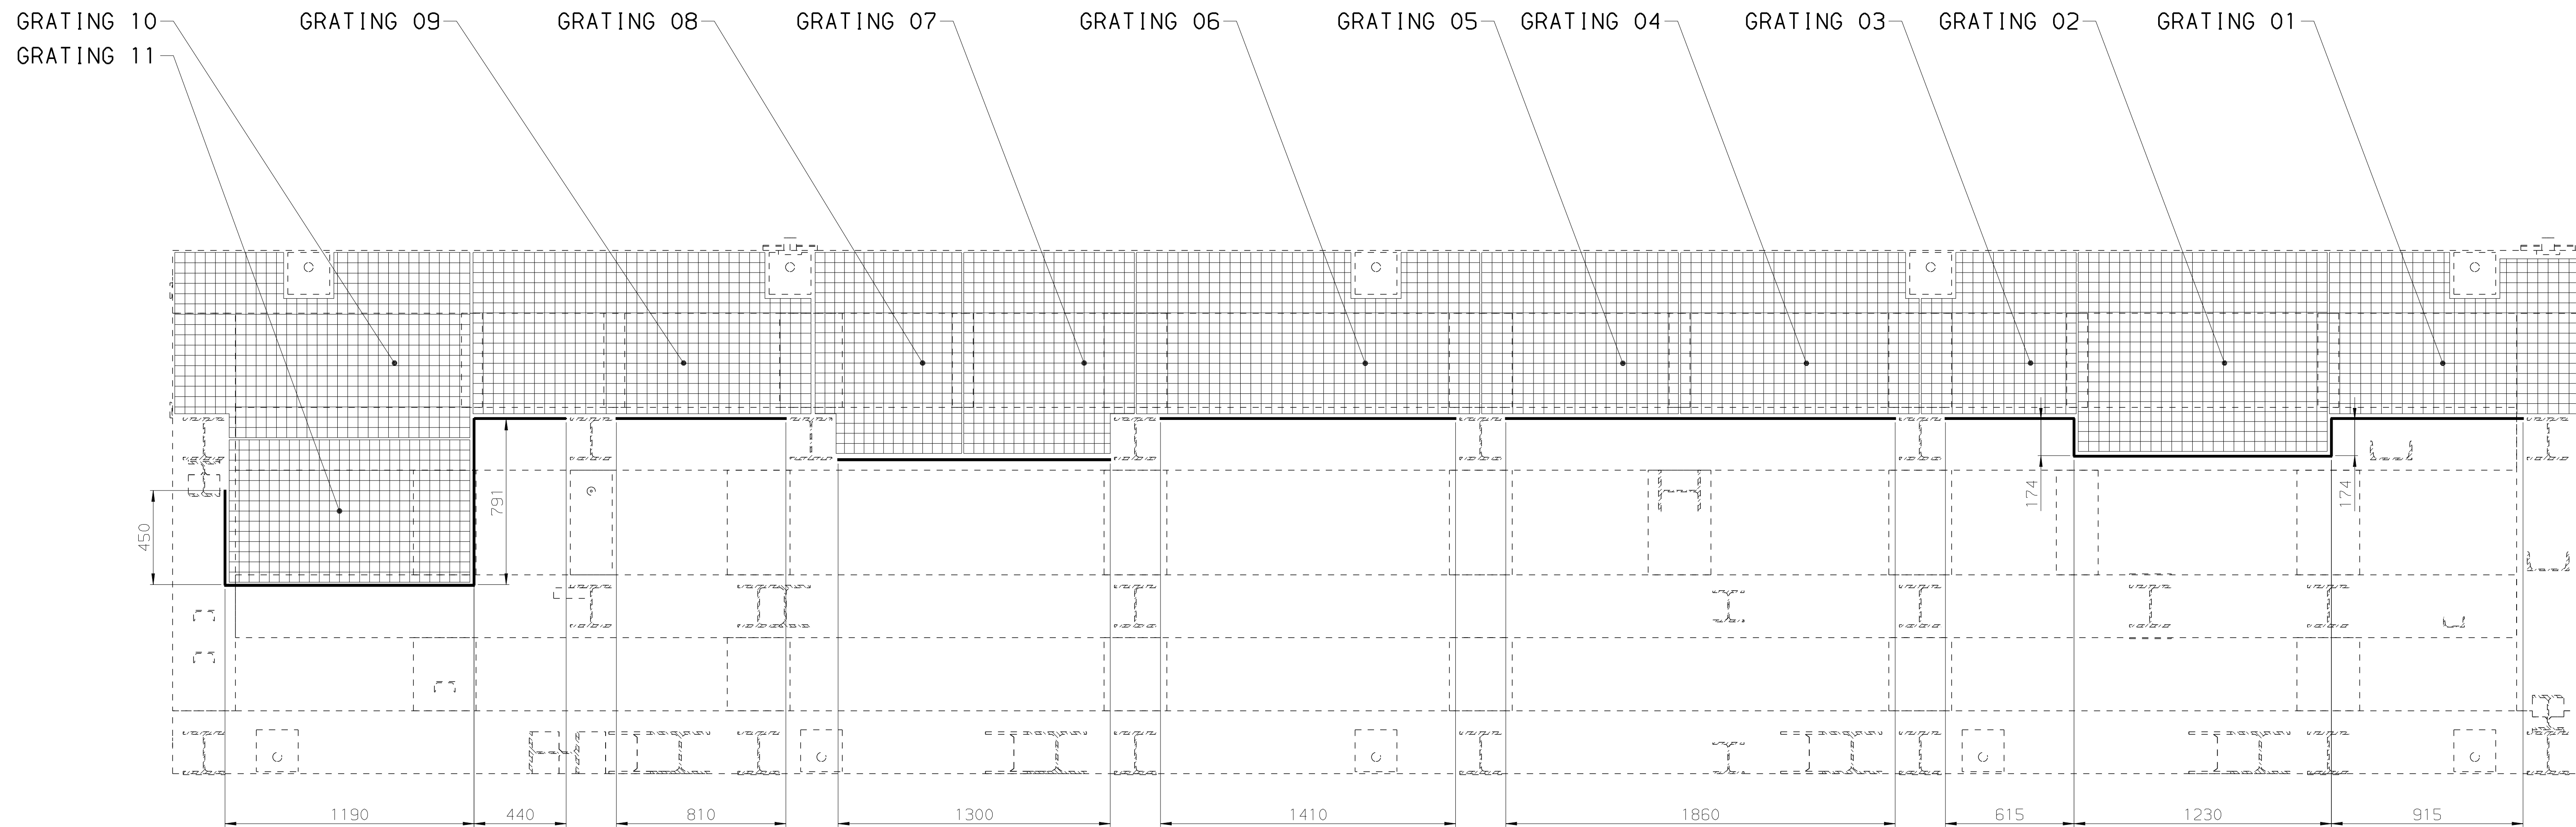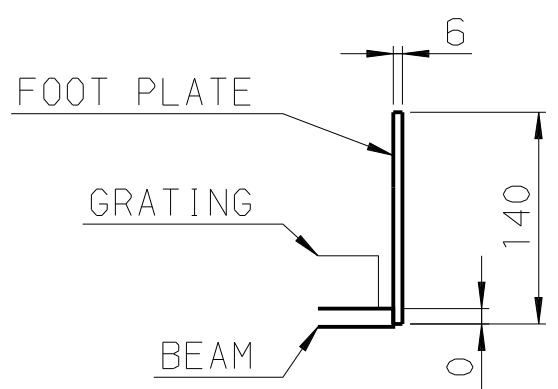


|   |          |   |               |   |                      |      |
|---|----------|---|---------------|---|----------------------|------|
| No.   | Revision | (a)   | (b)           | (c)   | (d)                  | Date |
|   |          | TONELLI_M   | TONELLI_M     | TONELLI_M   | TONELLI_M            |      |
|   |          | 11-17-2021   | 20-08-2021    | 21-12-2021   | 21-12-2021           |      |
|   |          | Name   | Name          | Name   | Name                 |      |
| Supp. parts list   |          | Design group   |               |   |                      |      |
| Replaced by   |          | Subst. for   |               | Orig. scale 1:15   |                      |      |
| SLP250V-SA   |          | <b>STEEL STRUCTURE</b><br><b>M3 RAILING AND GRATING</b><br><b>LABY-610 - NON-LUBE COMP.</b><br><b>ITEM NO.: C-001</b> |               |   | Drawn: 19-04-2022    |      |
|   |          |   |               |   | TONELLI_M            |      |
|   |          |   |               |   | Verified: 08-03-2022 |      |
| L-0184<br>ASME   |          |   |               |   | SABOGAL_A            |      |
|   |          |   |               |   | Standards conform:   |      |
| CAD-Drawing   |          | Part-No.   | Bar - Code    |   |                      |      |
|  <b>Burckhardt Compression</b> |          | E   | 0-125.619.977 |   | 2 - d                |      |
|   |          |   |               |   | 4                    |      |

This drawing is entrusted to the recipient personally, but the copyright remains with us. It must not be copied, reproduced or in any way communicated or made accessible to third parties without our written consent.


Similar Drug.

Machining regulations see Drawing Standards,

RAILING 1 REMOVABLE FOR MODULE LIFTING  
AND TRANSPORT




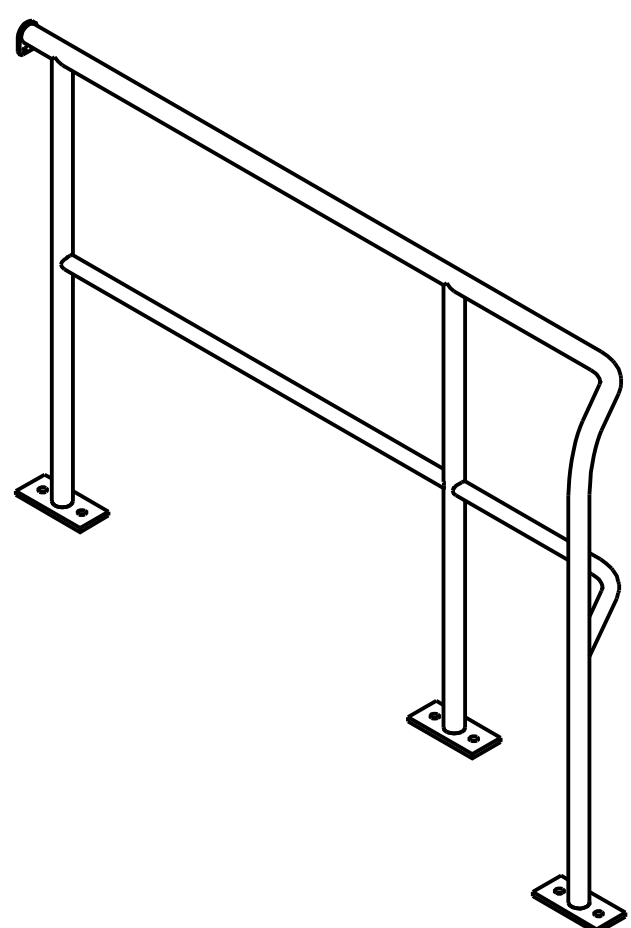


RAILING 4 REMOVABLE FOR MODULE LIFTING  
AND TRANSPORT



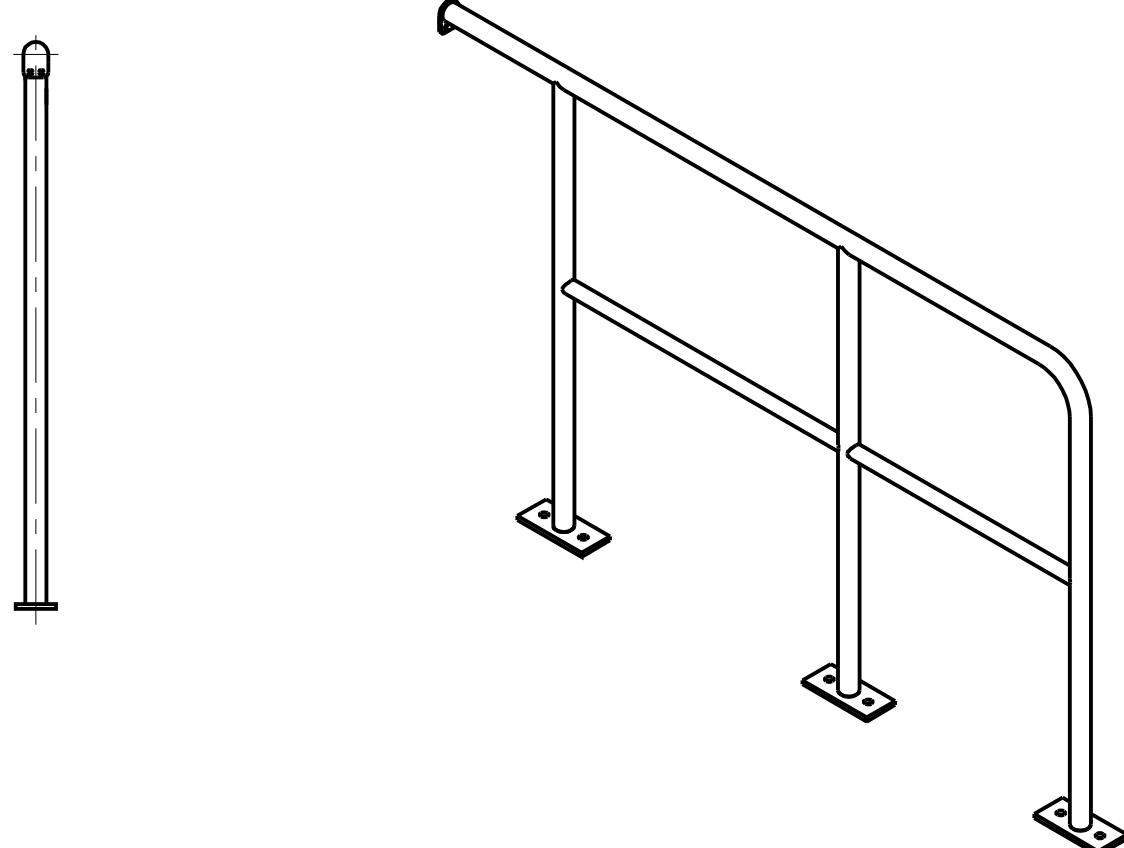


Technical drawing of a railing section. The drawing shows a side view of a railing with a vertical post and a horizontal rail. The dimensions are as follows:

- Overall width: 830
- Distance from left edge to center of post: 165
- Distance from center of post to right edge: 665
- Post diameter:  $\phi 42.2$
- Horizontal rail diameter:  $\phi 42.2$
- Vertical post diameter:  $\phi 33.4$
- Radius of the top corner: R100
- Callout 004 points to the horizontal rail.
- Callout 003 points to the vertical post.

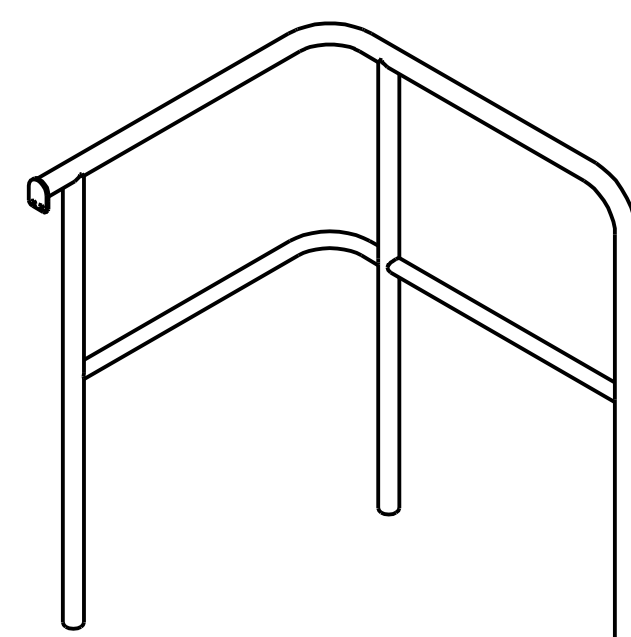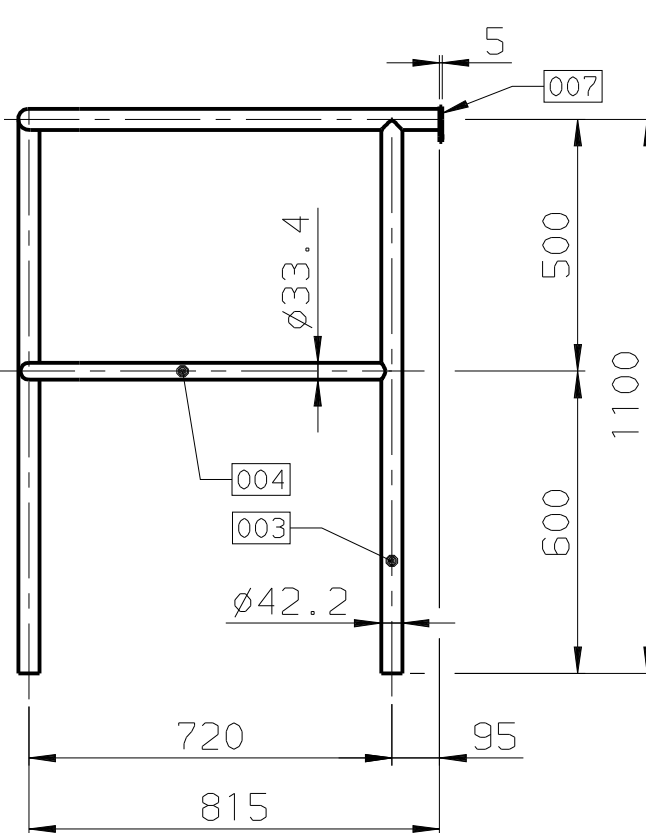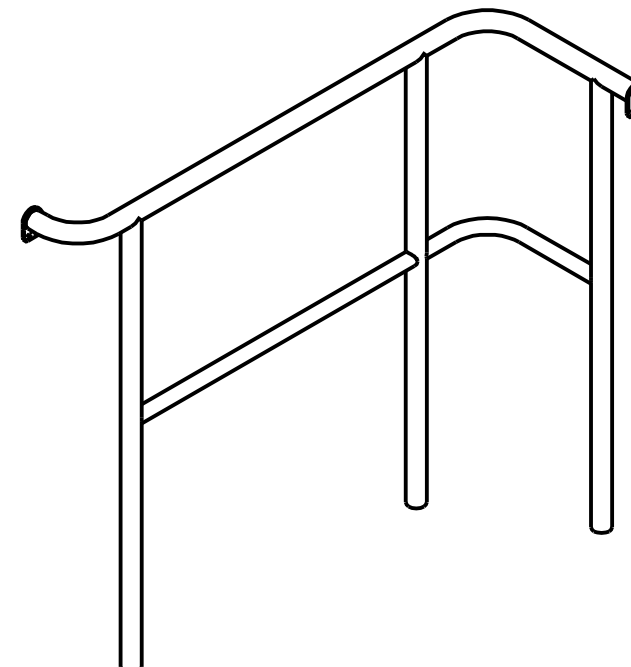
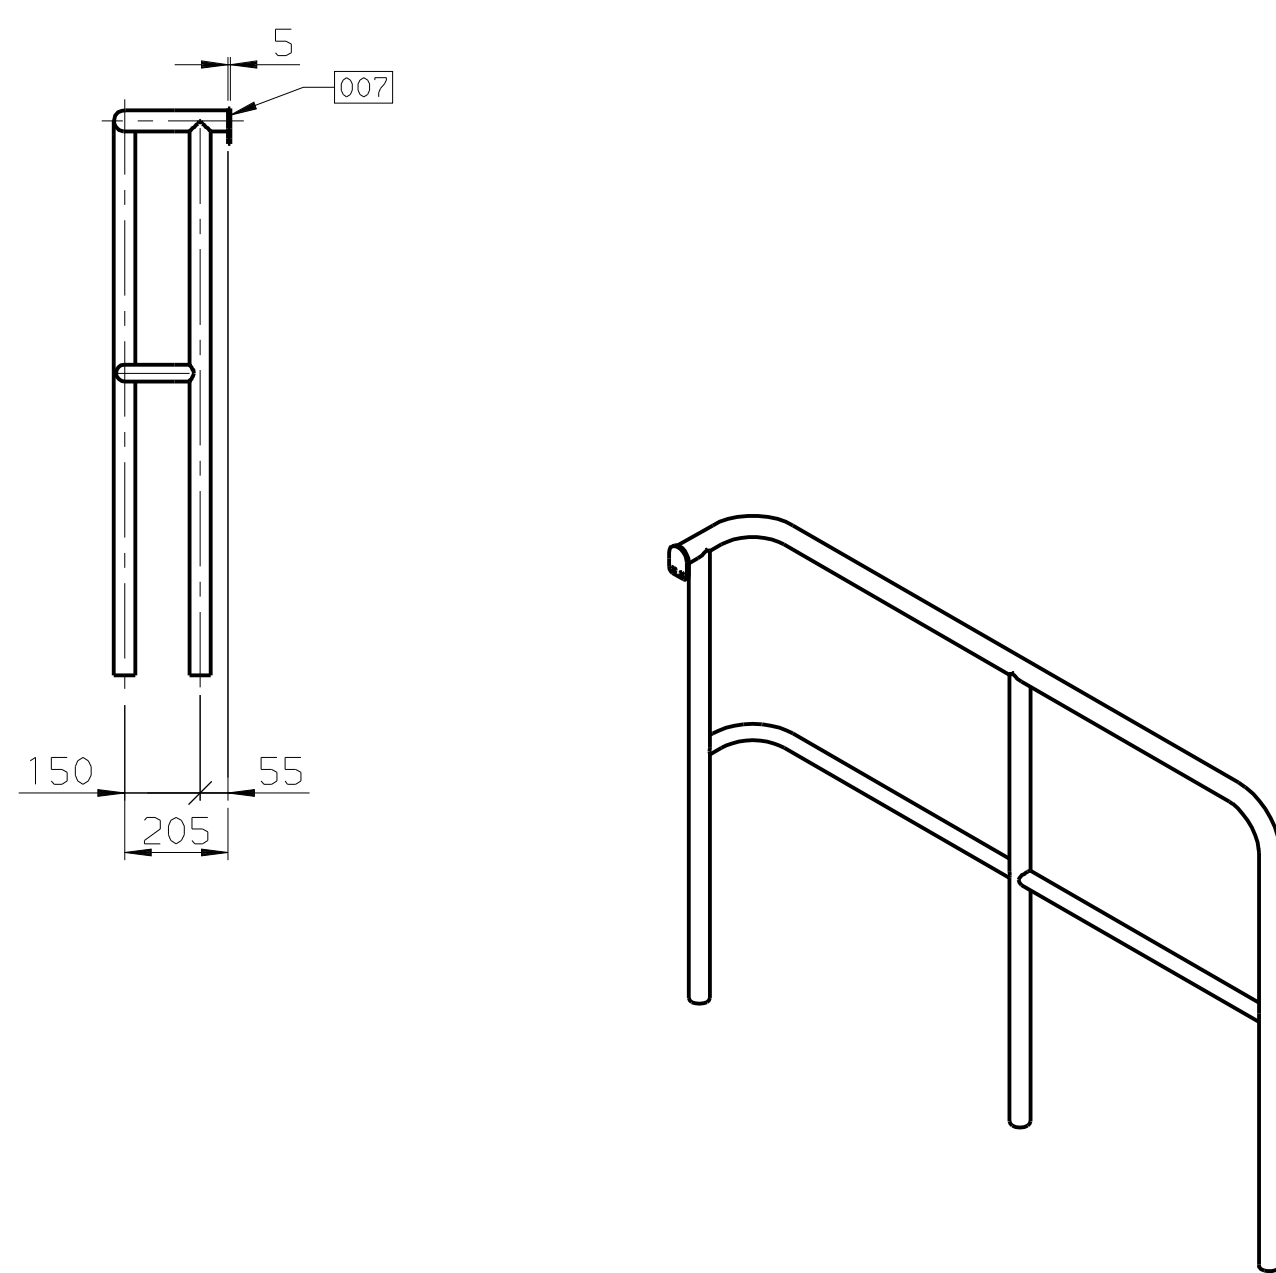
[illegible]

Technical drawing of a vertical support structure. The drawing shows a side view of a component with a total height of 1100. The main body has a height of 500, and the base has a height of 600. The base is a rectangular plate with a width of 445, divided into a 95 section on the left and a 350 section on the right. The base plate has four mounting holes, each with a diameter of  $\phi 42.2$ . The main body has a top flange with a width of 5 and a height of 500. The flange has a central hole with a diameter of  $\phi 33.4$  and a smaller hole with a diameter of  $\phi 42.2$ . The top flange has a rounded corner with a radius of  $R100$ . Callouts 007, 004, 003, and 002 point to specific features: 007 points to the top flange, 004 points to the central hole, 003 points to the base plate, and 002 points to the mounting holes.

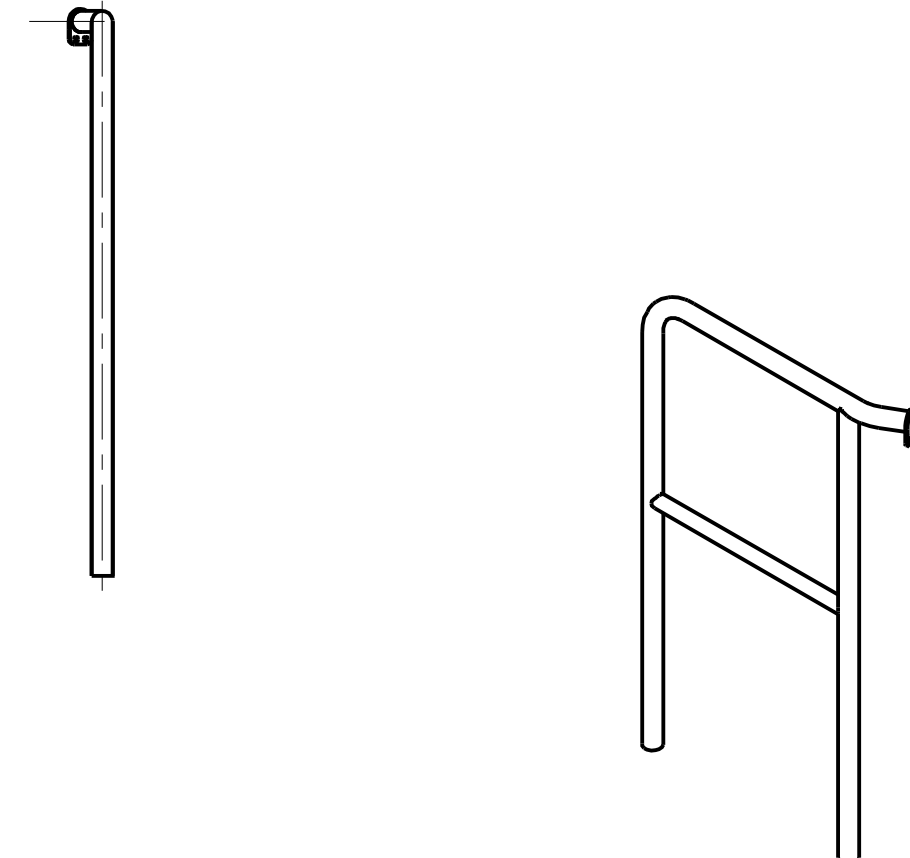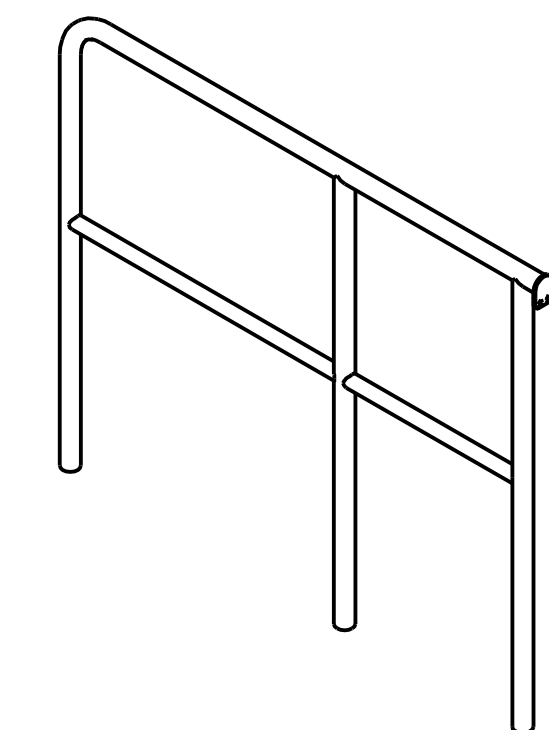
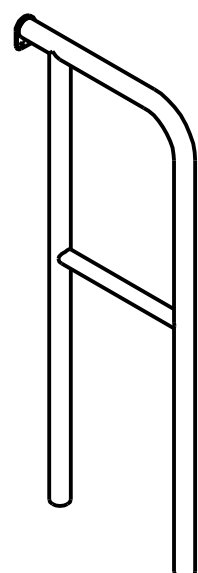


|   |   |   |   |   |
|---|---|---|---|---|
| <br>North direction                | <br>a) TONELL1_M | <br>b) TONELL1_M                 | <br>c) TONELL1_M | <br>d) TONELL1_M |
|   | Name _____<br>Date: 14-07-2024                                                                        | Name _____<br>Date: 20-08-2024                                                                                        | Name _____<br>Date: 21-12-2024                                                                        | Name _____<br>Date: 20-02-2025                                                                        |
| Sep. parts list<br>Replaced by _____                                                                                    |   | Design group _____<br>Subst. for _____                                                                                |   | Orig. scale 1:15                                                                                      |
| SLP250V-5A<br><br>L-0184<br>ASME                                                                                        |   | <b>STEEL STRUCTURE</b><br><b>M3 RAILING AND GRATING</b><br><b>LABY-G1ø - NON-LUBE COMP.</b><br><b>ITEM NO.: C-001</b> |   | Drawn: 14-07-2024<br>TONELL1_M<br><br>Verifed: 08-03-2024<br>SABOGAL_A<br><br>Standards<br>conforms   |
| CAD-Drawing   |   | Part-No. _____   | Bar - Code _____                                                                                      |   |
|  <b>Burckhardt<br/>Compression</b> |   | <b>E</b>   | <b>0-125.619.977</b>                                                                                  | <b>4 - d</b><br><b>d</b>                                                                              |

RAILING LOOSE 1

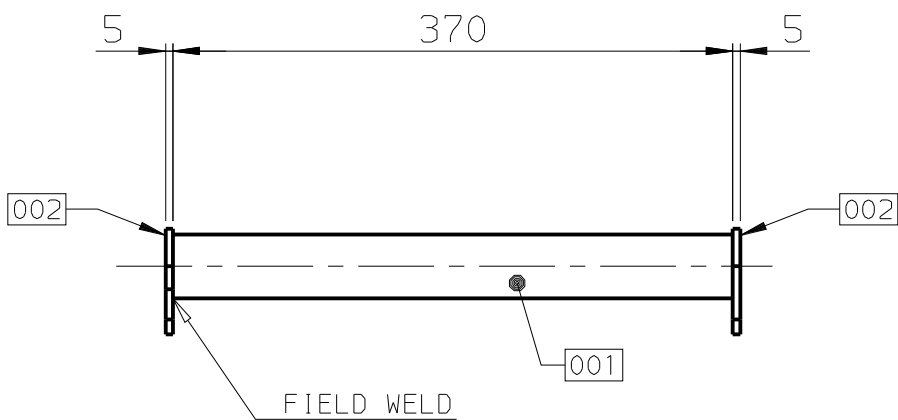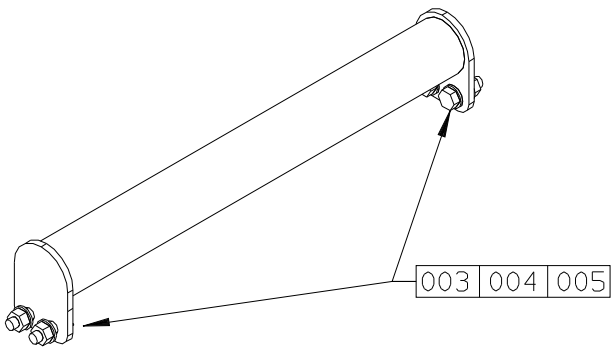

RAILING LOOSE 2 (QTY2)

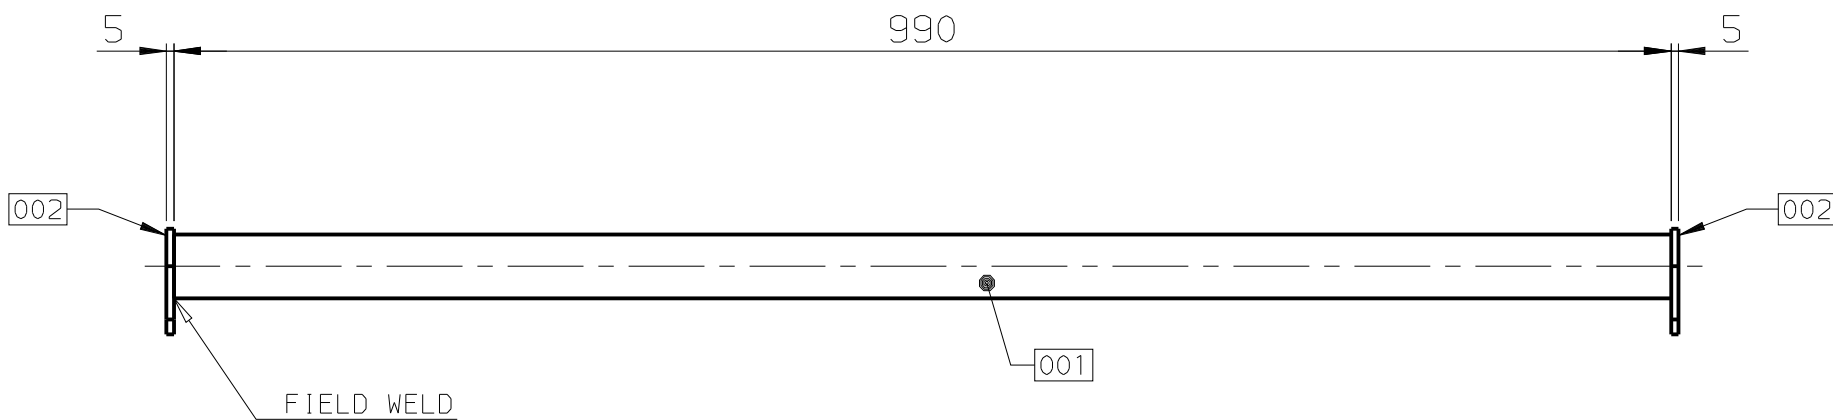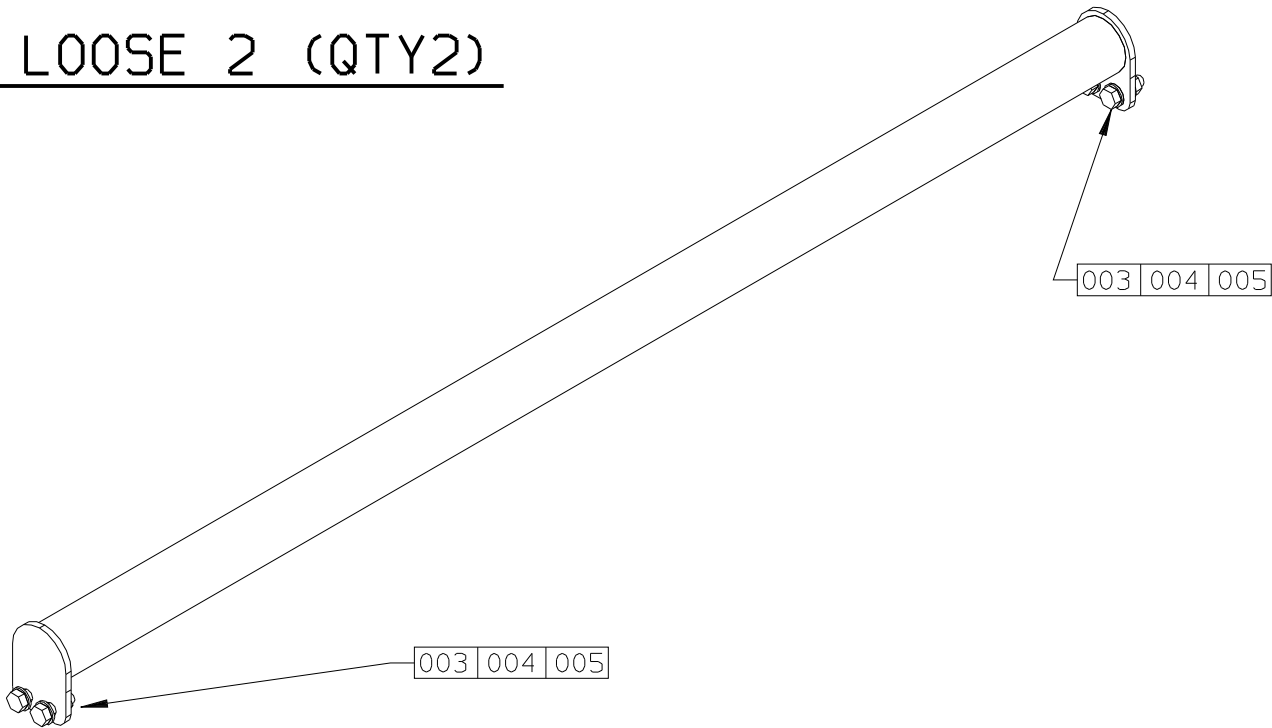


| Execution Code Number |     |                        |  | Pos.No.<br>Code | Designation          | Source of<br>Supply   | Mod.   |
|-----------------------|-----|------------------------|--|-----------------|----------------------|-----------------------|--------|
| Number OFF            |     |                        |  |                 | Material and Remarks | Approx.<br>mass kg/pc | Letter |
| 2.4m                  | 001 | PIPE 1 1/4" (SCHED.10) |  |                 |                      | /                     | / /    |
|                       |     | A106 GR B ASME B36.10M |  |                 |                      | 8                     | / /    |
| 6                     | 002 | PLATE 70x50x5          |  |                 |                      | /                     | / /    |
|                       |     | SS400                  |  |                 |                      | 1                     | / /    |
| 12                    | 003 | HEX. HEAD BOLT M8x25   |  |                 |                      | /                     | / /    |
|                       |     | 8.8 DIN EN ISO 4017    |  |                 |                      | /                     | / /    |
| 12                    | 004 | HEX. NUT M8            |  |                 |                      | /                     | / /    |
|                       |     | 8 DIN EN ISO 4032      |  |                 |                      | /                     | / /    |
| 24                    | 005 | WASHER (M8)            |  |                 |                      | /                     | / /    |
|                       |     | / ISO 7089-8-200 HV    |  |                 |                      | /                     | / /    |
| APPROX WEIGHT         |     |                        |  |                 |                      | 9                     | Kg     |

NOTE:  
1) ALL LISTE MATERIAL ARE WITHOUT ALLOWANCE.

POS 002

THICKNESS 5mm  
(SCALE 1:5)

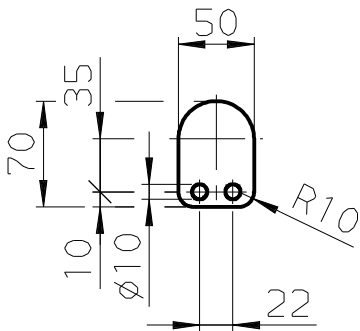

Documentation shall be deemed to be approved unless commented and/or rejected within 14 days


This drawing is entrusted to the recipient personally, but the copyright remains with us. It must not be copied, reproduced or in any way communicated or made accessible to third parties without our written consent.

Similar Drwg.


Machining regulations see Drawing Standards.

|                |                                  |                                                                                  |               |                       |      |                       |                   |                                 |      |  |
|----------------|----------------------------------|----------------------------------------------------------------------------------|---------------|-----------------------|------|-----------------------|-------------------|---------------------------------|------|--|
| Modifications  | <input type="radio"/>            |                                                                                  |               | <input type="radio"/> |      | <input type="radio"/> |                   | <input type="radio"/>           |      |  |
|                | <input checked="" type="radio"/> | TONELLI_M                                                                        | 18-07-2022    | <input type="radio"/> |      | <input type="radio"/> |                   | <input type="radio"/>           |      |  |
|                |                                  | Name                                                                             | Date          |                       | Name | Date                  |                   | Name                            | Date |  |
| Sep.parts List |                                  |                                                                                  | Design group  |                       |      |                       |                   |                                 |      |  |
| Replaced by    |                                  |                                                                                  | Subst. for    |                       |      |                       | Orig. scale 1:5 , |                                 |      |  |
| SLP250V-5A     |                                  | STEEL STRUCTURE<br>RAILING LOOSE<br>LABY-GI● - NON-LUBE COMP.<br>ITEM NO.: C-001 |               |                       |      |                       |                   | Drawn: 14-04-2022<br>TONELLI_M  |      |  |
| L-0184<br>ASME |                                  |                                                                                  |               |                       |      |                       |                   | Verified: 25-07-2022<br>ZUBER_R |      |  |
|                |                                  |                                                                                  |               |                       |      | Standards conform:    |                   |                                 |      |  |
| CAD-Drawing    |                                  | Part-No.                                                                         | Bar - Code    |                       |      |                       |                   |                                 |      |  |
|                |                                  | E                                                                                | 2-125.619.985 |                       |      |                       |                   | 1 - 1<br>a                      |      |  |

LOOSE-RAIL-5  
1:15

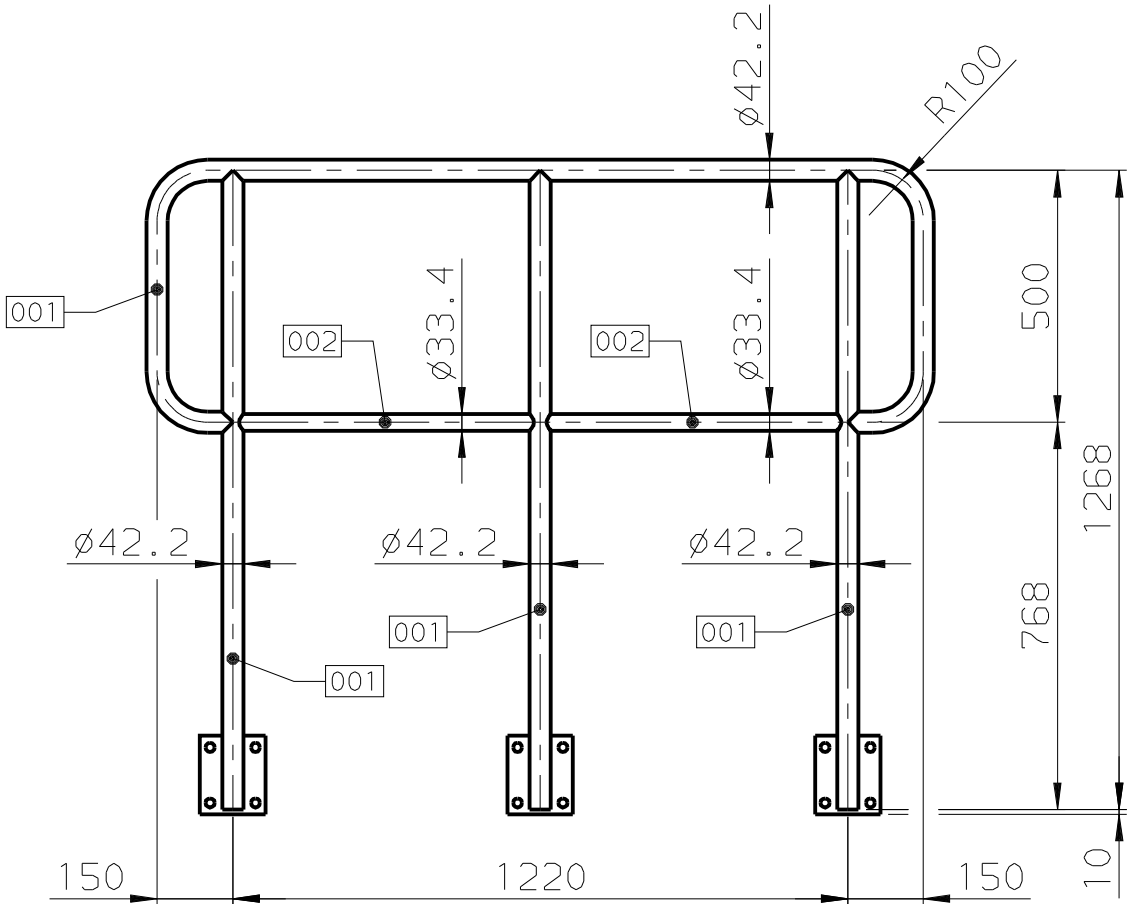


LOOSE-RAIL-5  
1:15

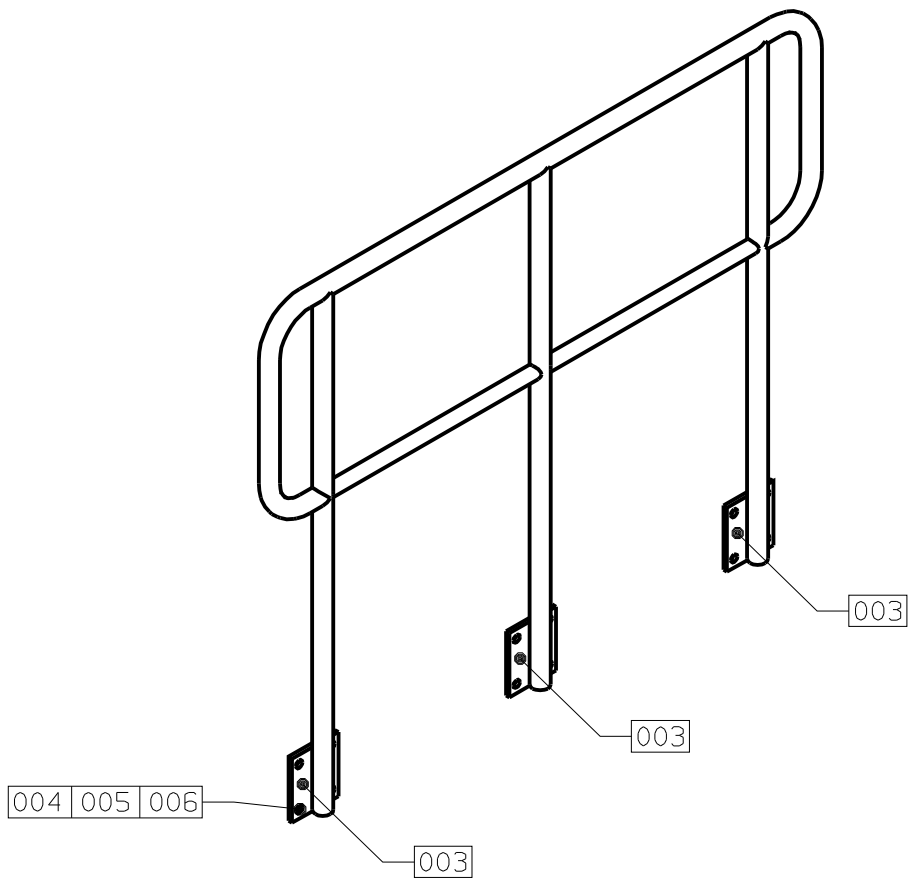

P05 003

THICKNESS 10mm  
(SCALE 1:5)

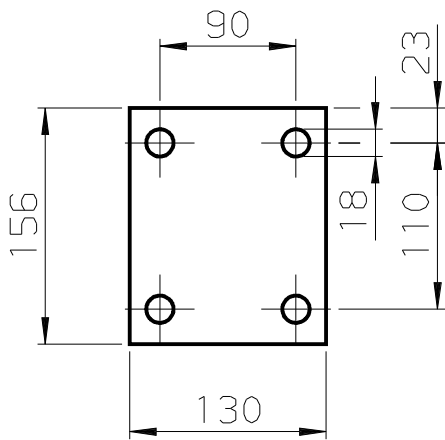

This drawing is entrusted to the recipient personally, but the copyright remains with us. It must not be copied, reproduced or in any way communicated or made accessible to third parties without our written consent.

Similar Drwg.

Machining regulations see Drawing Standards.

| Execution Code Number |     |                                  |  | Pos.No.<br>Code | Designation          | Source of<br>Supply   | Mod.   |    |   |
|-----------------------|-----|----------------------------------|--|-----------------|----------------------|-----------------------|--------|----|---|
| Number OFF            |     |                                  |  |                 | Material and Remarks | Approx.<br>mass kg/pc | Letter |    |   |
| 7m                    | 001 | PIPE 1 1/4" (SCHED.10)           |  |                 |                      | /                     | /      | /  |   |
|                       |     | A106 GR B ASME B36.10M           |  |                 |                      | 22                    | /      | /  |   |
| 1.5m                  | 002 | PIPE 1" (SCHED.10)               |  |                 |                      | /                     | /      | /  |   |
|                       |     | A106 GR B ASME B36.10M           |  |                 |                      | 4                     | /      | /  |   |
| 3                     | 003 | PLATE 156x130x10                 |  |                 |                      | /                     | /      | /  |   |
|                       |     | SS400                            |  |                 |                      | /                     | 2      | /  | / |
| 12                    | 004 | HEX. HEAD BOLT W/SHANK M16x50/38 |  |                 |                      | /                     | /      | /  |   |
|                       |     | 8.8 DIN EN ISO 4014              |  |                 |                      | /                     | /      | /  |   |
| 12                    | 005 | HEX. NUT M16                     |  |                 |                      | /                     | /      | /  |   |
|                       |     | 8 DIN EN ISO 4032                |  |                 |                      | /                     | /      | /  |   |
| 24                    | 006 | WASHER (M16)                     |  |                 |                      | /                     | /      | /  |   |
|                       |     | / ISO 7089-16-200 HV             |  |                 |                      | /                     | /      | /  |   |
| APPROX WEIGHT         |     |                                  |  |                 |                      | ≈                     | 32     | Kg |   |

NOTE:  
1) ALL LISTE MATERIAL ARE WITHOUT ALLOWANCE.



Documentation shall be deemed to be approved unless commented and/or rejected within 14 days

|   |                |                                                                                       |      |               |  |      |      |                    |  |      |      |                                   |   |      |      |  |
|---|----------------|---------------------------------------------------------------------------------------|------|---------------|--|------|------|--------------------|--|------|------|-----------------------------------|---|------|------|--|
| Modifications   |                |                                                                                       |      |               |  |      |      |                    |  |      |      |                                   |   |      |      |  |
|   |                |                                                                                       |      |               |  |      |      |                    |  |      |      |                                   |   |      |      |  |
|   |                | Name                                                                                  | Date |               |  | Name | Date |                    |  | Name | Date |                                   |   | Name | Date |  |
|   | Sep.parts List |                                                                                       |      | Design group  |  |      |      |                    |  |      |      |                                   |   |      |      |  |
| Replaced by   |                |                                                                                       |      | Subst. for    |  |      |      | Orig. scale 1:15 , |  |      |      |                                   |   |      |      |  |
| SLP250V-5A   |                | STEEL STRUCTURE<br>RAILING FOR M3<br><br>LABY-GI● - NON-LUBE COMP.<br>ITEM NO.: C-001 |      |               |  |      |      |                    |  |      |      | Drawn: 23-01-2023<br>TONELLI_M    |   |      |      |  |
| L-0184<br>ASME   |                |                                                                                       |      |               |  |      |      |                    |  |      |      | Verified: 10-03-2023<br>SABOGAL_A |   |      |      |  |
|   |                |                                                                                       |      |               |  |      |      |                    |  |      |      | Standards conform:                |   |      |      |  |
| CAD-Drawing   |                | Part-No.                                                                              |      | Bar - Code    |  |      |      |                    |  |      |      |                                   |   |      |      |  |
|  <b>Burckhardt<br/>Compression</b> |                | E                                                                                     |      | 2-125.622.142 |  |      |      |                    |  |      |      | 1 - 1                             |   |      |      |  |